
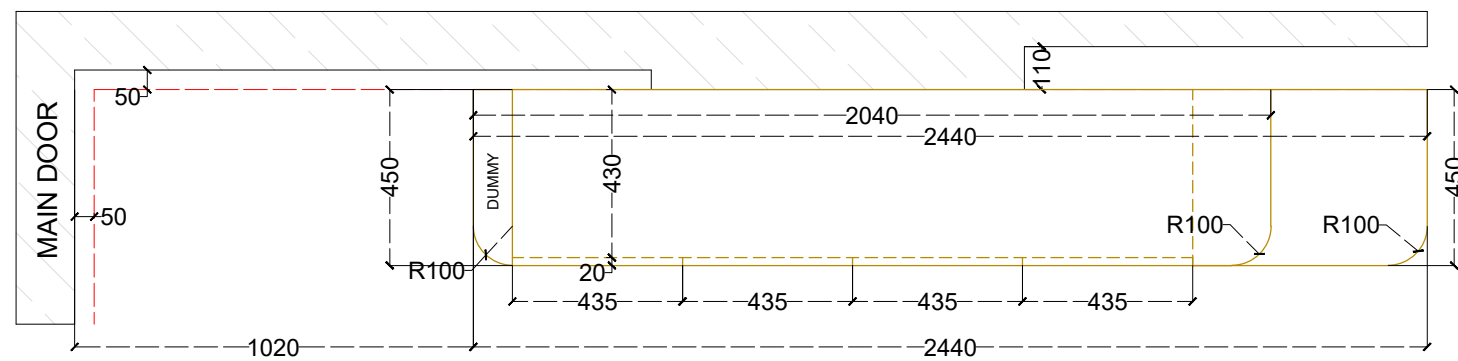
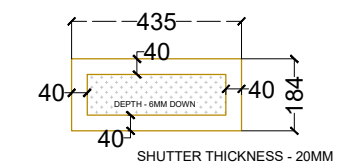
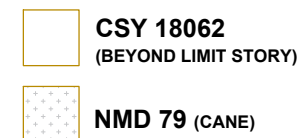


OPEN SHELF DETAIL

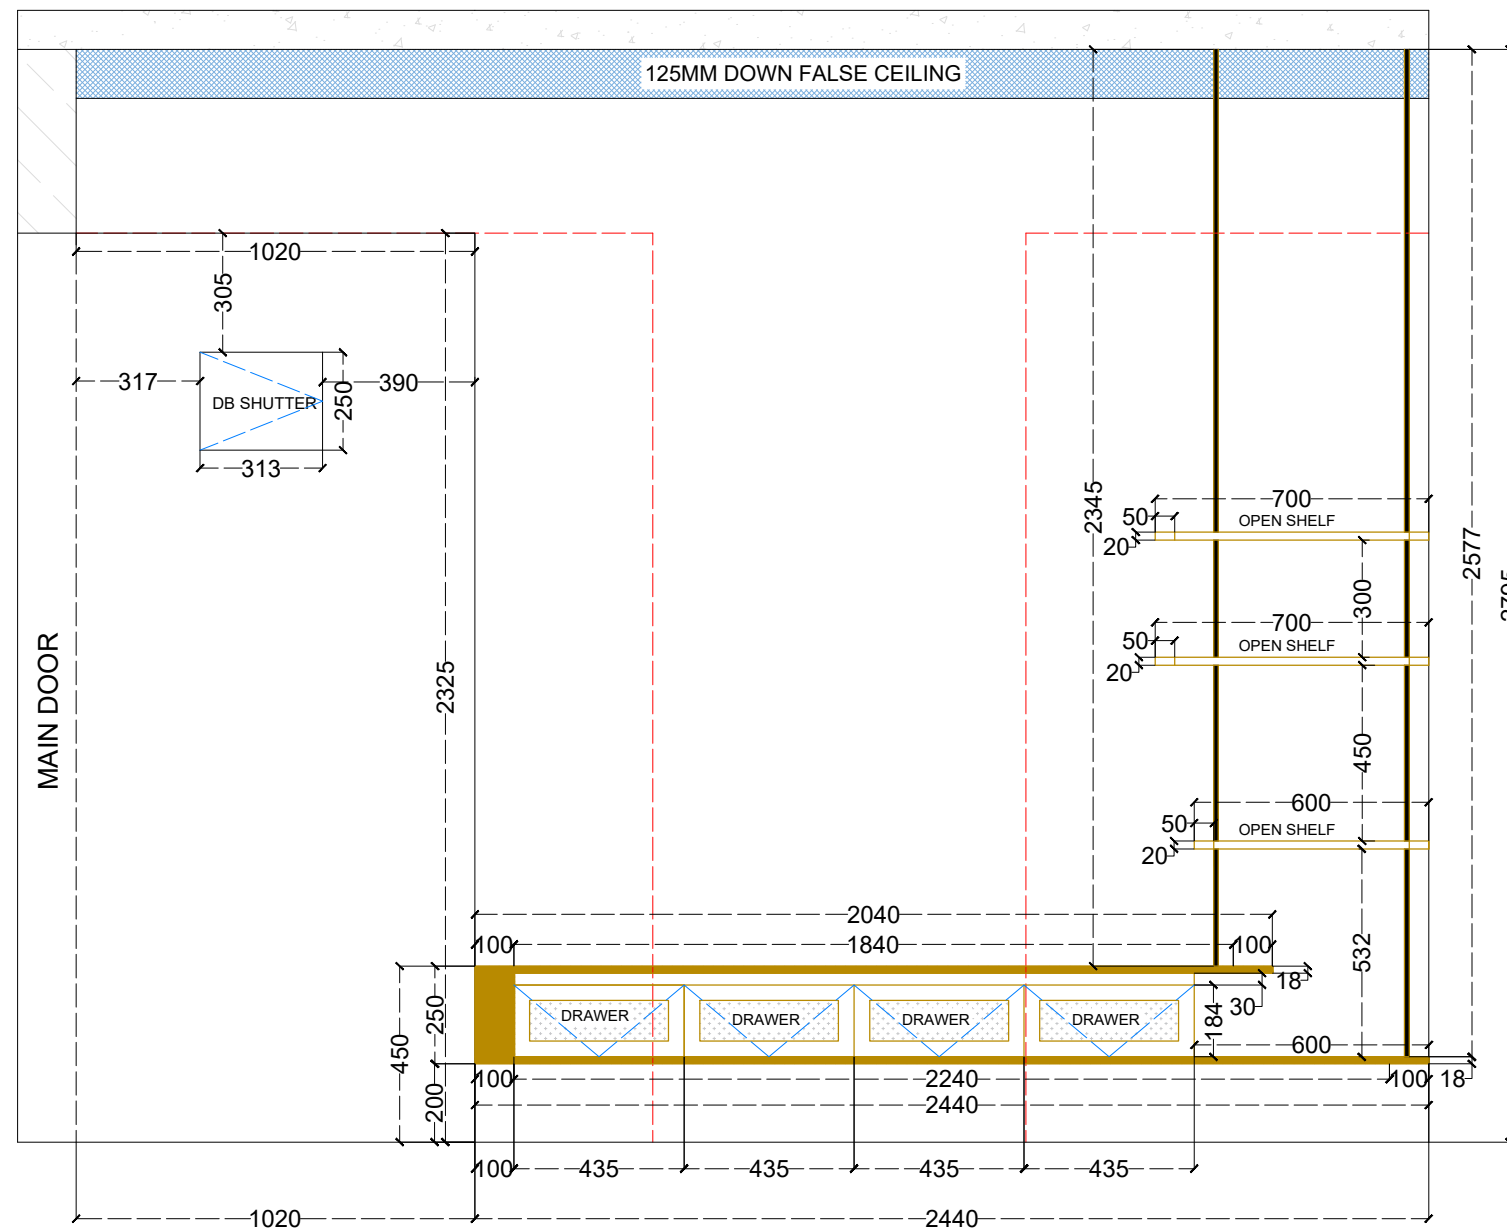

SHUTTER DETAIL (QTY - 4Nos)

TV UNIT - DETAIL SHEET

BASE UNIT

CORE MATERIAL	MR ply
EXPOSED SIDE FINISH	CSY 18062 (BEYOND LIMIT STORY)
SHUTER FASCIA FINISH 1	CSY 18062 (BEYOND LIMIT STORY)
SHUTER FASCIA FINISH 2	NMD 79 (CANE)
INTERNAL FINISH	220 MT/SF (SAFE DECOR)
VISIBLE EDGE BANDING COLOUR	MATCHING WITH LAMINATE

CURVE DUMMY

CORE MATERIAL	MR ply
CURVE DUMMY FINISH	CSY 18062 (BEYOND LIMIT STORY)

HANDLE

DRAWERS	SLANT CUT HANDLE	4Nos
----------------	-------------------------	-------------



CSY 18062 (BEYOND LIMIT STORY)




NMD 79 (CANE)




220 MT/SF (SAFE DECOR)


TITLE : TV UNIT	DISIGNED BY : JITHESH K	PROPOSED INTERIORS FOR : PROJECT : DESIRE TREE CLIENT : Mr AMIT	 LISNO INDIA PRIVATE LIMITED H1/1, 402 Asher Enclave, Naigaon (E) Mumbai, Maharashtra-401208
DATE : 04/05/2026	CHECKED BY :		
PROJECT CODE : M064	HANDOVER DATE :		

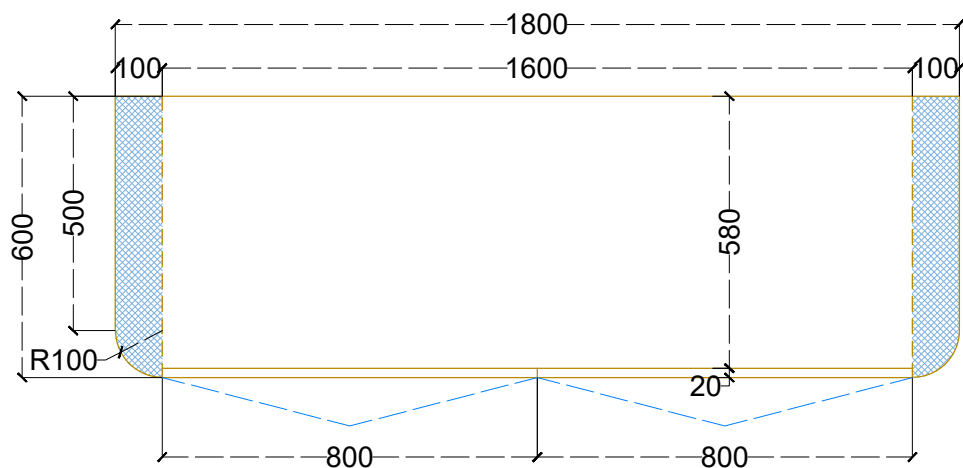


DINING - SEATER WITH STORAGE - PLAN

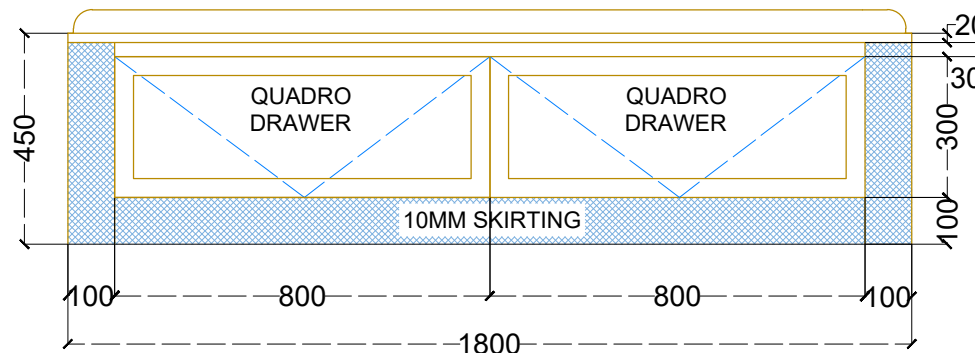

DINING - SEATER WITH STORAGE - ELEVATION

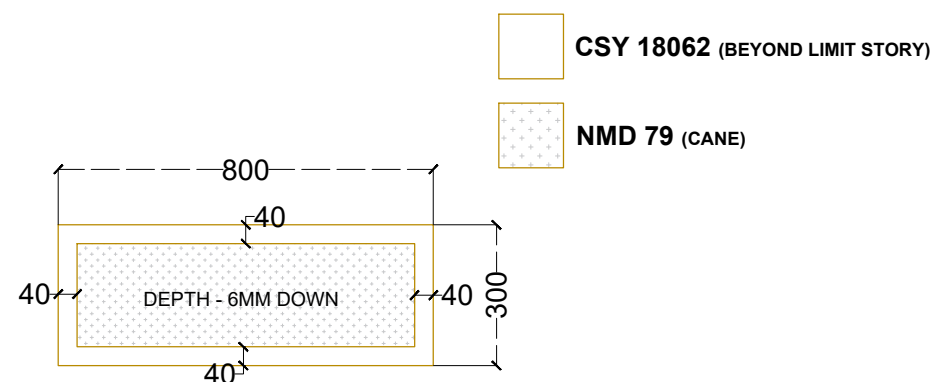

SHUTTER DETAIL (QTY 2Nos)

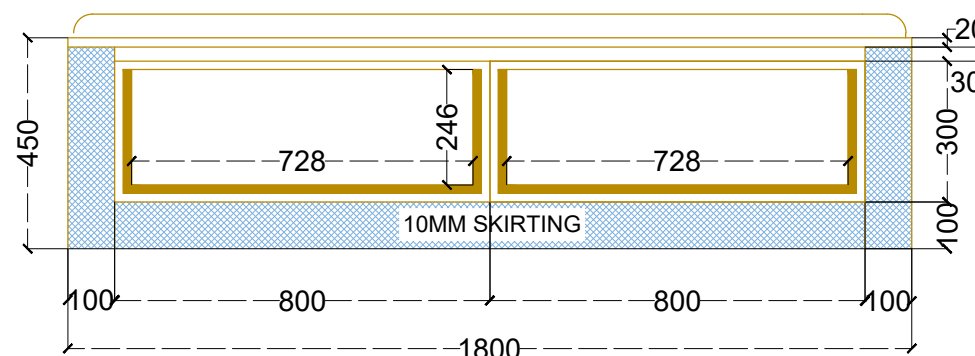

DINING - SEATER WITH STORAGE - INTERNAL

DINING - SEATER UNIT - DETAIL SHEET

BASE UNIT

CORE MATERIAL	MR ply
EXPOSED SIDE FINISH	CSY 18062 (BEYOND LIMIT STORY)
SHUTER FASCIA FINISH 1	CSY 18062 (BEYOND LIMIT STORY)
SHUTER FASCIA FINISH 2	NMD 79 (CANE)
INTERNAL FINISH	220 MT/SF (SAFE DECOR)
VISIBLE EDGE BANDING COLOUR	MATCHING WITH LAMINATE

CURVE DUMMY & SKIRTING

CORE MATERIAL	MR ply
SKIRTING FINISH	CSY 18062 (BEYOND LIMIT STORY)
CURVE DUMMY FINISH	CSY 18062 (BEYOND LIMIT STORY)

HANDLE

BASE DRAWERS	SLANT CUT	2Nos
--------------	-----------	------



CSY 18062 (BEYOND LIMIT STORY)



NMD 79 (CANE)



220 MT/SF (SAFE DECOR)

TITLE : DINING - SEATER UNIT

DISINED BY : JITHESH K

PROPOSED INTERIORS FOR :

DATE : 04/05/2026

CHECKED BY :

PROJECT : DESIRE TREE

PROJECT CODE : M064

HANDOVER DATE :

CLIENT : Mr AMIT



LISNO INDIA PRIVATE LIMITED

H1/1, 402 Asher Enclave, Naigaon (E) Mumbai,
Maharashtra-401208

PUJA UNIT - DETAIL SHEET

BASE UNIT

CORE MATERIAL	MR ply
EXPOSED SIDE FINISH	CSY 18062 (BEYOND LIMIT STORY)
SHUTER FASCIA FINISH 1	CSY 18062 (BEYOND LIMIT STORY)
SHUTER FASCIA FINISH 2	OT 2153 (RESHAM)
INTERNAL FINISH	220 MT/SF (SAFE DECOR)
VISIBLE EDGE BANDING COLOUR	MATCHING WITH LAMINATE

FILLER & SKIRTING

CORE MATERIAL	MR ply
SKIRTING FINISH	CSY 18062 (BEYOND LIMIT STORY)
FILLER FINISH	CSY 18062 (BEYOND LIMIT STORY)

HANDLES

BASE UNIT SHUTTERS	SLANT CUT	3Nos
--------------------	-----------	------




CSY 18062 (BEYOND LIMIT STORY)




OT 2153 (RESHAM)




220 MT/SF (SAFE DECOR)

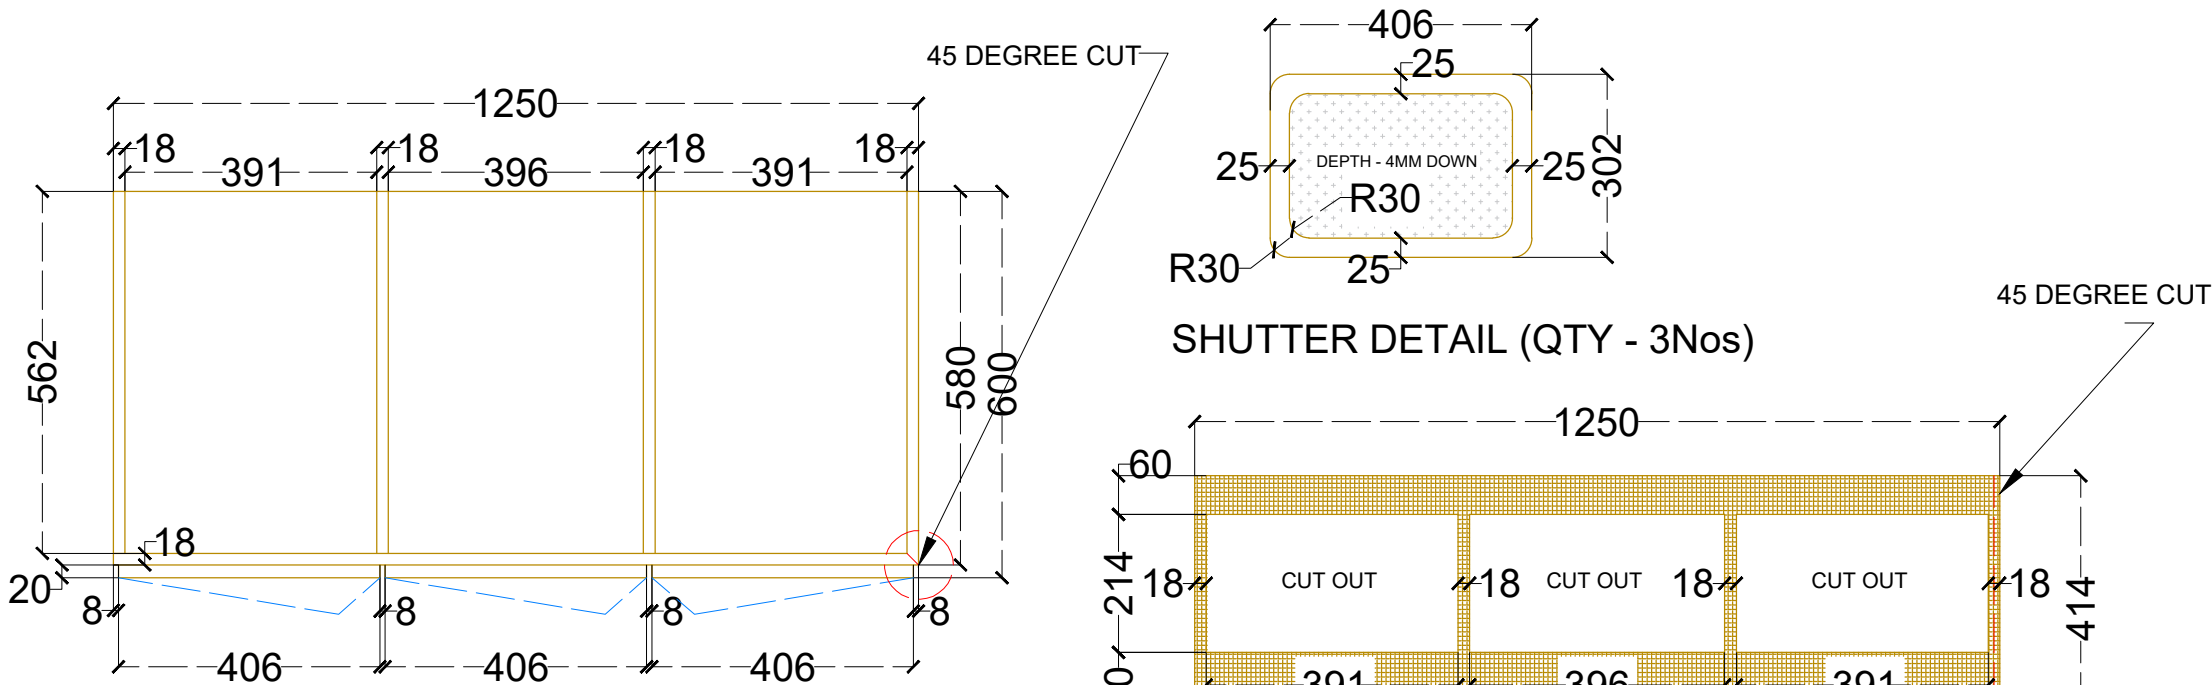


POOJA UNIT - PLAN

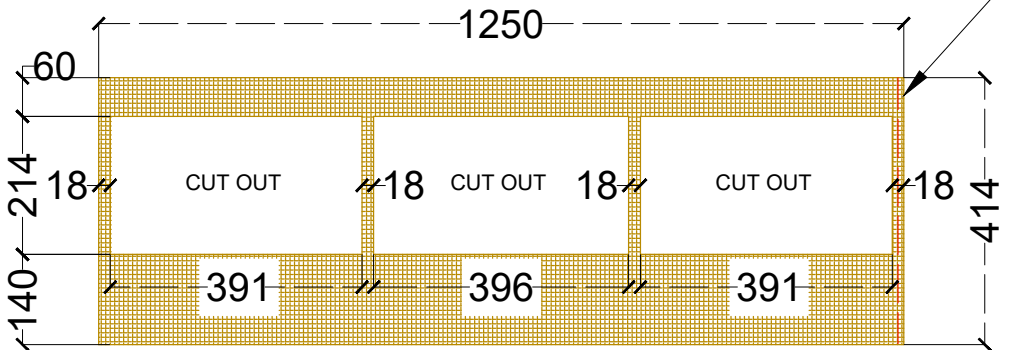

CARCASS FRONT PANEL DETAIL
(18MM)

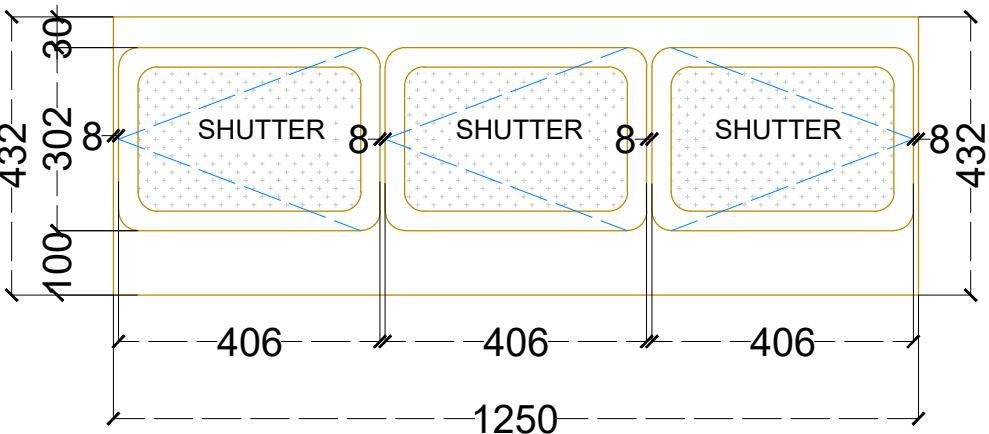

POOJA UNIT - ELEVATION

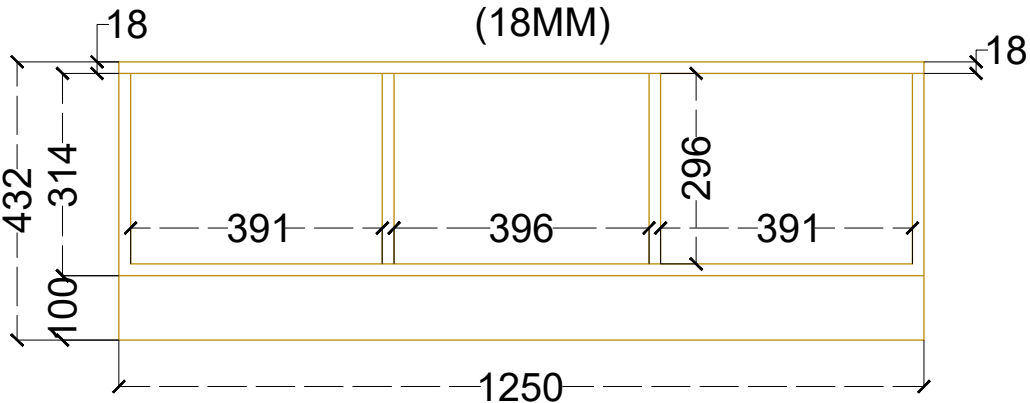

POOJA UNIT - INTERNAL

TITLE : PUJA - UNIT

DATE : 04/05/2026

PROJECT CODE : M064

DISINED BY : JITHESH K

CHECKED BY :

HANDOVER DATE :


PROPOSED INTERIORS FOR :

PROJECT : DESIRE TREE

CLIENT : Mr AMIT



LISNO INDIA PRIVATE LIMITED
H1/1, 402 Asher Enclave, Naigaon (E) Mumbai,
Maharashtra-401208

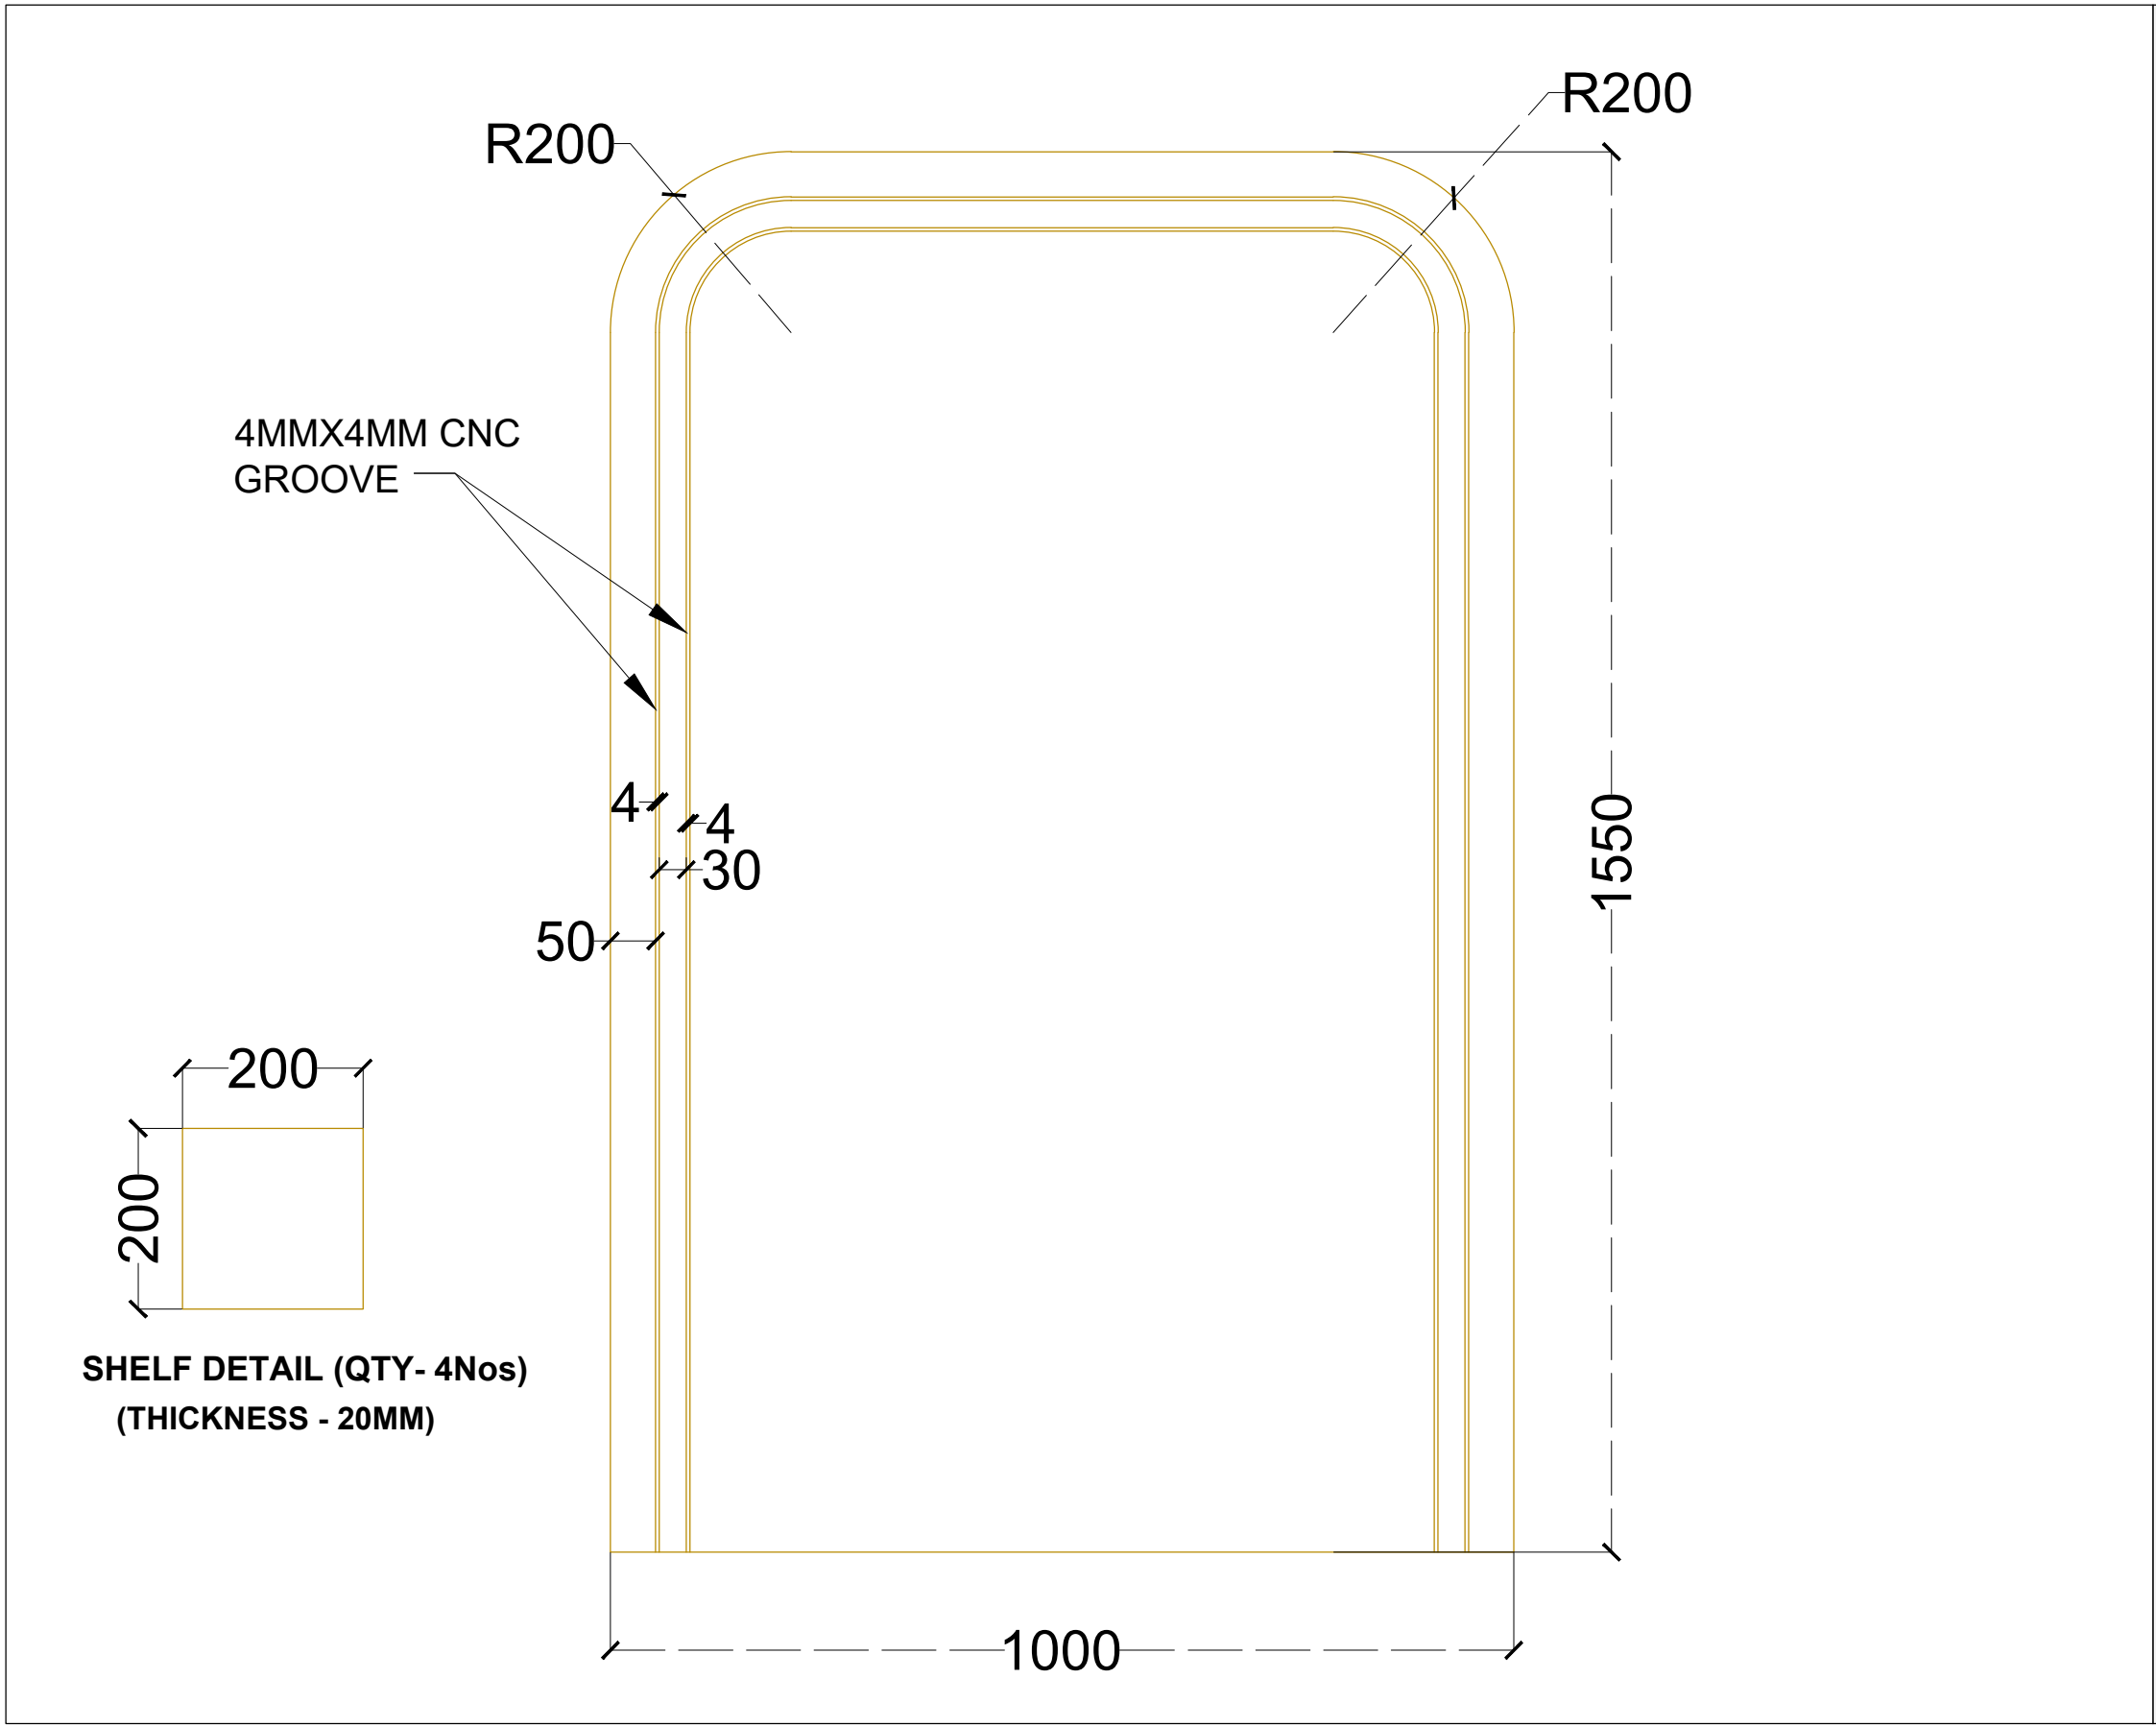


PUJA BACK PANEL - DETAIL SHEET

DRAWER BASE UNIT

CORE MATERIAL	MR ply
EXPOSED SIDE FINISH	CSY 18062 (BEYOND LIMIT STORY)
VISIBLE EDGE BANDING COLOUR	MATCHING WITH LAMINATE

CSY 18062 (BEYOND LIMIT STORY)

TITLE : PUJA BACK PANEL	DISINED BY : JITHESH K	PRAPOSED INTERIORS FOR : PROJECT : DESIRE TREE CLIENT : Mr AMIT	 LISNO INDIA PRIVATE LIMITED H1/1, 402 Asher Enclave, Naigaon (E) Mumbai, Maharashtra-401208
DATE : 04/05/2026	CHECKED BY :		
PROJECT CODE : M064	HANDOVER DATE :		

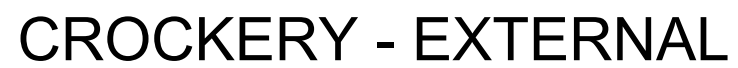

TALL UNIT

SKIRTING

HANDLE

CSY 18062 (BEYOND LIMIT STORY)


**BLACK TINTED FLUTED GLASS
(TOUGHENED)**

220 MT/SF (SAFE DECOR)

CLIENT : Mr AMIT



LISNO INDIA PRIVATE LIMITED
H1/1, 402 Asher Enclave, Naigaon (E) Mumbai,
Maharashtra-401208

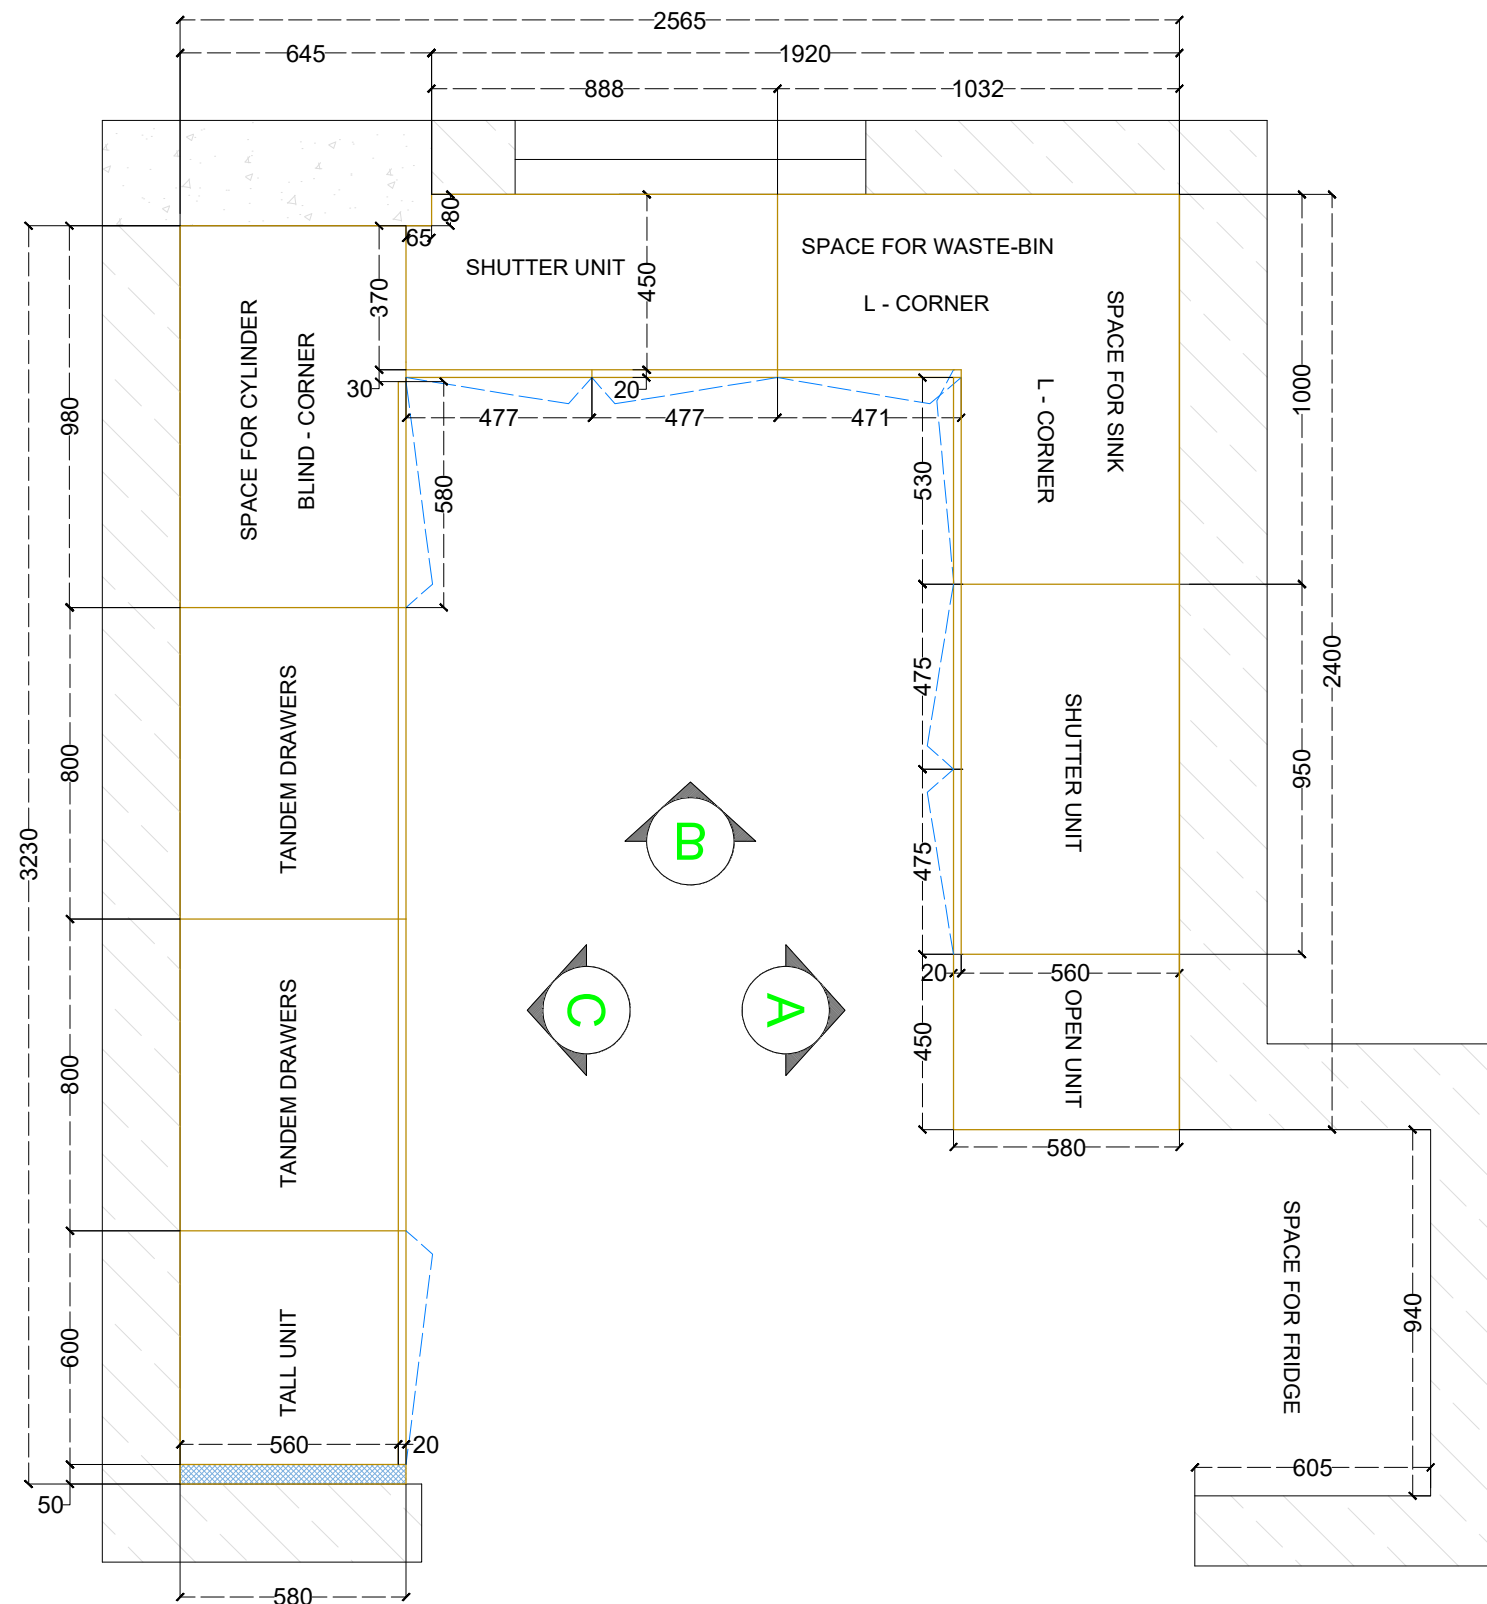


KITCHEN - BASE UNIT PLAN

KITCHEN - DETAIL SHEET




KITCHEN - SHUTTER FIXING DETAIL

BEADING DETAILS (BEADING THICKNESS - 5MM)

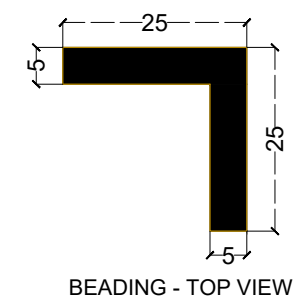

BEADING - TOP VIEW

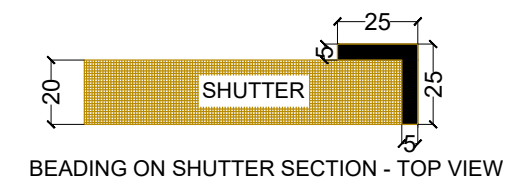

BEADING ON SHUTTER SECTION - TOP VIEW

TITLE : KITCHEN

DATE : 04/05/2026

PROJECT CODE : M064

DISIGNED BY : JITHESH K

CHECKED BY :

HANDOVER DATE :

PROPOSED INTERIORS FOR :


PROJECT : DESIRE TREE

CLIENT : Mr AMIT




LISNO INDIA PRIVATE LIMITED
H1/1, 402 Asher Enclave, Naigaon (E) Mumbai,
Maharashtra-401208

KITCHEN - DETAIL SHEET

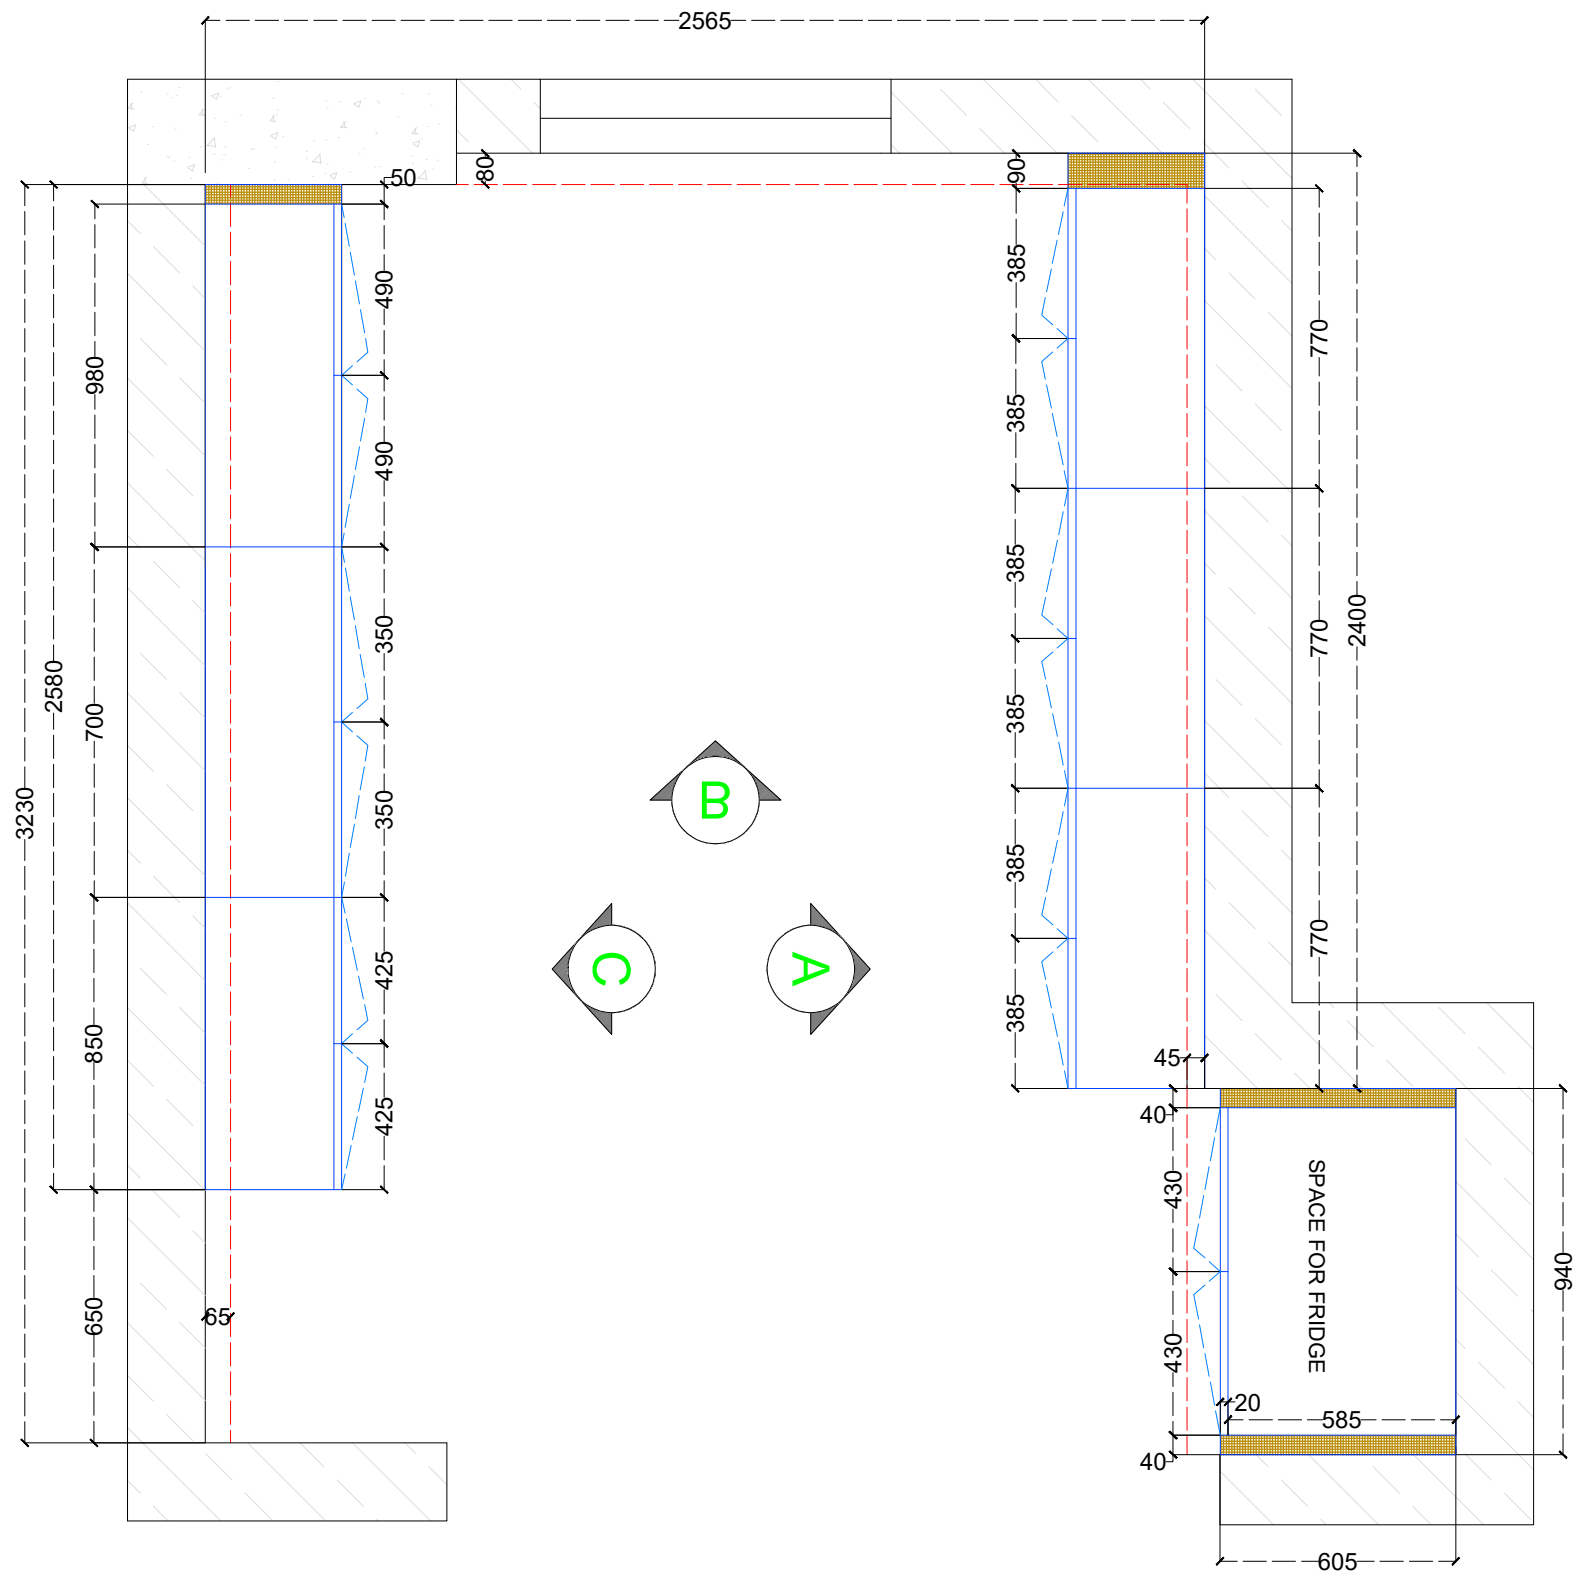

KITCHEN - WALL UNIT PLAN

TITLE : KITCHEN	DISINED BY : JITHESH K	PROPOSED INTERIORS FOR : PROJECT : DESIRE TREE CLIENT : Mr AMIT	LISNO INDIA PRIVATE LIMITED H1/1, 402 Asher Enclave, Naigaon (E) Mumbai, Maharashtra-401208
DATE : 04/05/2026	CHECKED BY :		
PROJECT CODE : M064	HANDOVER DATE :		

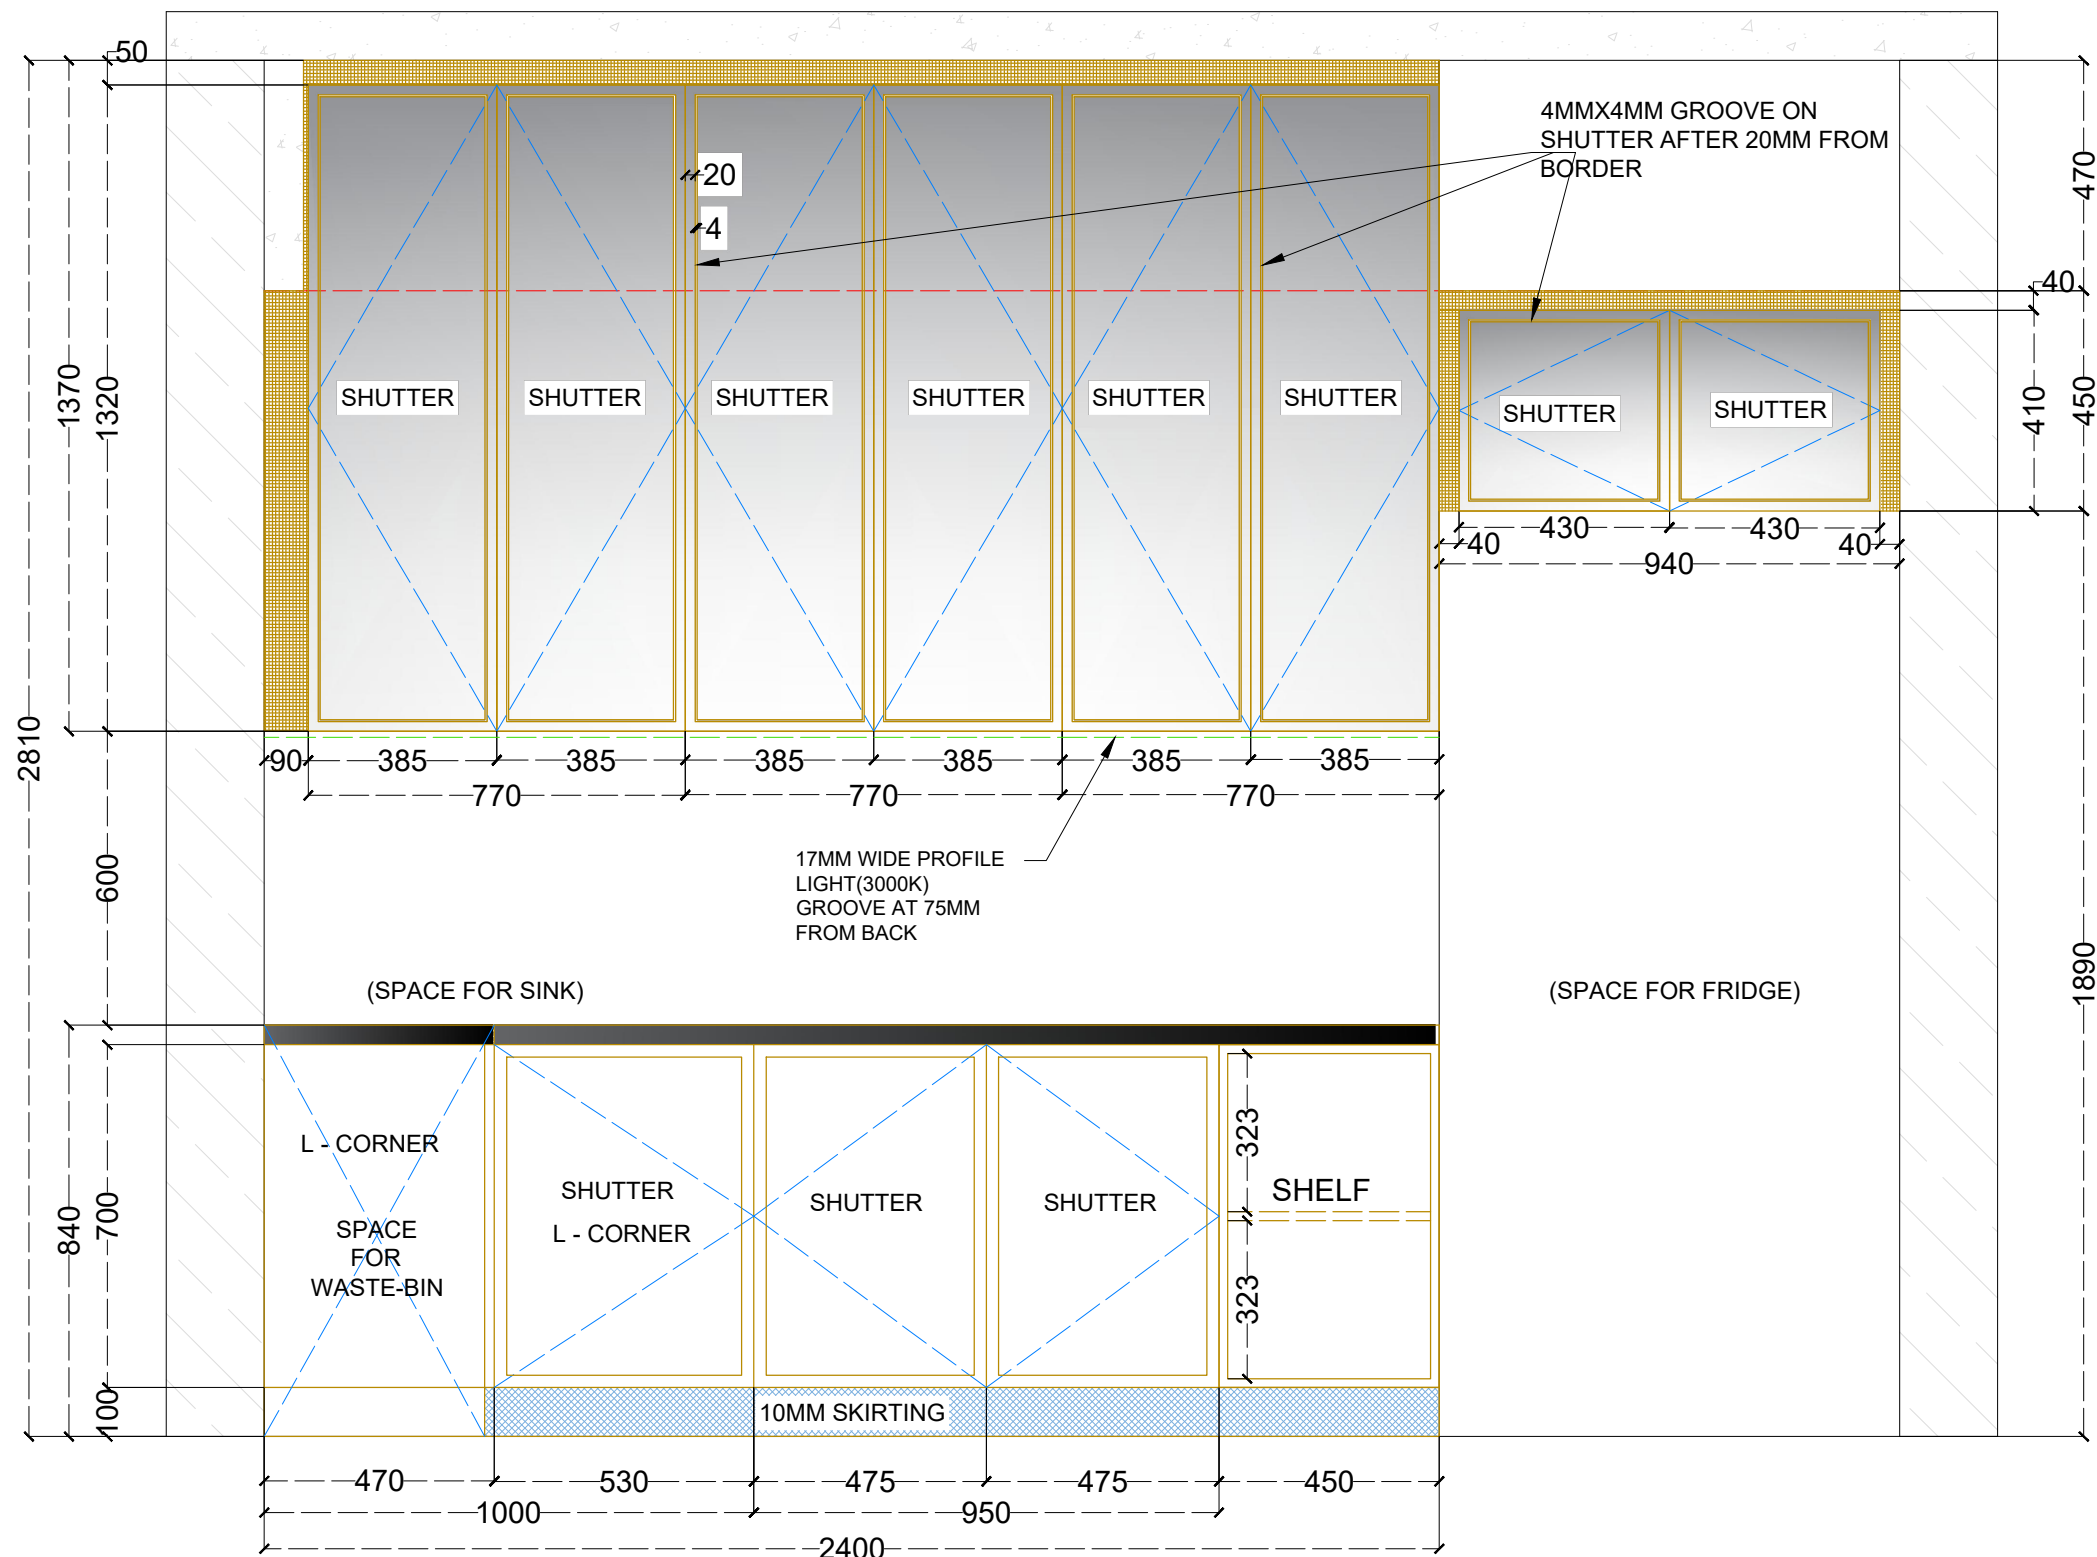

KITCHEN - ELEVATION A

KITCHEN - DETAIL SHEET

BASE UNIT & TALL UNIT

CORE MATERIAL	BWP ply
EXPOSED SIDE FINISH	CSY 18062 (BEYOND LIMIT STORY)
SHUTER FASCIA FINISH	CSY 18062 (BEYOND LIMIT STORY)
DRAWER FASCIA FINISH	CSY 18062 (BEYOND LIMIT STORY)
INTERNAL FINISH	220 MT/SF (SAFE DECOR)
VISIBLE EDGE BANDING COLOUR	MATCHING WITH LAMINATE

FILLER & SKIRTING

CORE MATERIAL	MR ply
SKIRTING FINISH	CSY 18062 (BEYOND LIMIT STORY)
FILLER FINISH	CSY 18062 (BEYOND LIMIT STORY)

WALL UNIT

CORE MATERIAL	MR ply
EXPOSED SIDE FINISH	1108 (SDW)
SHUTER FASCIA FINISH	1108 (SDW)
GLASS SHUTTER - GLASS	BLACK TINTED FLUTED
GLASS SHUTTER - PROFILE	BLACK
INTERNAL FINISH	238 MT/SF (SAFE DECOR)
VISIBLE EDGE BANDING COLOUR	MATCHING WITH LAMINATE

FILLER

CORE MATERIAL	MR ply
FILLER FINISH	1108 (SDW)

HANDLE

TALL UNIT SHUTTER	KNOB	3Nos
BASE UNIT SHUTTER	KNOB	7Nos
BASE UNIT DRAWER	KNOB	5Nos
WALL UNIT SHUTTER	KNOB	10Nos
GLASS SHUTTER	BLACK BINDI PROFILE	4Nos

TITLE : DINING - SEATER UNIT

DISINED BY : JITHESH K

PROPOSED INTERIORS FOR :

DATE : 04/05/2026

CHECKED BY :

PROJECT : DESIRE TREE


PROJECT CODE : M064

HANDOVER DATE :

CLIENT : Mr AMIT




LISNO INDIA PRIVATE LIMITED
H1/1, 402 Asher Enclave, Naigaon (E) Mumbai,
Maharashtra-401208

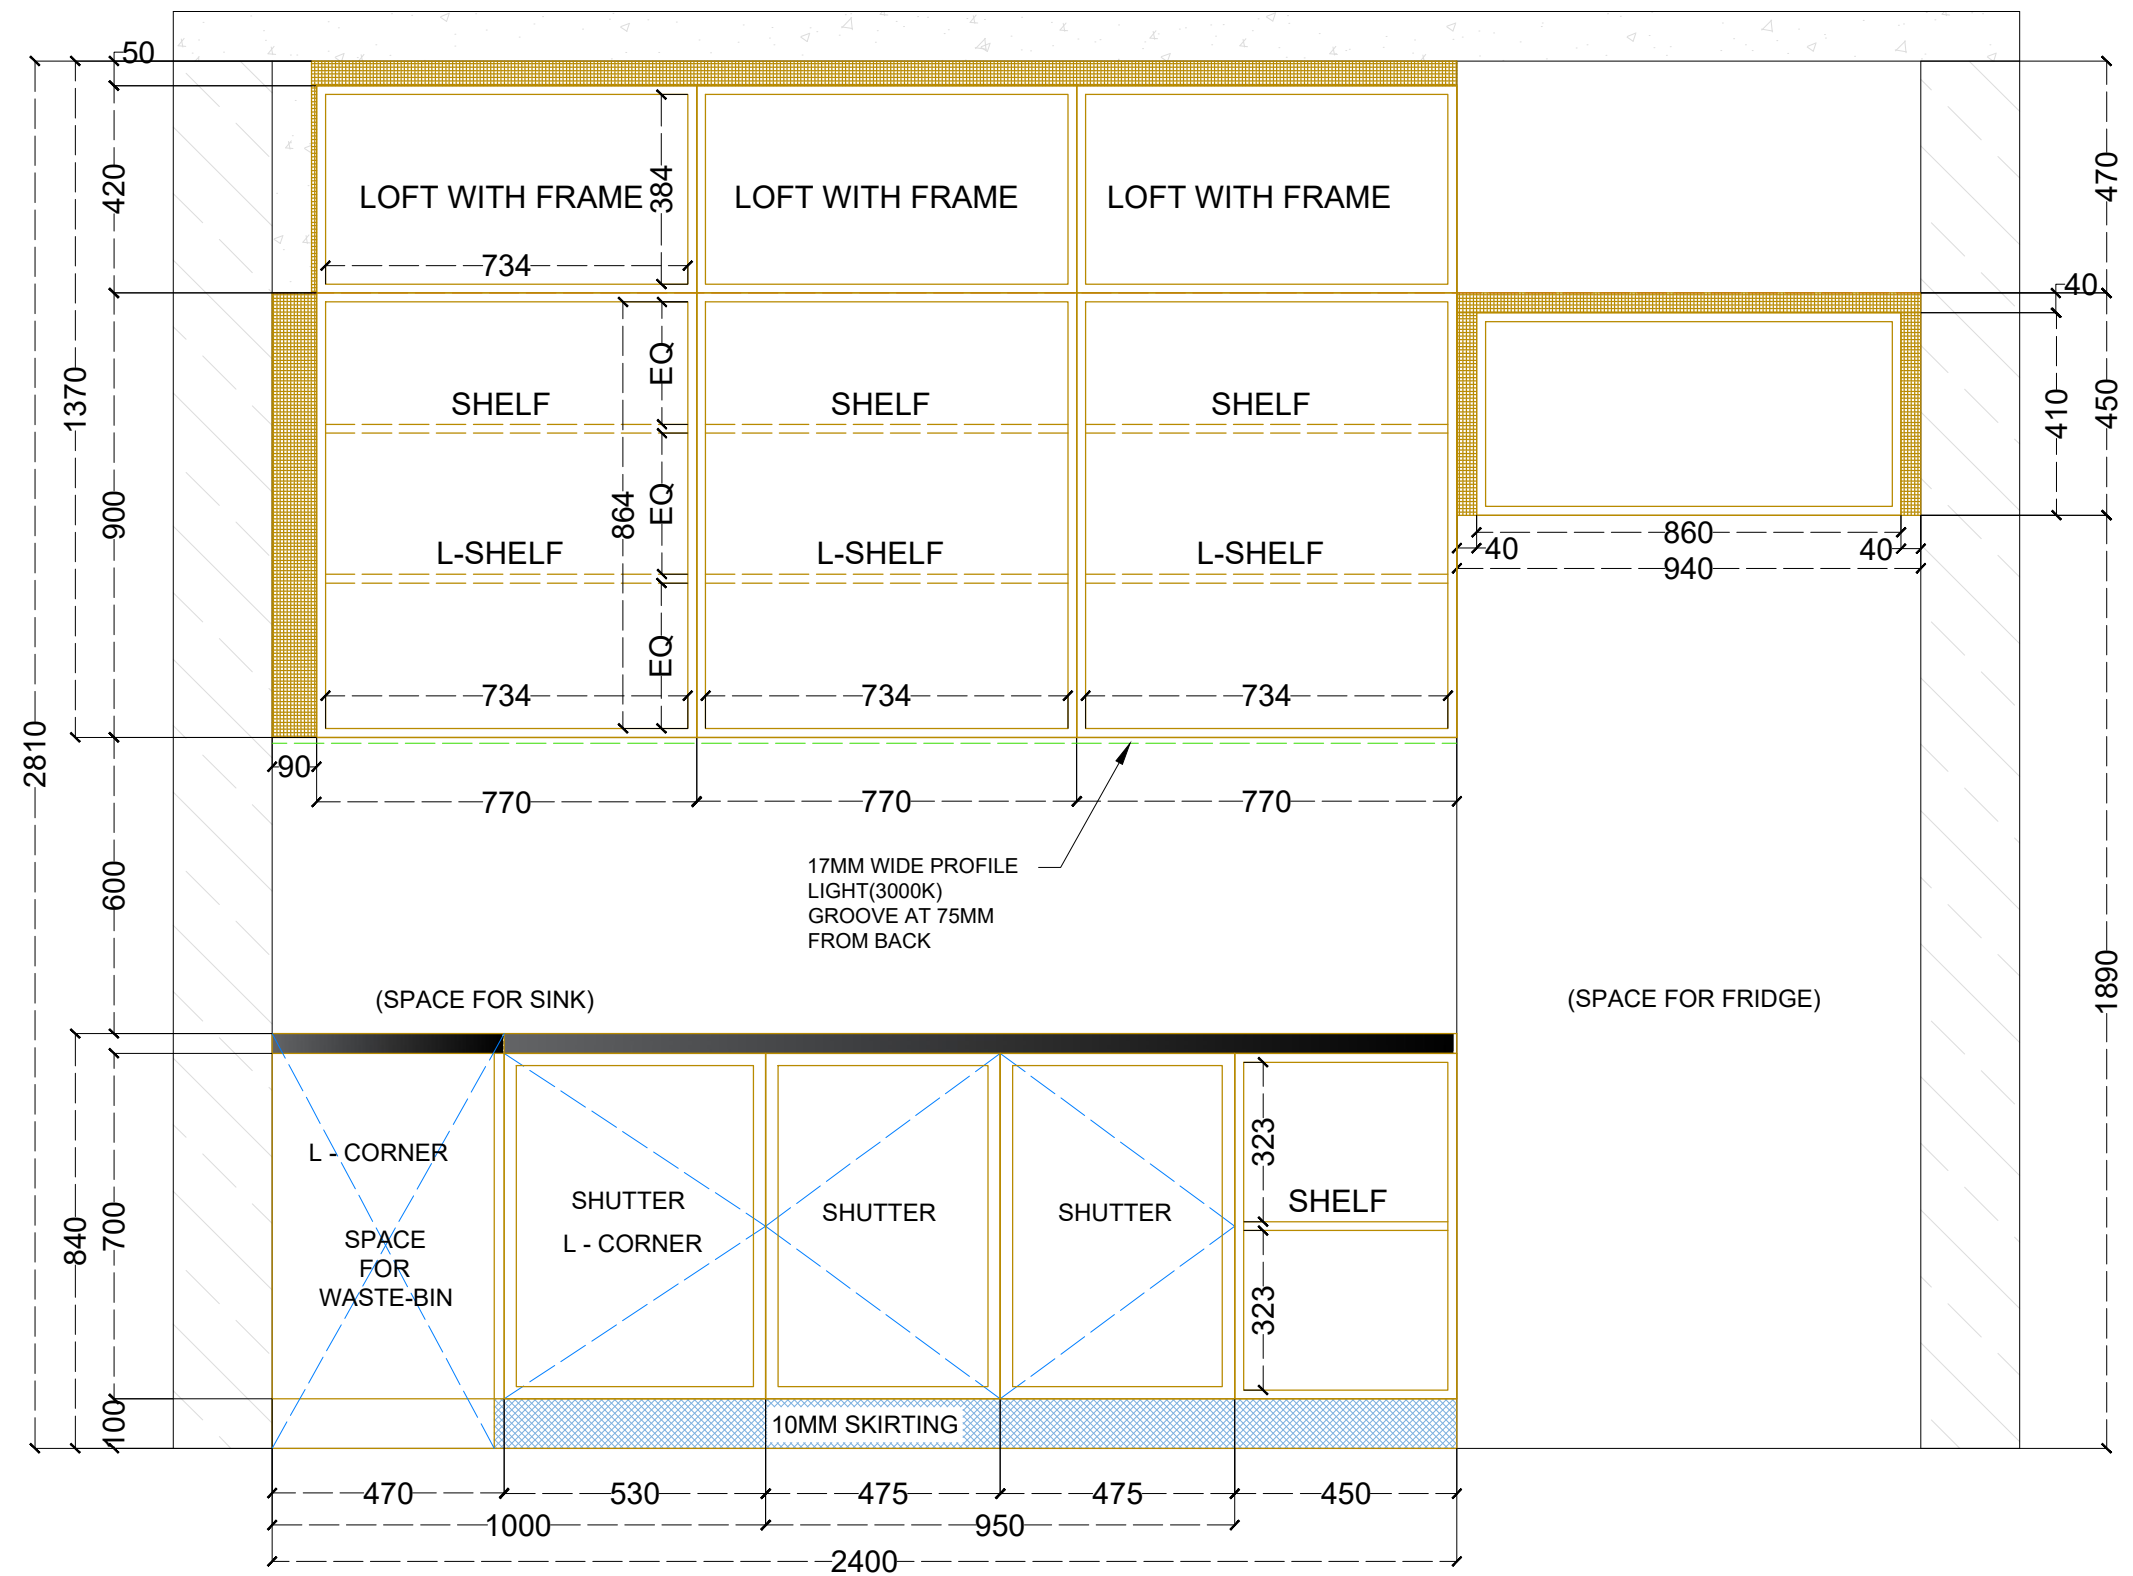

KITCHEN - ELEVATION A INTERNALS


TITLE : KITCHEN	DISINED BY : JITHESH K	PROPOSED INTERIORS FOR : PROJECT : DESIRE TREE CLIENT : Mr AMIT	 LISNO INDIA PRIVATE LIMITED H1/1, 402 Asher Enclave, Naigaon (E) Mumbai, Maharashtra-401208
DATE : 04/05/2026	CHECKED BY :		
PROJECT CODE : M064	HANDOVER DATE :		

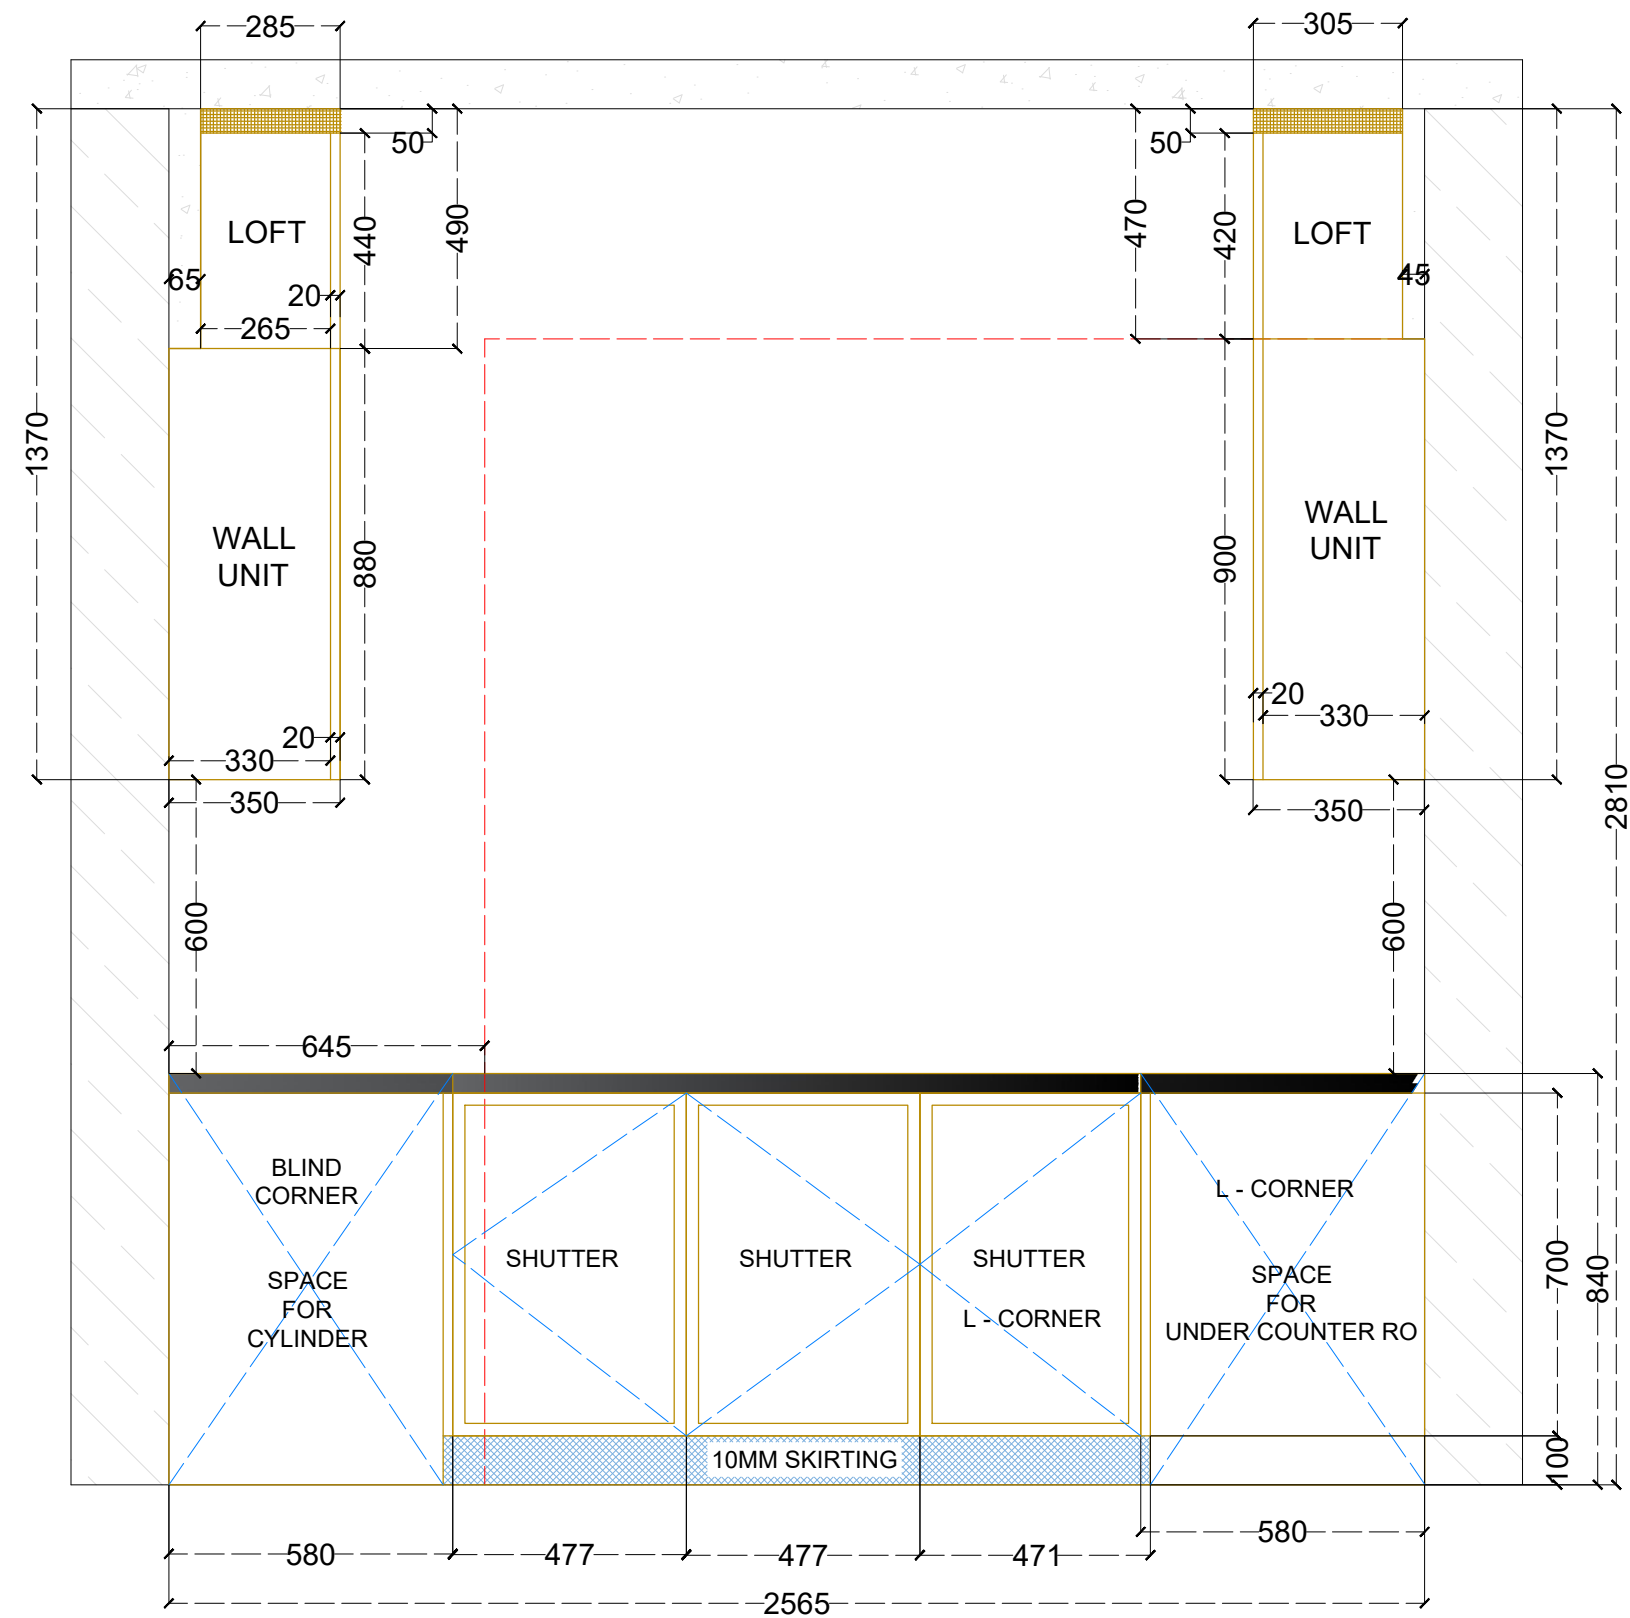

KITCHEN - ELEVATION B

KITCHEN - DETAIL SHEET


TITLE : DINING - SEATER UNIT	DISINED BY : JITHESH K	PROPOSED INTERIORS FOR : PROJECT : DESIRE TREE CLIENT : Mr AMIT	 LISNO INDIA PRIVATE LIMITED H1/1, 402 Asher Enclave, Naigaon (E) Mumbai, Maharashtra-401208
DATE : 04/05/2026	CHECKED BY :		
PROJECT CODE : M064	HANDOVER DATE :		

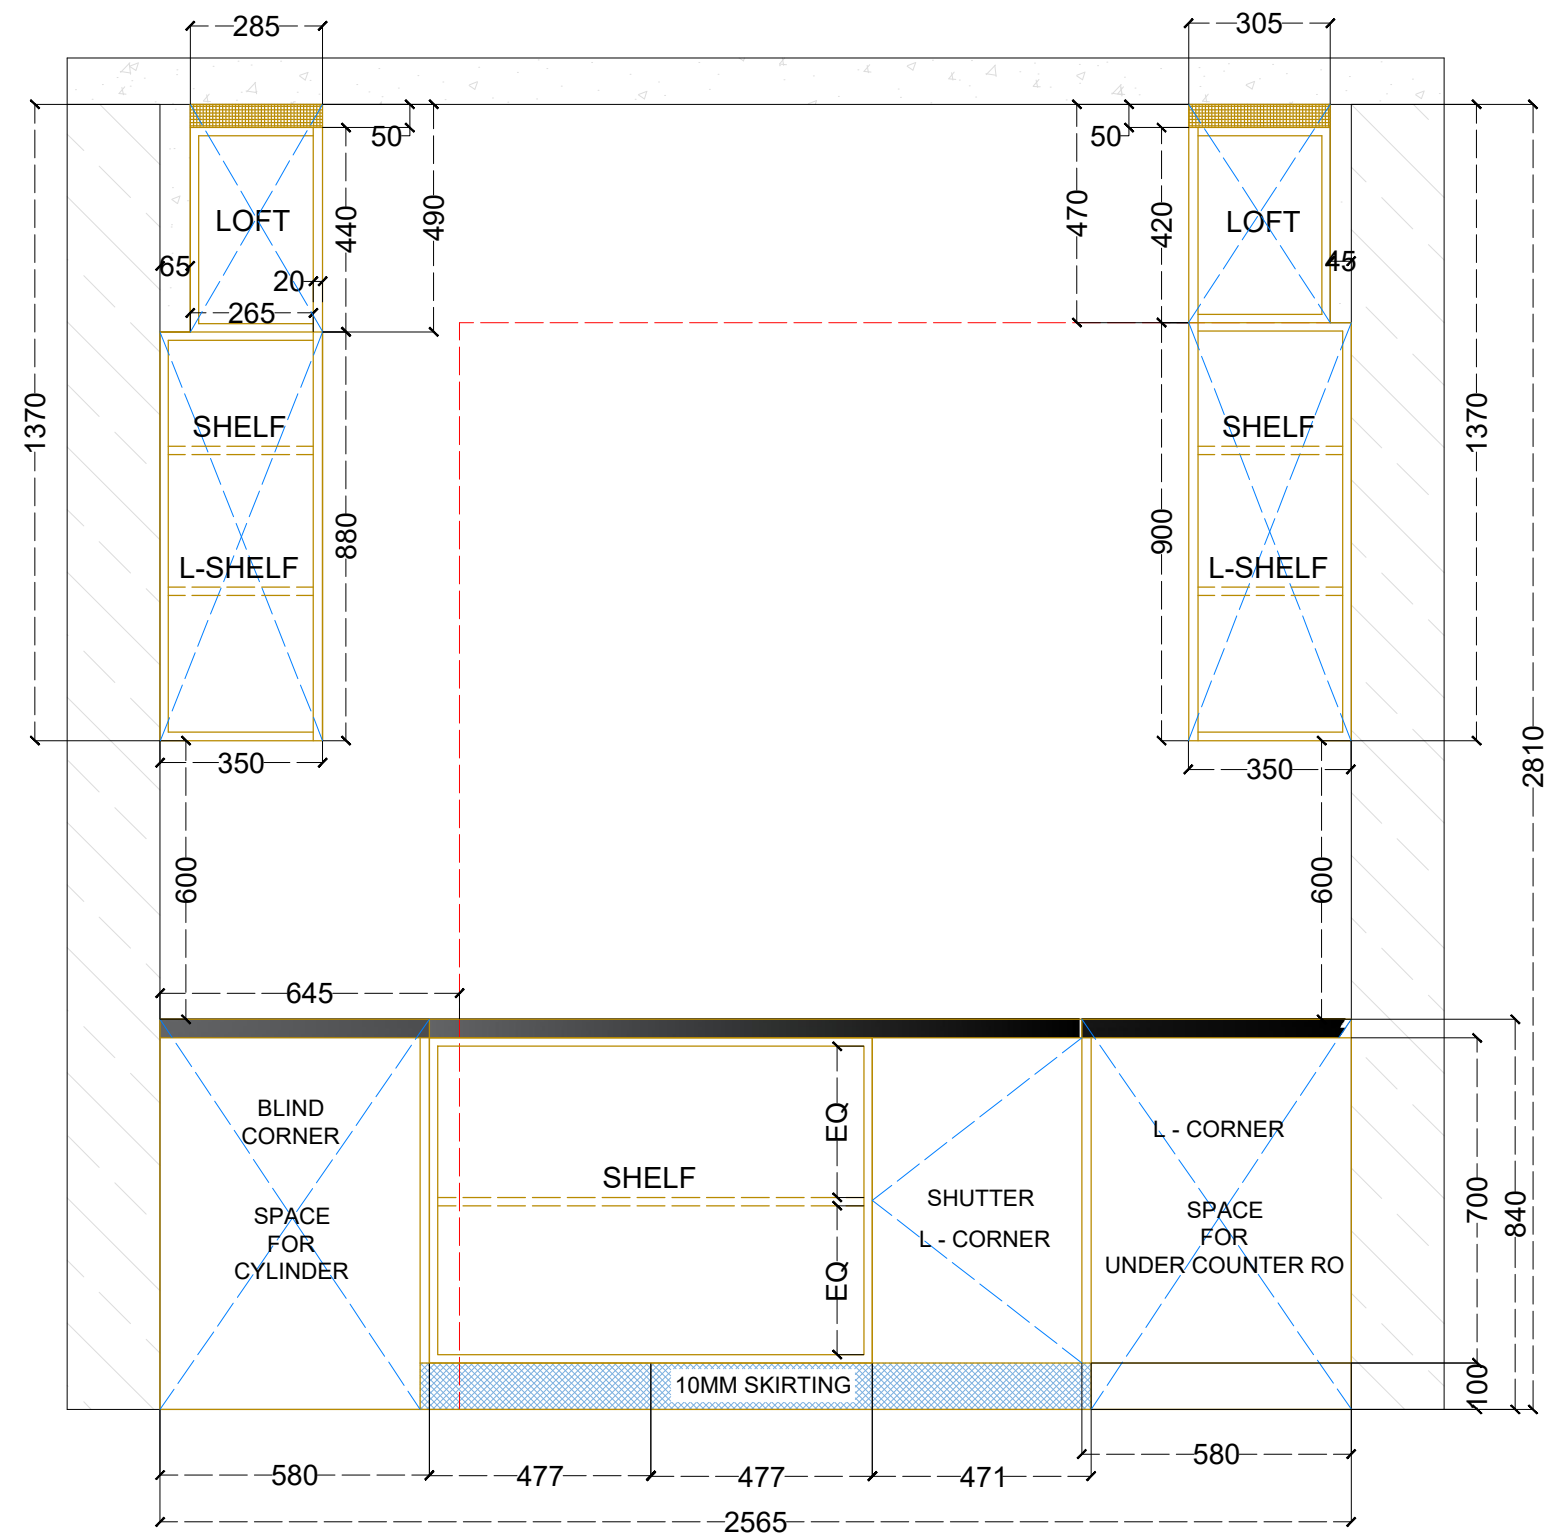

KITCHEN - ELEVATION B INTERNAL

TITLE : KITCHEN	DISINED BY : JITHESH K	PROPOSED INTERIORS FOR : PROJECT : DESIRE TREE CLIENT : Mr AMIT	 LISNO INDIA PRIVATE LIMITED H1/1, 402 Asher Enclave, Naigaon (E) Mumbai, Maharashtra-401208
DATE : 04/05/2026	CHECKED BY :		
PROJECT CODE : M064	HANDOVER DATE :		


KITCHEN - DETAIL SHEET

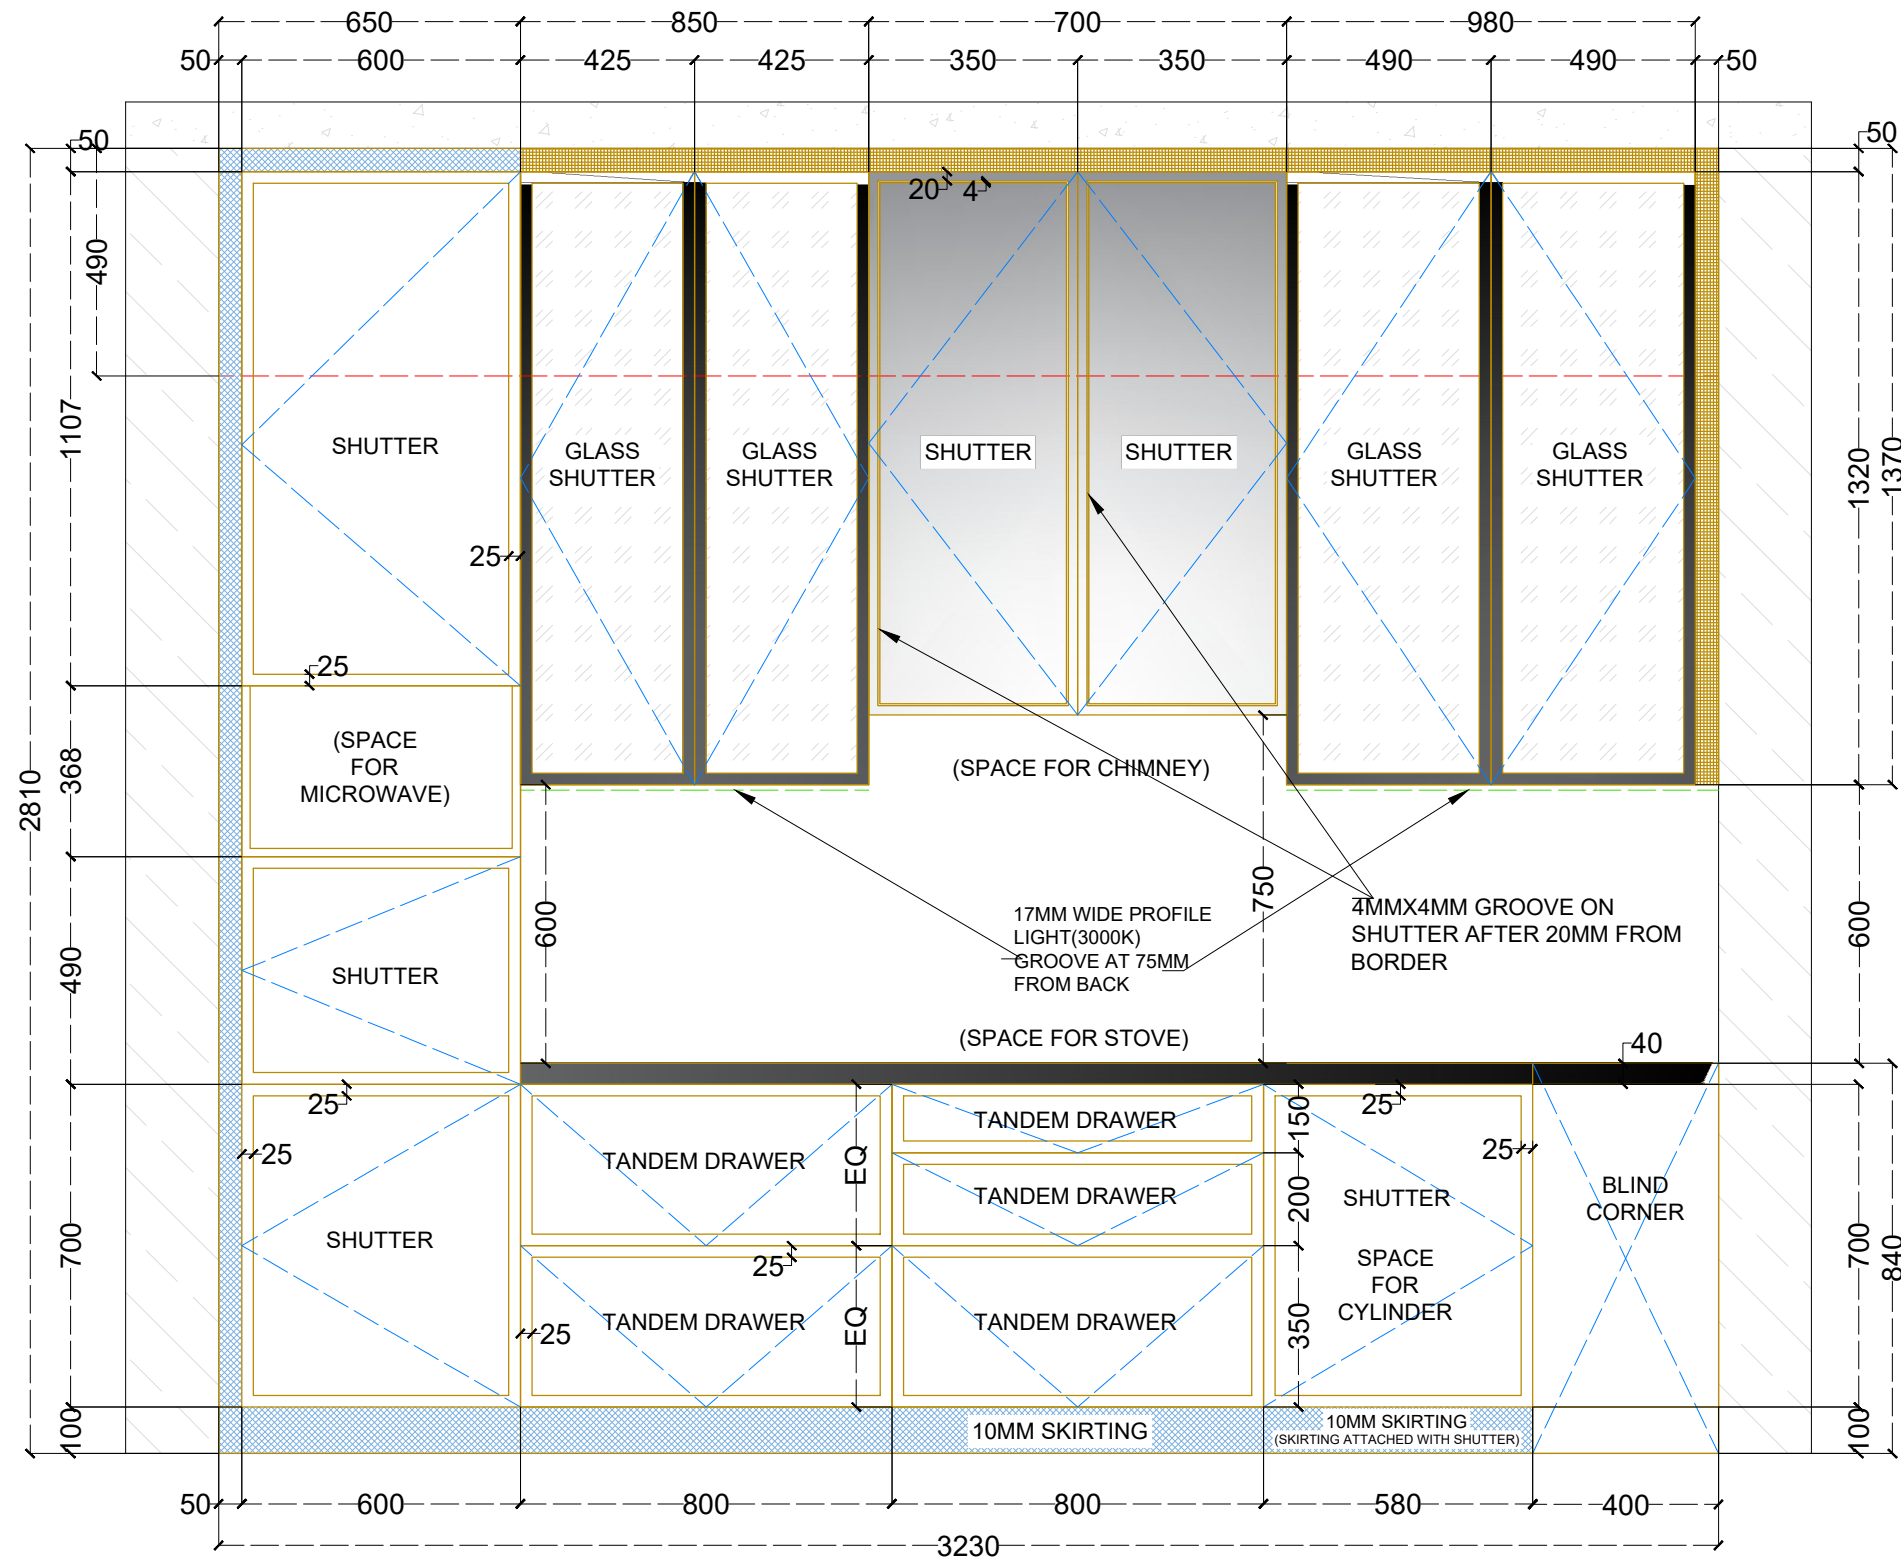

KITCHEN - ELEVATION C




1108 (SDW)

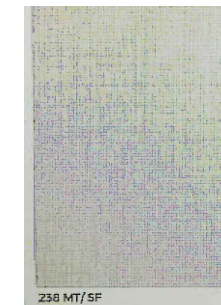

238 MT/SF (SAFE DECOR)



220 MT/SF (SAFE DECOR)

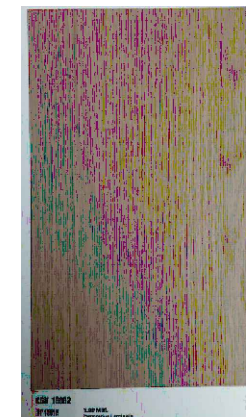

CSY 18062 (BEYOND LIMIT STORY)



BLACK TINTED FLUTED GLASS

TITLE : KITCHEN

DATE : 04/05/2026

PROJECT CODE : M064

DISIGNED BY : JITHESH K

CHECKED BY :

HANDOVER DATE :


PROPOSED INTERIORS FOR :

PROJECT : DESIRE TREE

CLIENT : Mr AMIT




LISNO INDIA PRIVATE LIMITED
H1/1, 402 Asher Enclave, Naigaon (E) Mumbai,
Maharashtra-401208

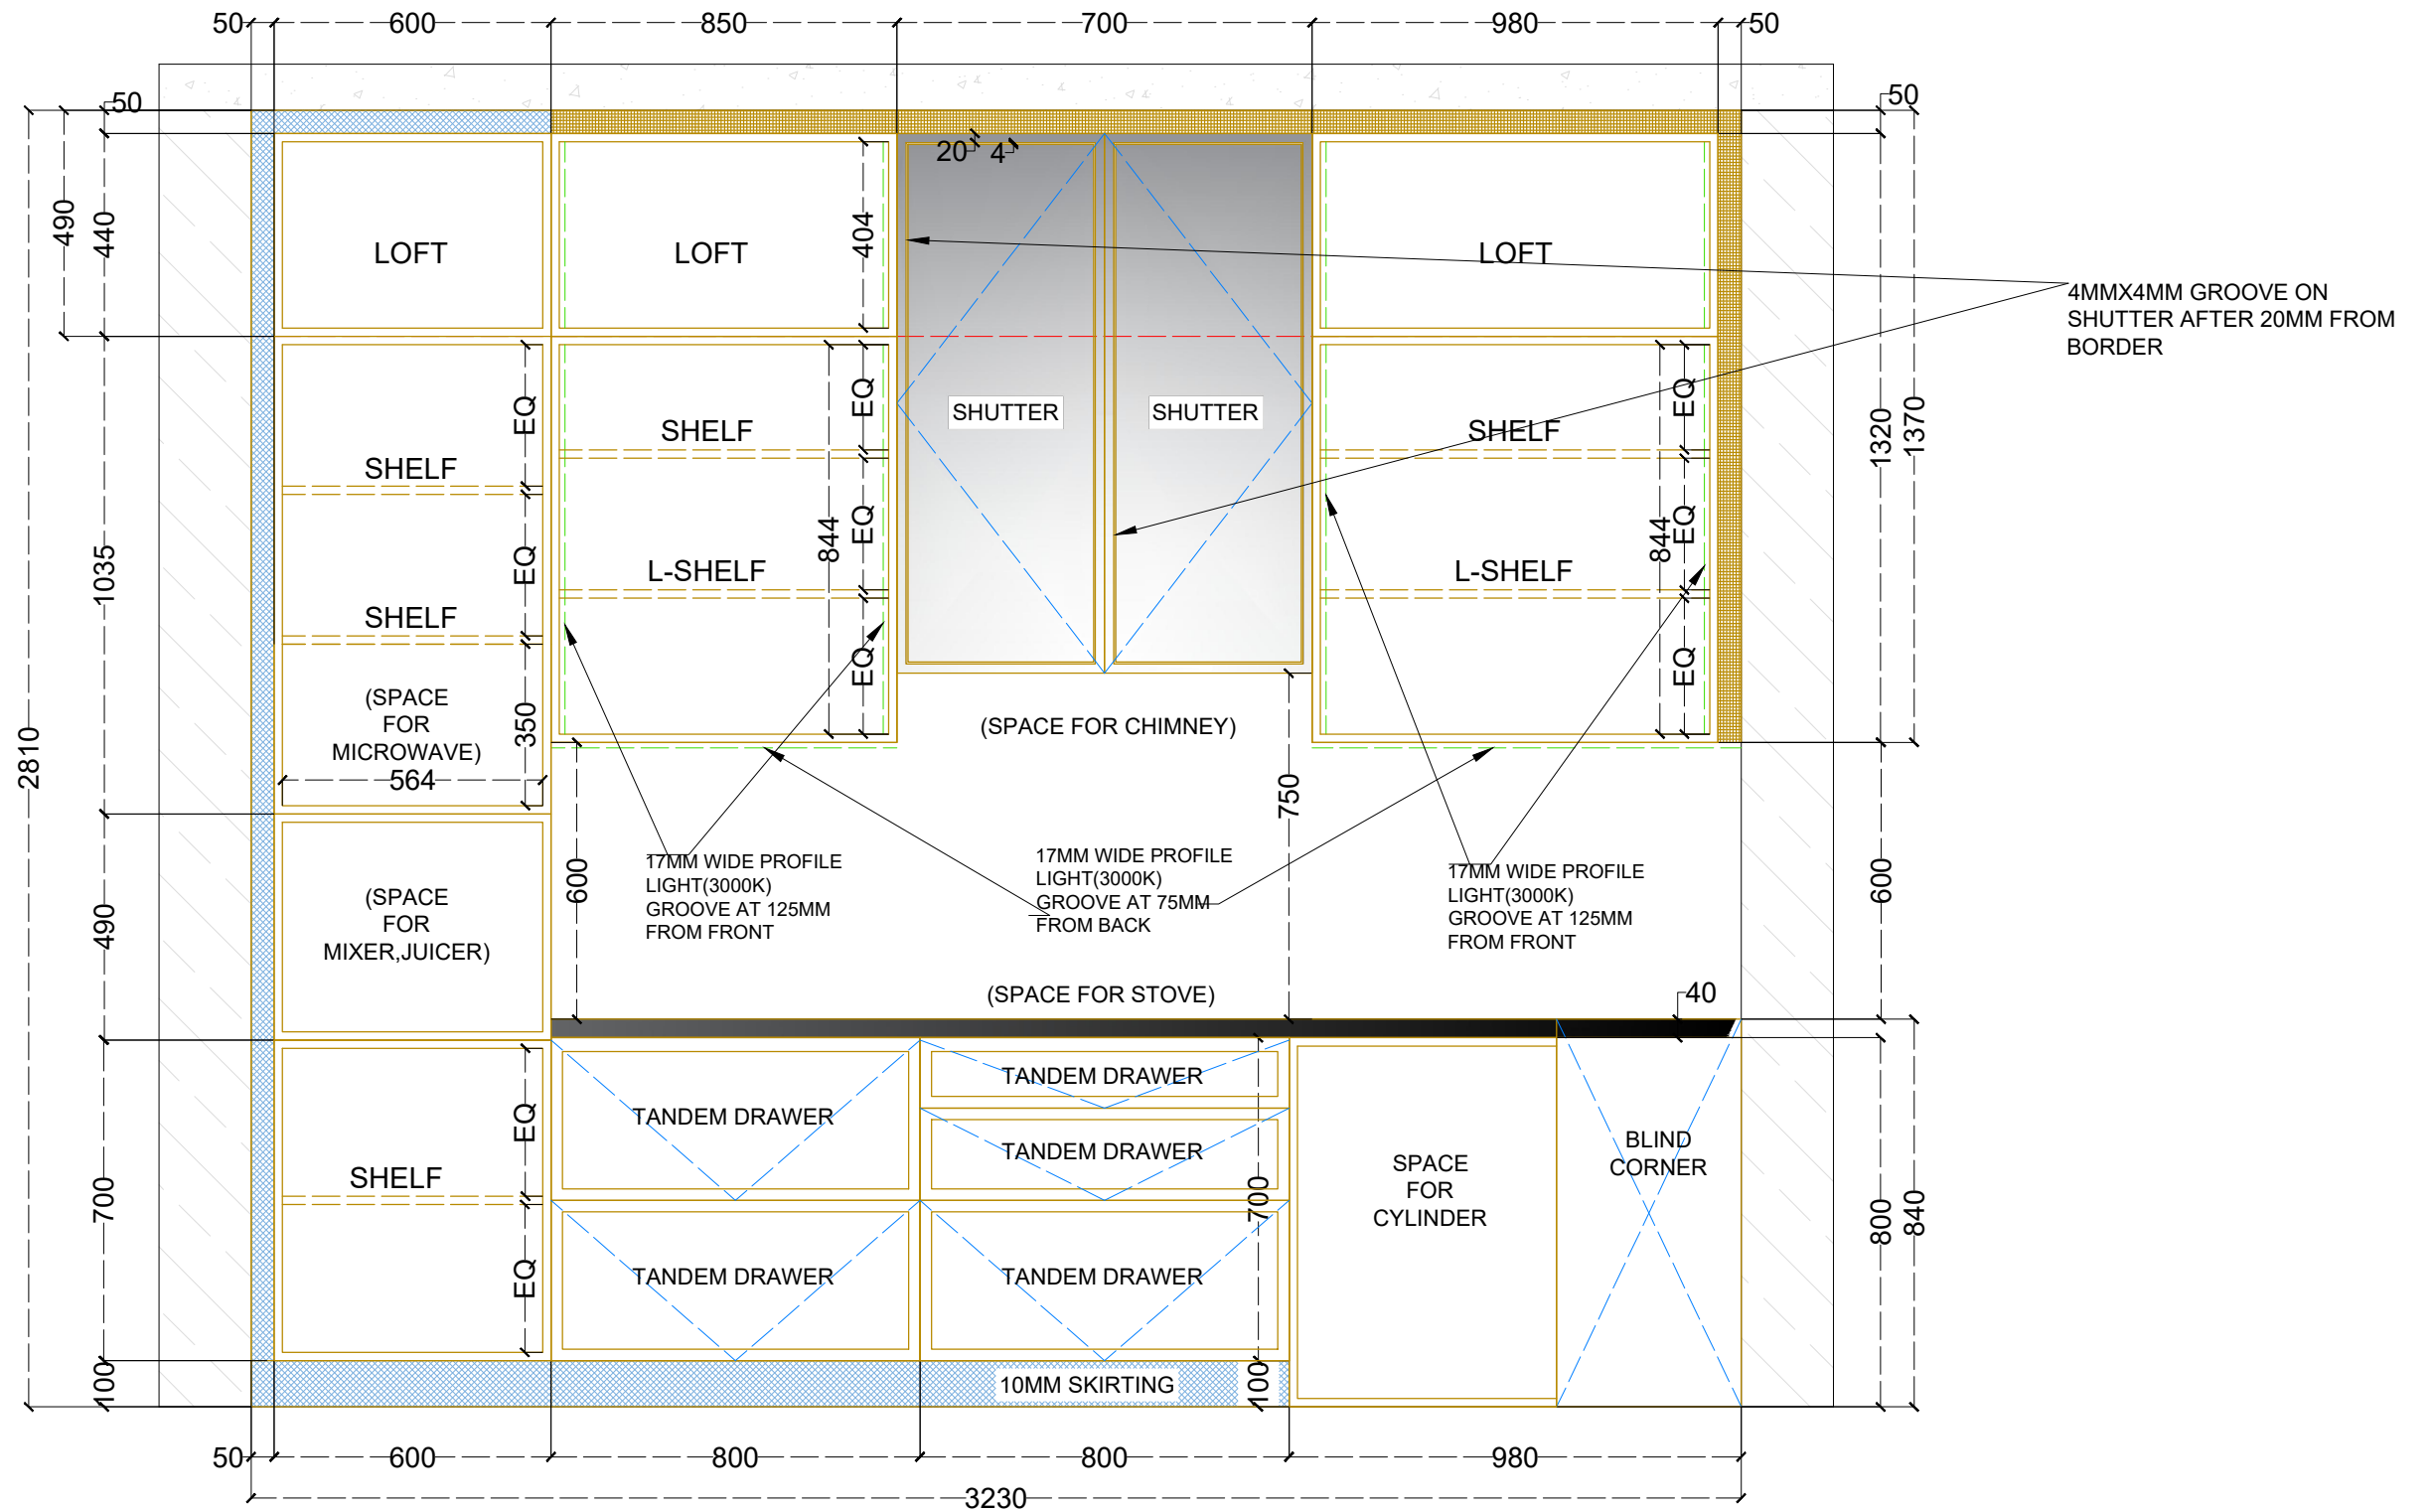


KITCHEN - ELEVATION C INTERNAL

TITLE : KITCHEN	DISINED BY : JITHESH K	PROPOSED INTERIORS FOR : PROJECT : DESIRE TREE CLIENT : Mr AMIT	 LISNO INDIA PRIVATE LIMITED H1/1, 402 Asher Enclave, Naigaon (E) Mumbai, Maharashtra-401208
DATE : 04/05/2026	CHECKED BY :		
PROJECT CODE : M064	HANDOVER DATE :		

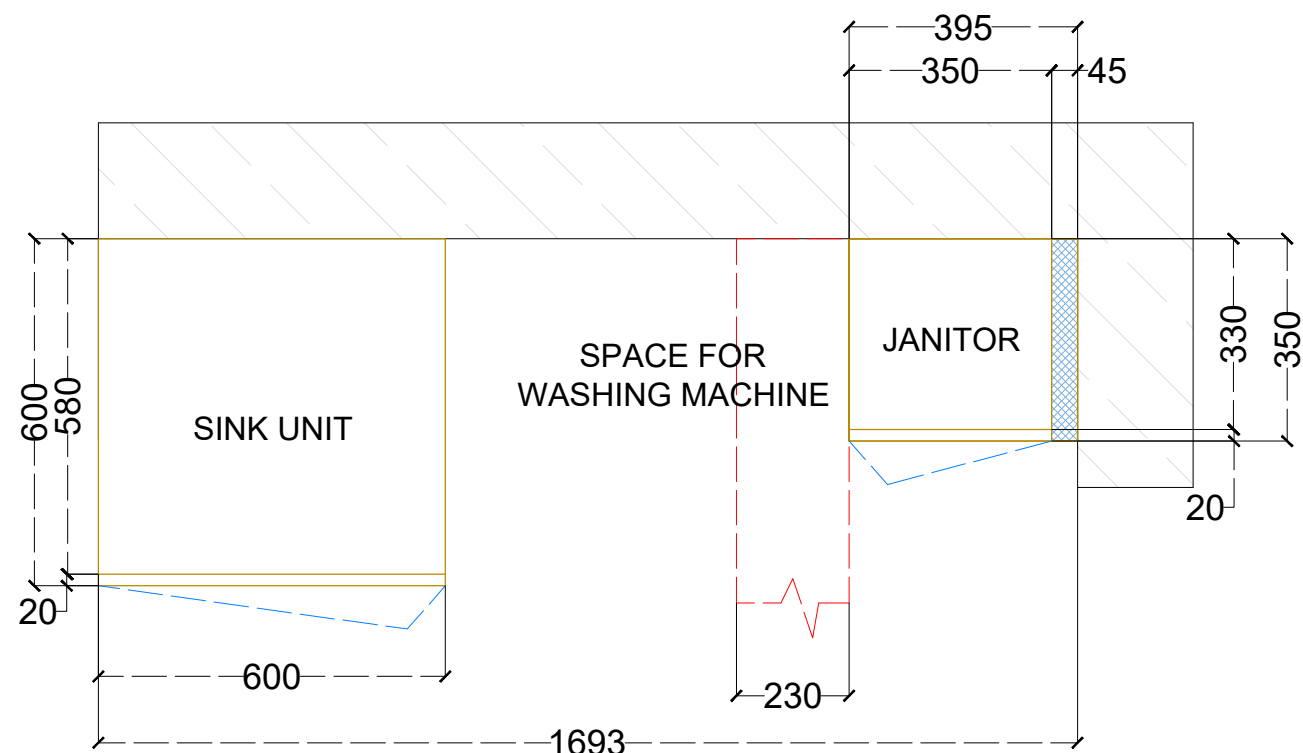

UTILITY - BASE UNIT PLAN

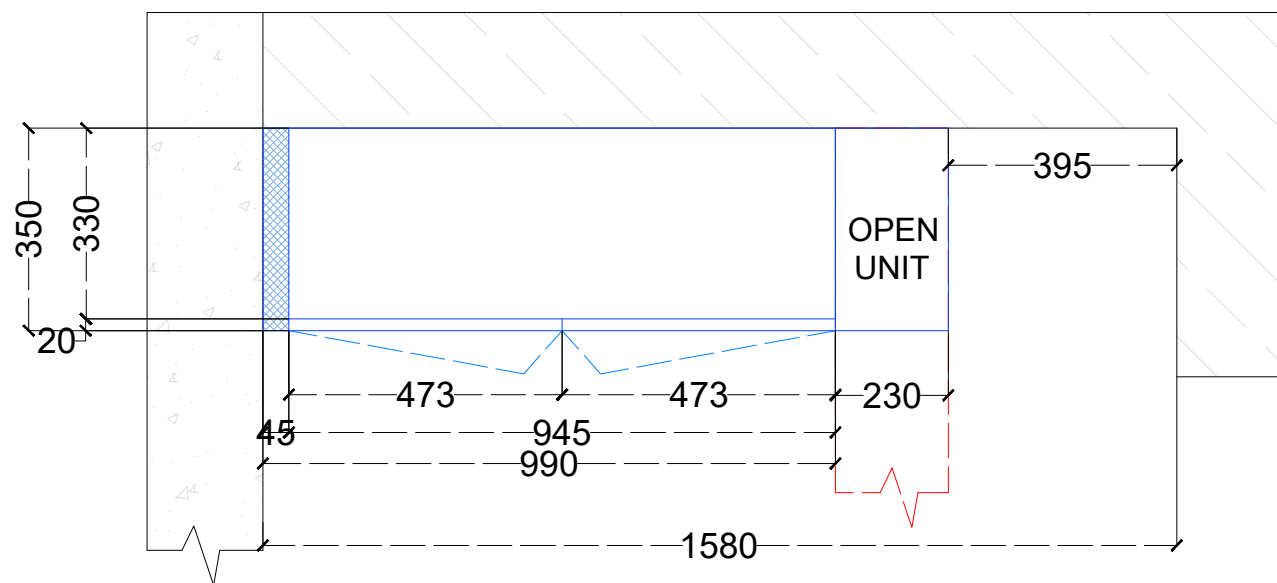

UTILITY - WALL UNIT PLAN

UTILITY UNIT - DETAIL SHEET

BASE UNIT & JANITOR

CORE MATERIAL	BWP ply
EXPOSED SIDE FINISH	MR-EL-28 LINEN HEX(ELEGORA)
SHUTER FASCIA FINISH	MR-EL-28 LINEN HEX(ELEGORA)
INTERNAL FINISH	220 MT/SF (SAFE DECOR)
VISIBLE EDGE BANDING COLOUR	MATCHING WITH LAMINATE

WALL - UNIT

CORE MATERIAL	BWP ply
EXPOSED SIDE FINISH	MR-EL-28 LINEN HEX(ELEGORA)
SHUTER FASCIA FINISH	MR-EL-28 LINEN HEX(ELEGORA)
INTERNAL FINISH	220 MT/SF (SAFE DECOR)
VISIBLE EDGE BANDING COLOUR	MATCHING WITH LAMINATE

FILLER & SKIRTING


CORE MATERIAL	BWP ply
SKIRTING FINISH	MR-EL-28 LINEN HEX(ELEGORA)
FILLER FINISH	MR-EL-28 LINEN HEX(ELEGORA)

HANDLE

BASE UNIT SHUTTER	SLANT CUT	1Nos
JANITOR SHUTTER	PUSH TO OPEN	1Nos
WALL UNIT SHUTTER	10MM EXTENSION ON BOTTOM	2Nos



220 MT/SF (SAFE DECOR)

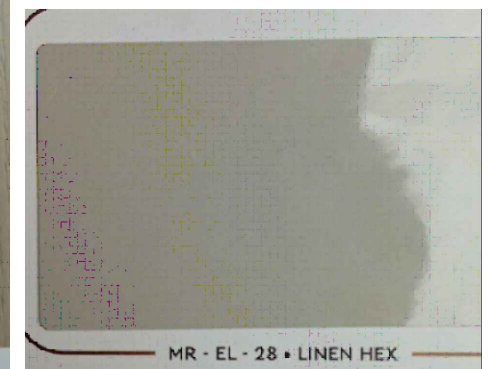

MR-EL-28 LINEN HEX(ELEGORA)

TITLE : UTILITY - UNIT

DISINED BY : JITHESH K

PROPOSED INTERIORS FOR :

DATE : 04/05/2026

CHECKED BY :

PROJECT : DESIRE TREE

PROJECT CODE : M064


HANDOVER DATE :

CLIENT : Mr AMIT




LISNO INDIA PRIVATE LIMITED

H1/1, 402 Asher Enclave, Naigaon (E) Mumbai,
Maharashtra-401208

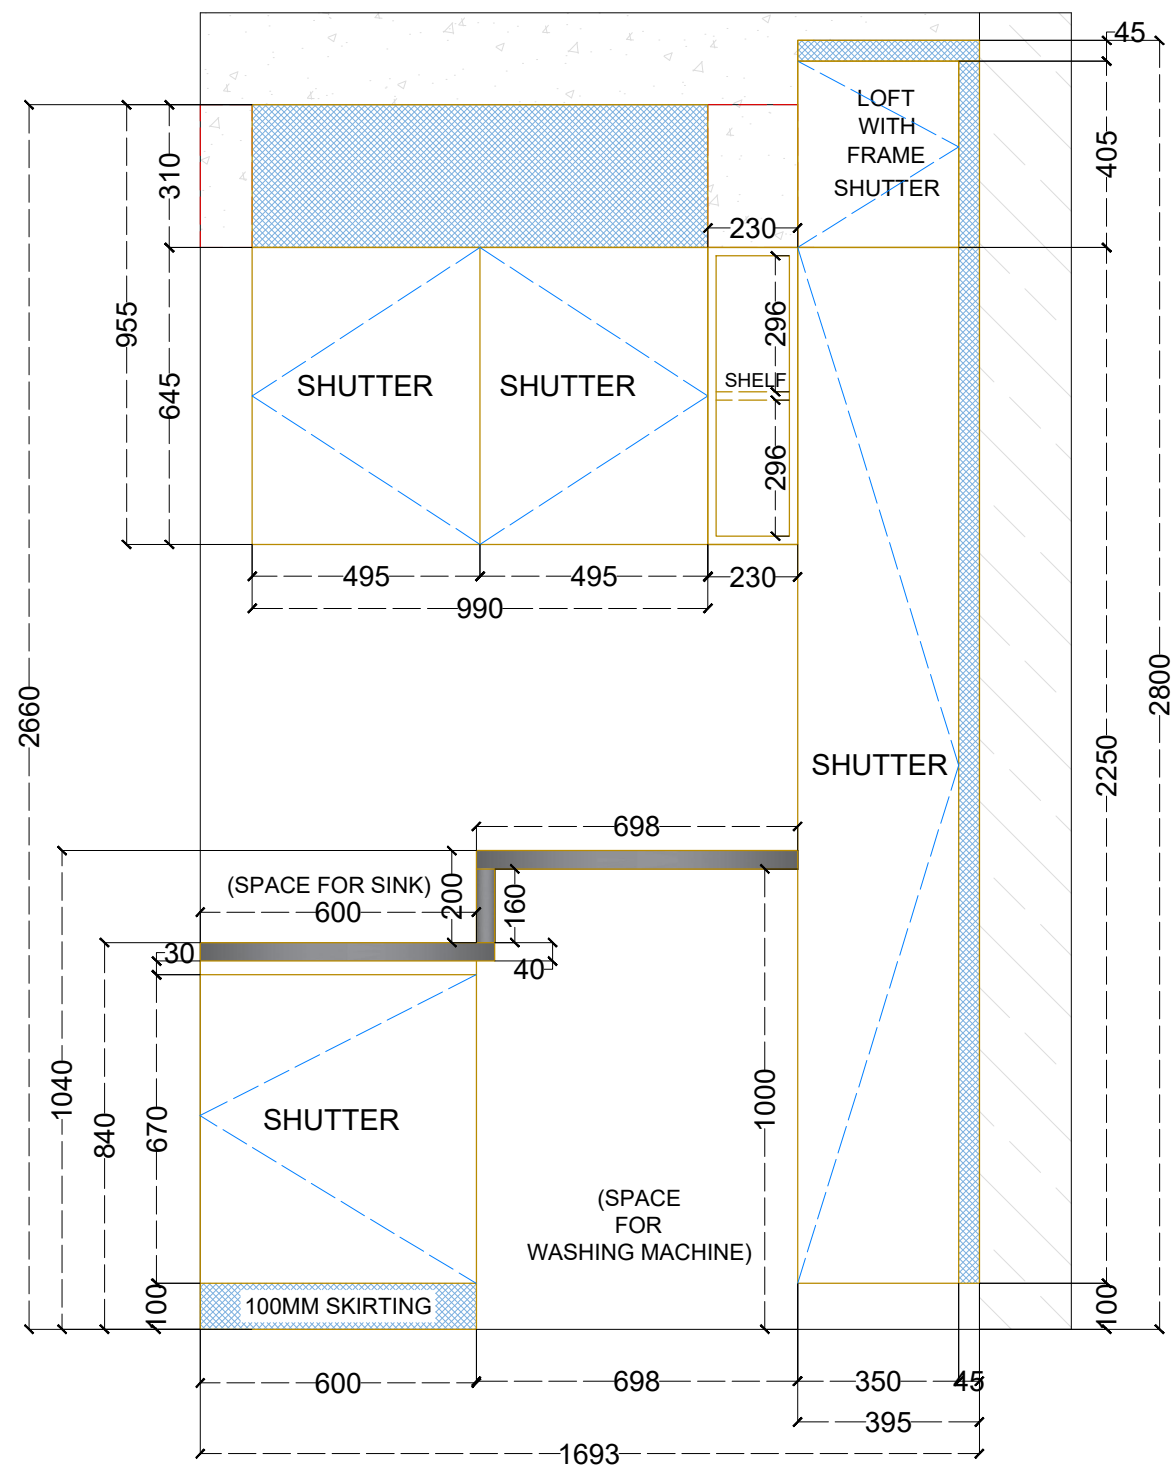

UTILITY - EXTERNAL

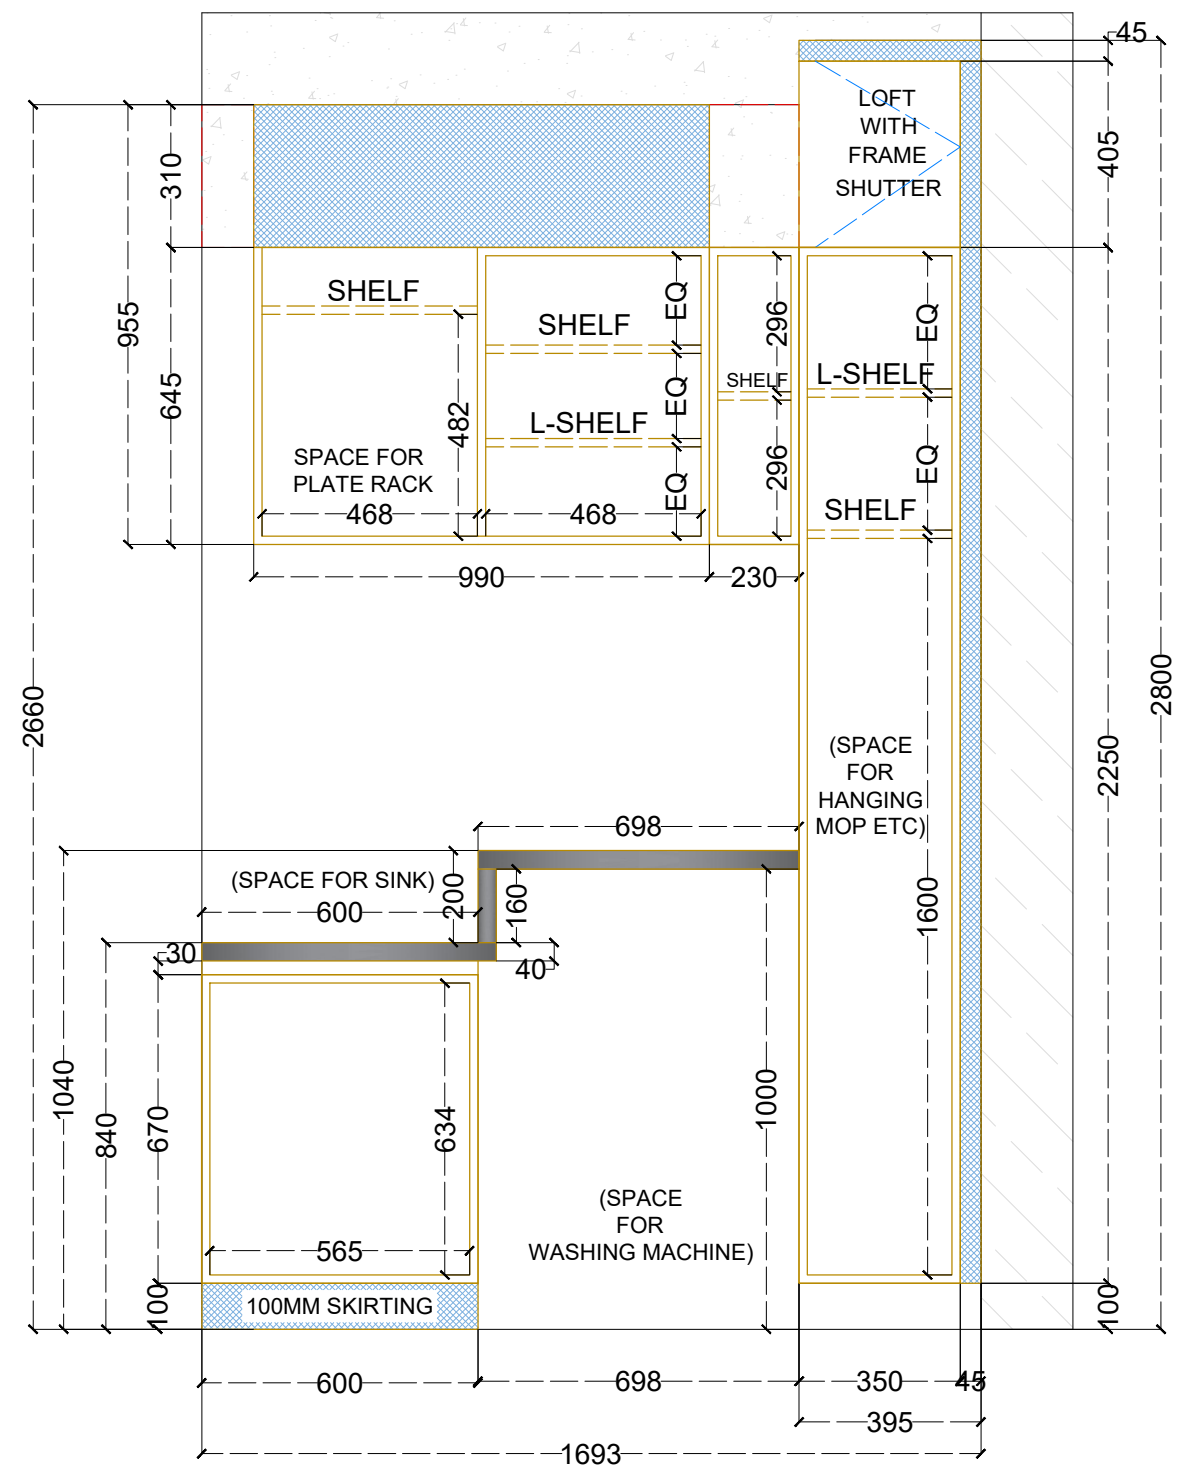

UTILITY - INTERNAL

TITLE : UTILITY - UNIT

DISINED BY : JITHESH K

DATE : 04/05/2026

CHECKED BY :

PROJECT CODE : M064

HANDOVER DATE :


PROPOSED INTERIORS FOR :

PROJECT : DESIRE TREE

CLIENT : Mr AMIT



LISNO INDIA PRIVATE LIMITED
H1/1, 402 Asher Enclave, Naigaon (E) Mumbai,
Maharashtra-401208

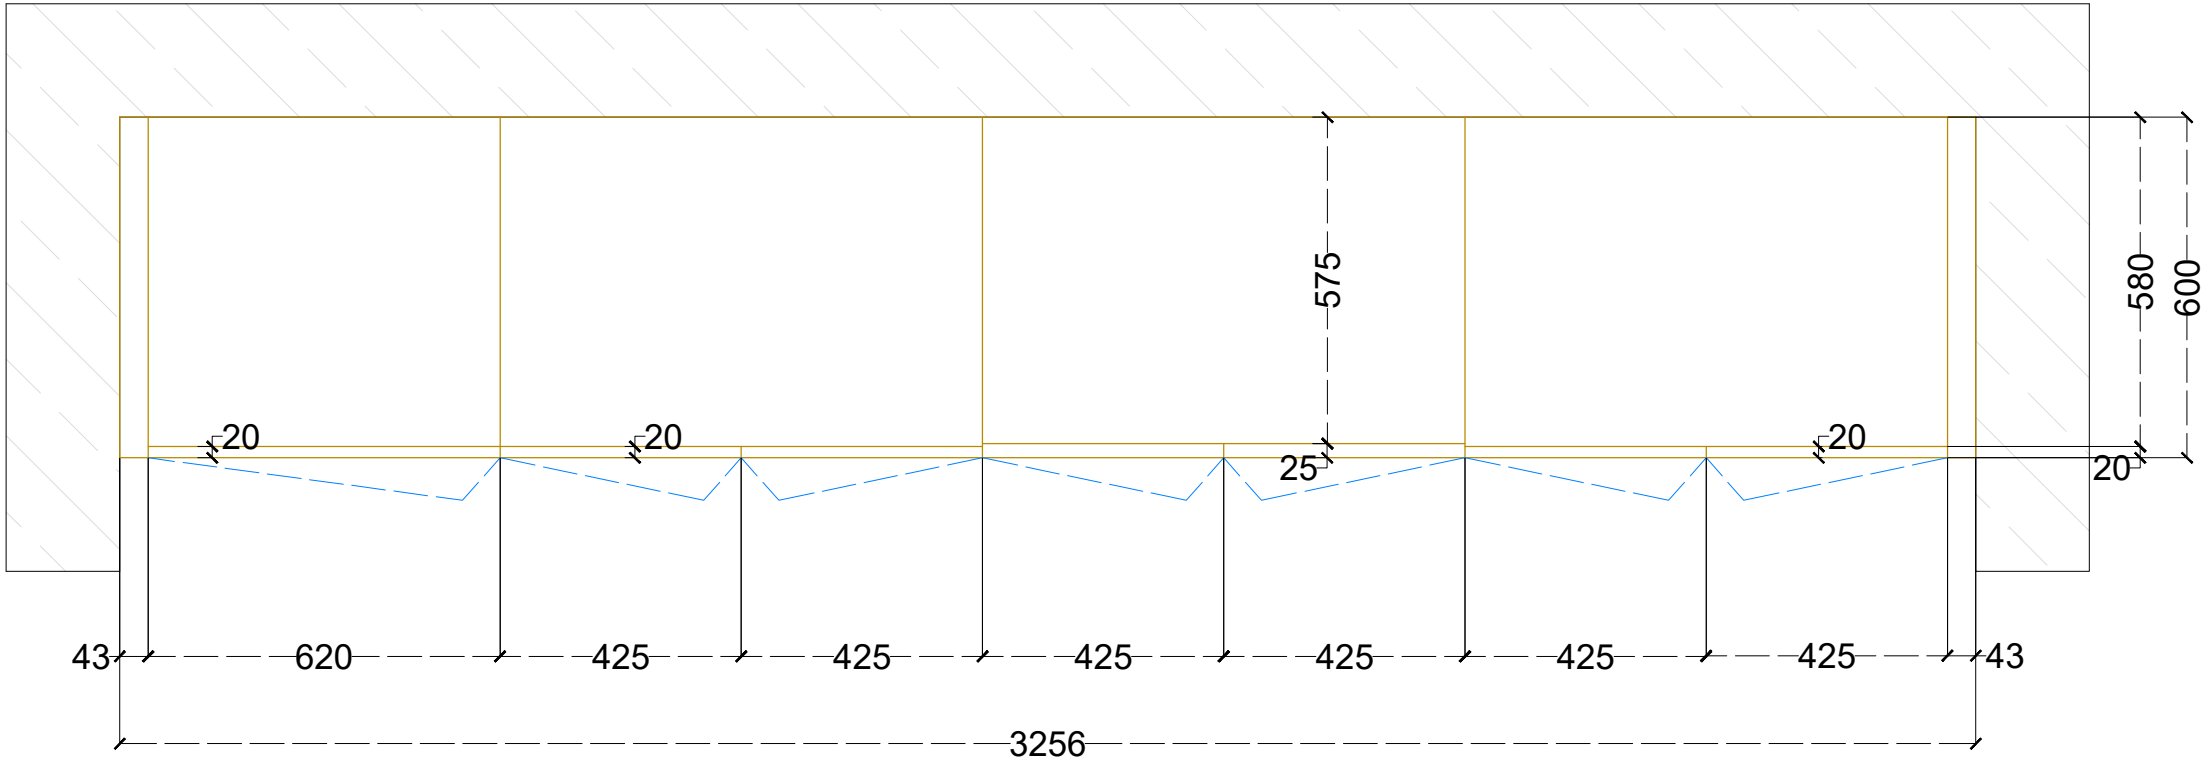


MBR WARDROBE - PLAN

TITLE : MBR - WARDROBE	DISINED BY : JITHESH K	PROPOSED INTERIORS FOR : PROJECT : DESIRE TREE CLIENT : Mr AMIT	 LISNO INDIA PRIVATE LIMITED H1/1, 402 Asher Enclave, Naigaon (E) Mumbai, Maharashtra-401208
DATE : 04/05/2026	CHECKED BY :		
PROJECT CODE : M064	HANDOVER DATE :		






TITLE : MBR - WARDROBE	DISIGNED BY : JITHESH K	PROPOSED INTERIORS FOR : PROJECT : DESIRE TREE CLIENT : Mr AMIT	 LISNO INDIA PRIVATE LIMITED H1/1, 402 Asher Enclave, Naigaon (E) Mumbai, Maharashtra-401208
DATE : 04/05/2026	CHECKED BY :		
PROJECT CODE : M064	HANDOVER DATE :		

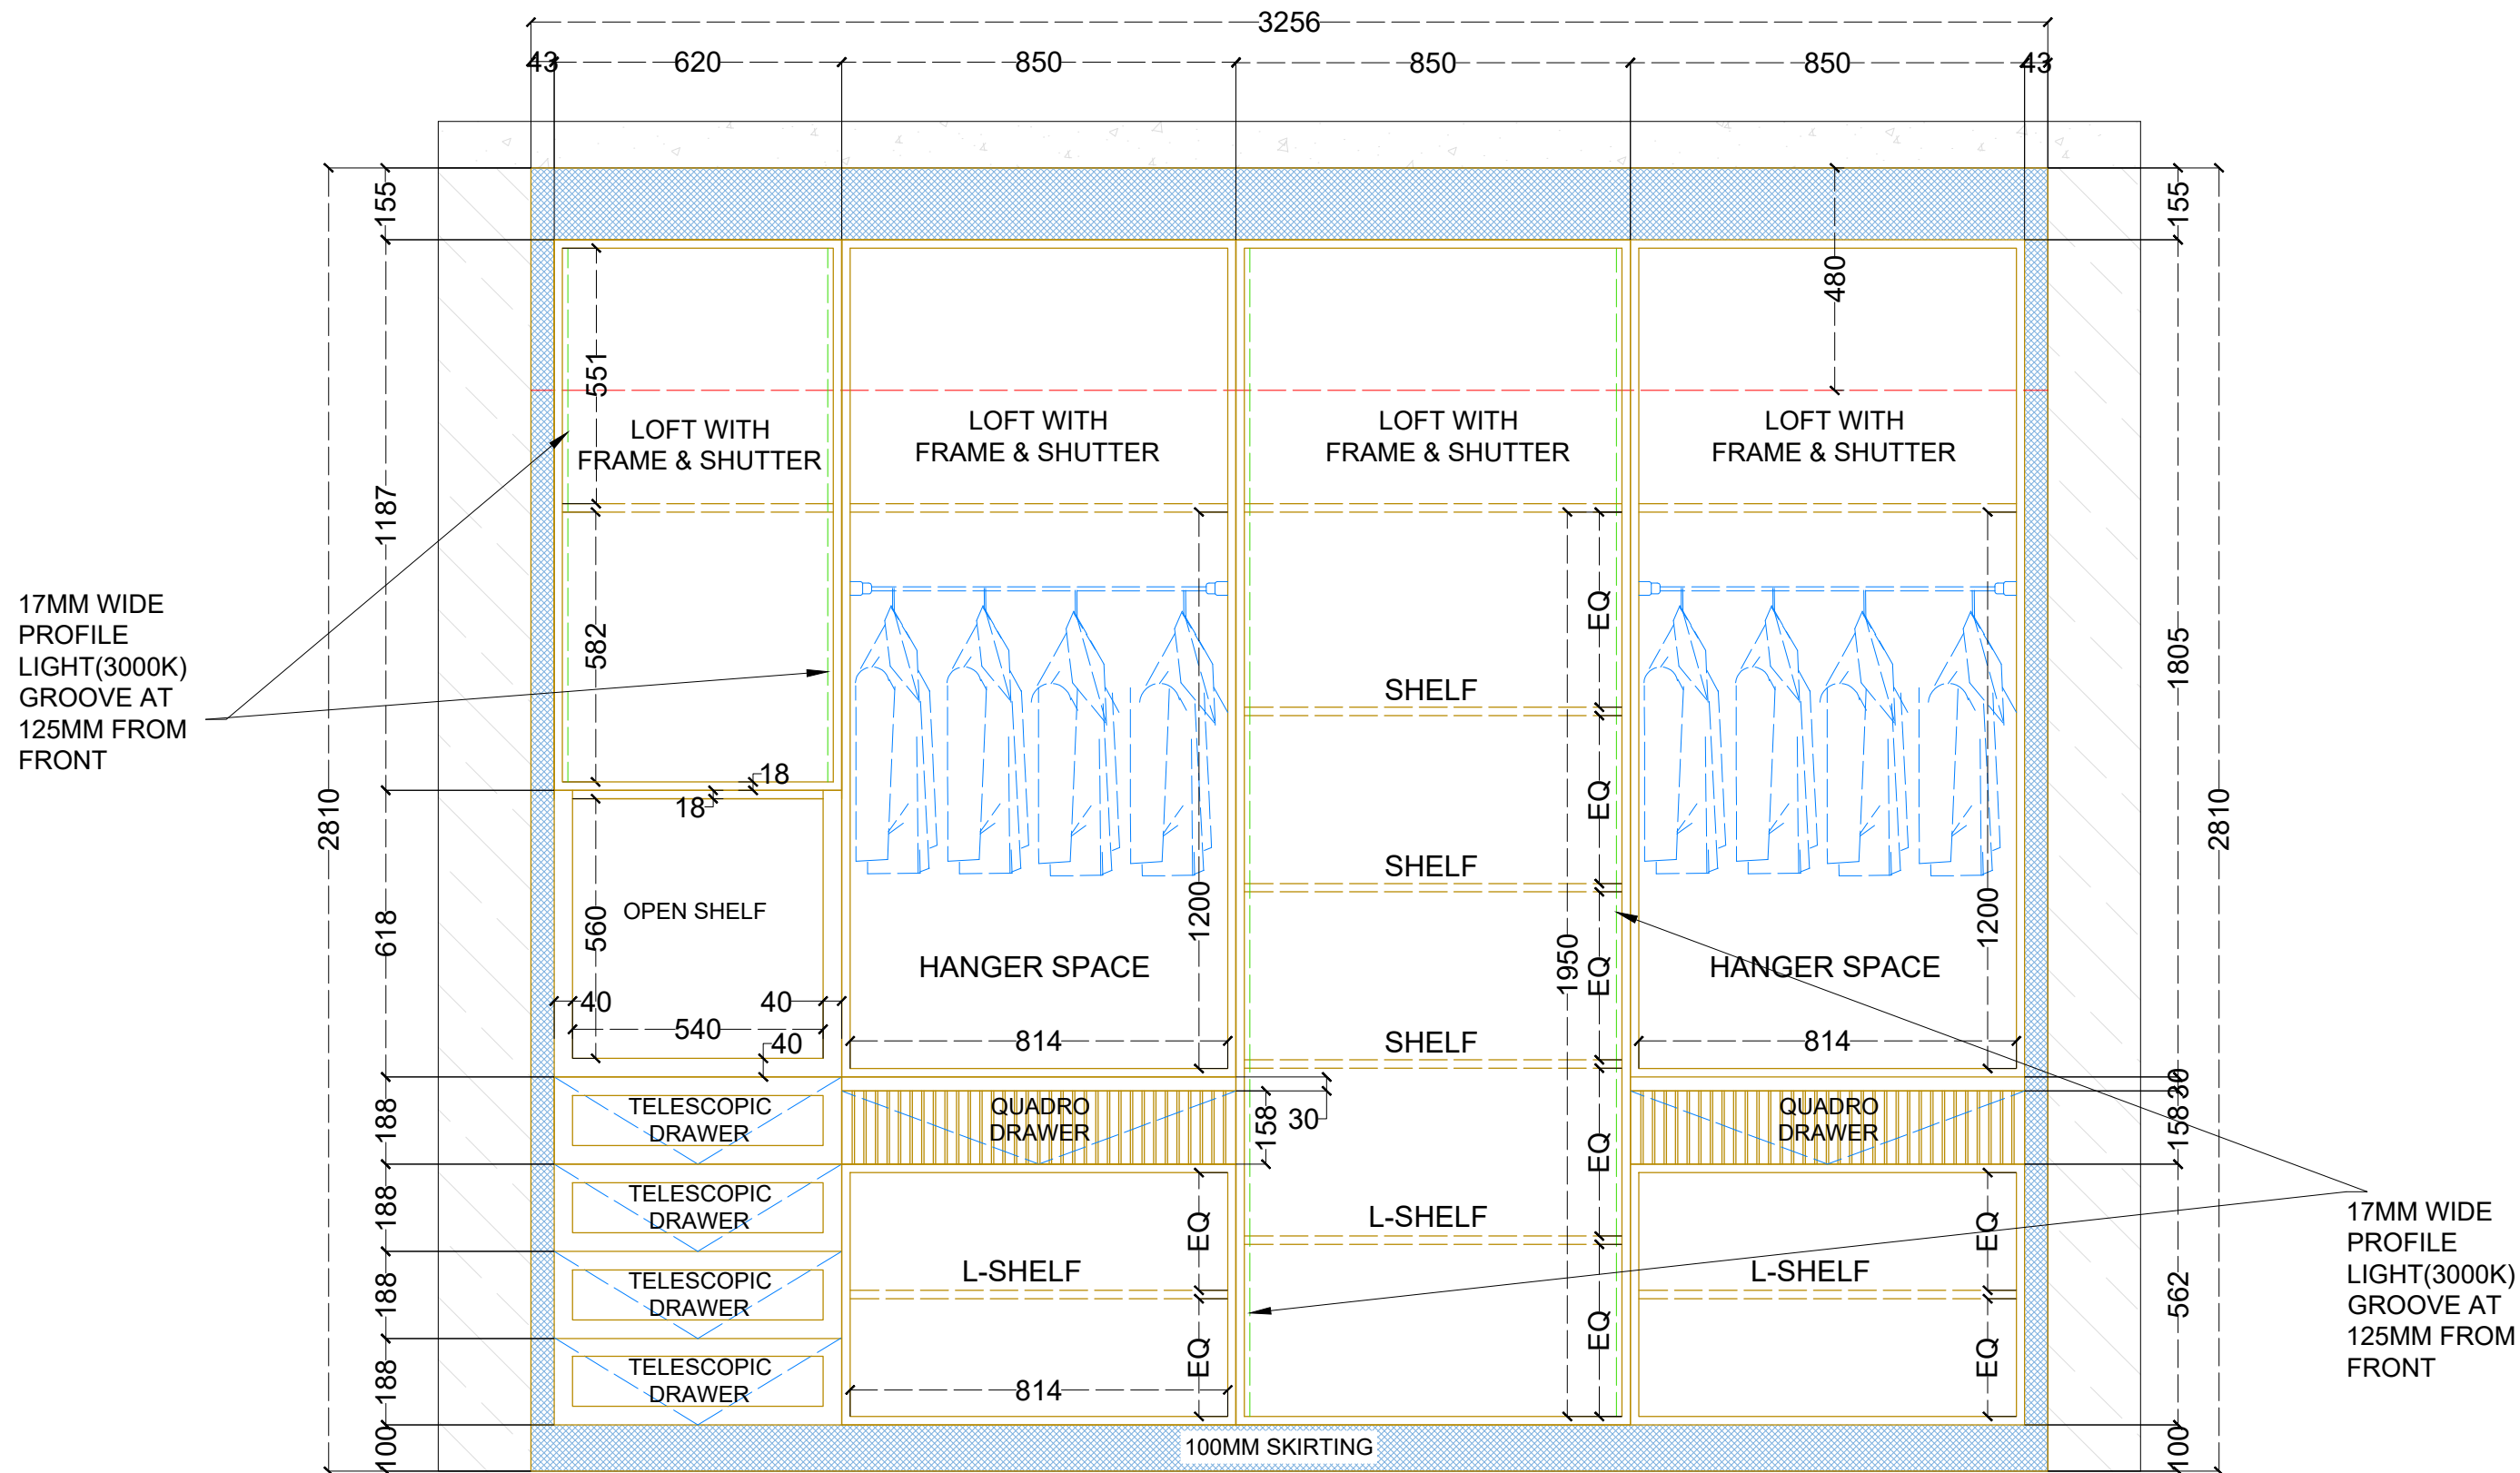

MBR WARDROBE - INTERNAL

TITLE : MBR - WARDROBE	DISINED BY : JITHESH K	PROPOSED INTERIORS FOR : PROJECT : DESIRE TREE CLIENT : Mr AMIT	 LISNO INDIA PRIVATE LIMITED H1/1, 402 Asher Enclave, Naigaon (E) Mumbai, Maharashtra-401208
DATE : 04/05/2026	CHECKED BY :		
PROJECT CODE : M064	HANDOVER DATE :		

MBR WARDROBE SHUTTER - DETAIL

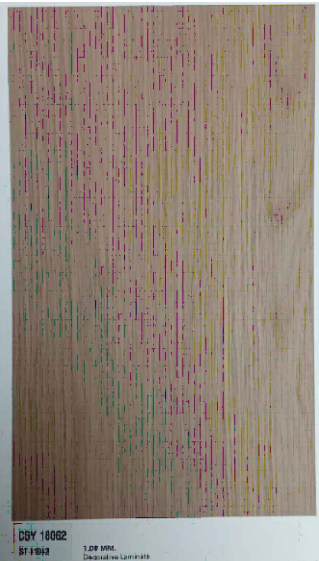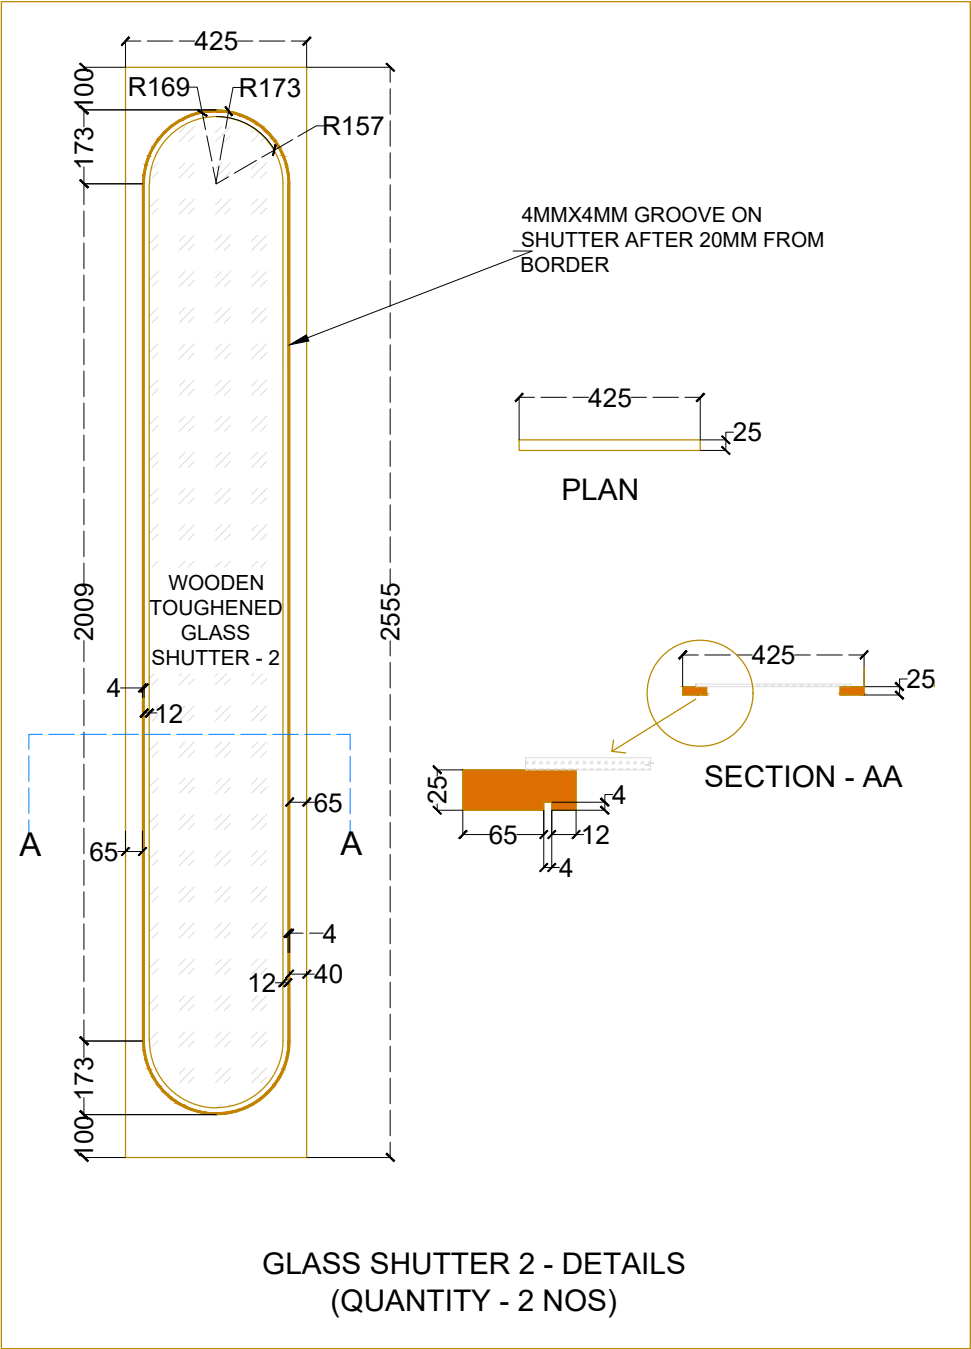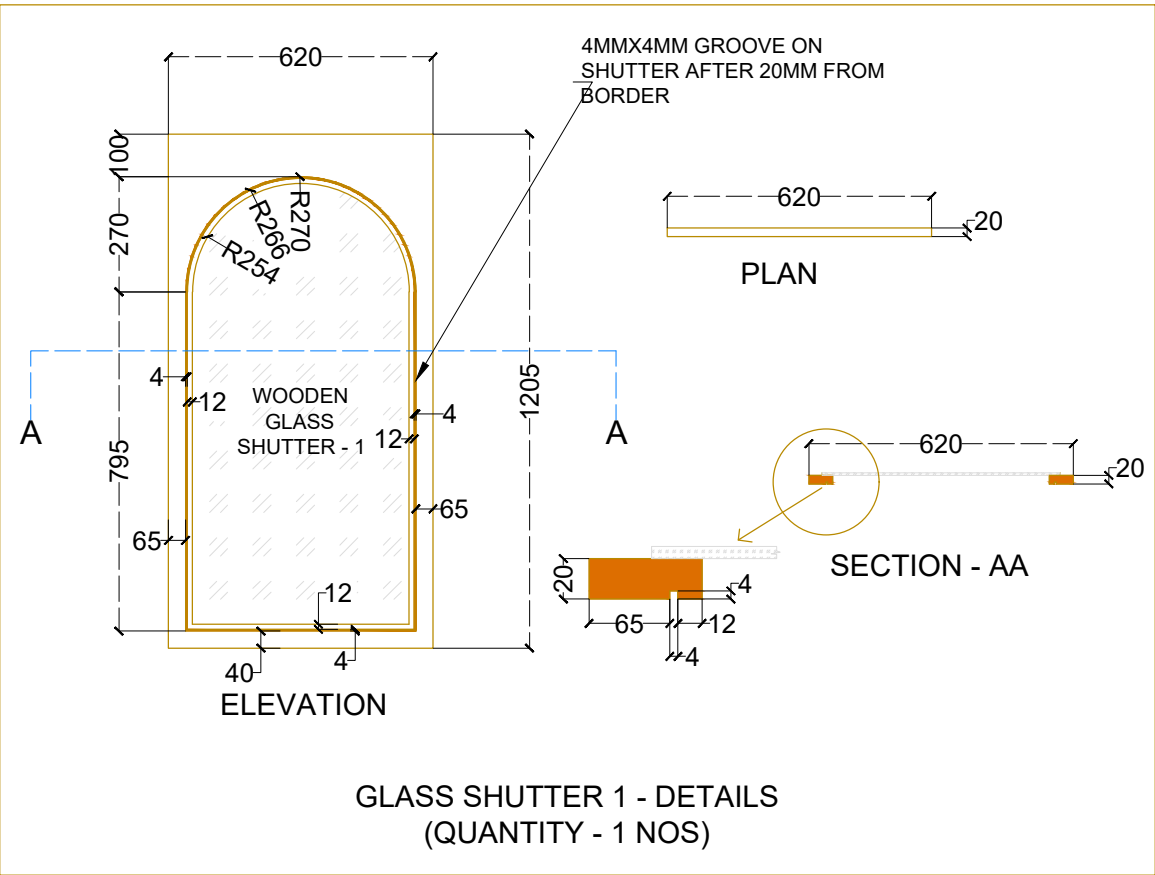



CSY 18062 (BEYOND LIMIT STORY)



BLACK TINTED FLUTED GLASS
(TOUGHENED)

TITLE : MBR WARDROBE SHUTTER	DISINED BY : JITHESH K	PROPOSED INTERIORS FOR : PROJECT : DESIRE TREE CLIENT : Mr AMIT	 LISNO INDIA PRIVATE LIMITED H1/1, 402 Asher Enclave, Naigaon (E) Mumbai, Maharashtra-401208
DATE : 04/05/2026	CHECKED BY :		
PROJECT CODE : M064	HANDOVER DATE :		

MBR WARDROBE SHUTTER - DETAIL

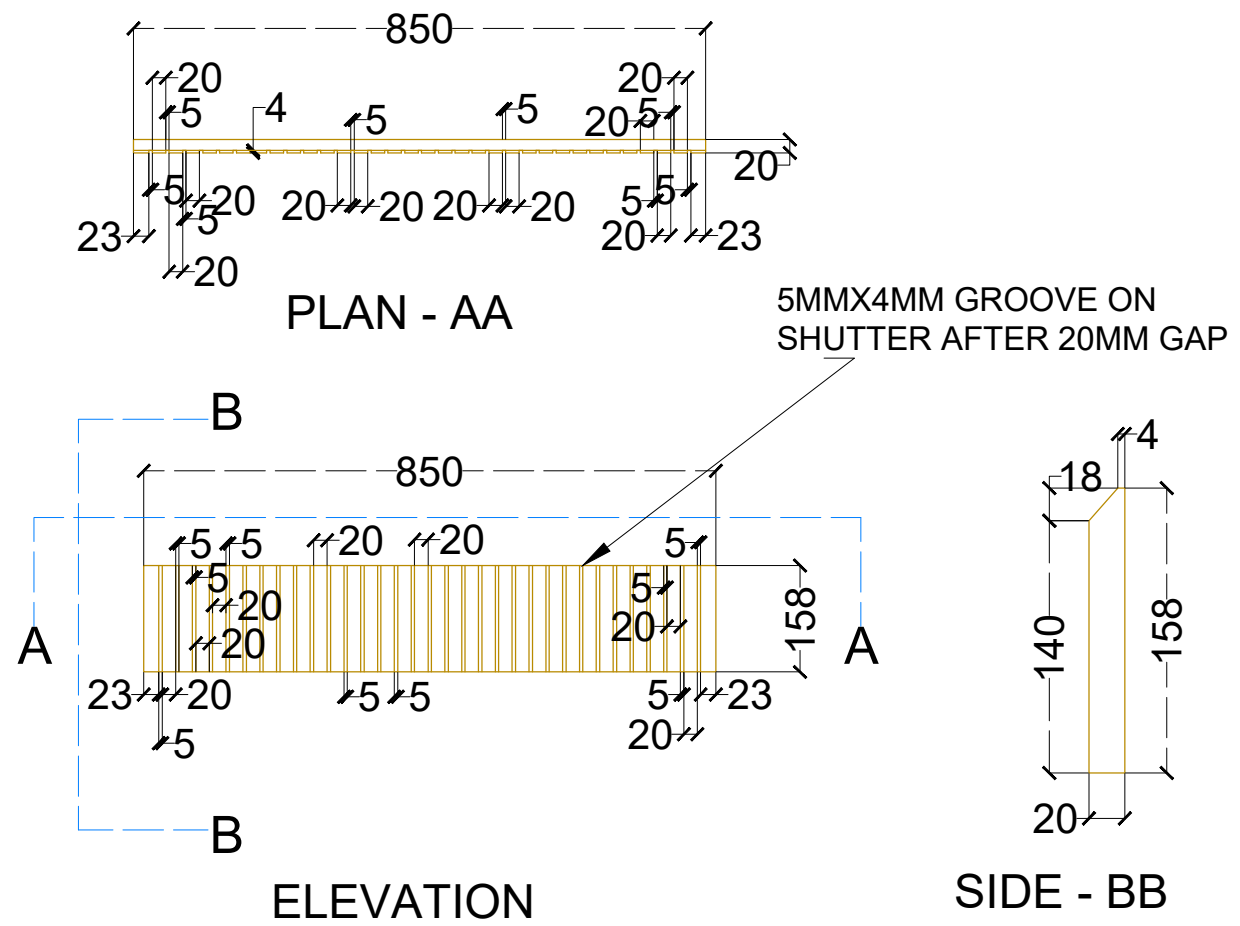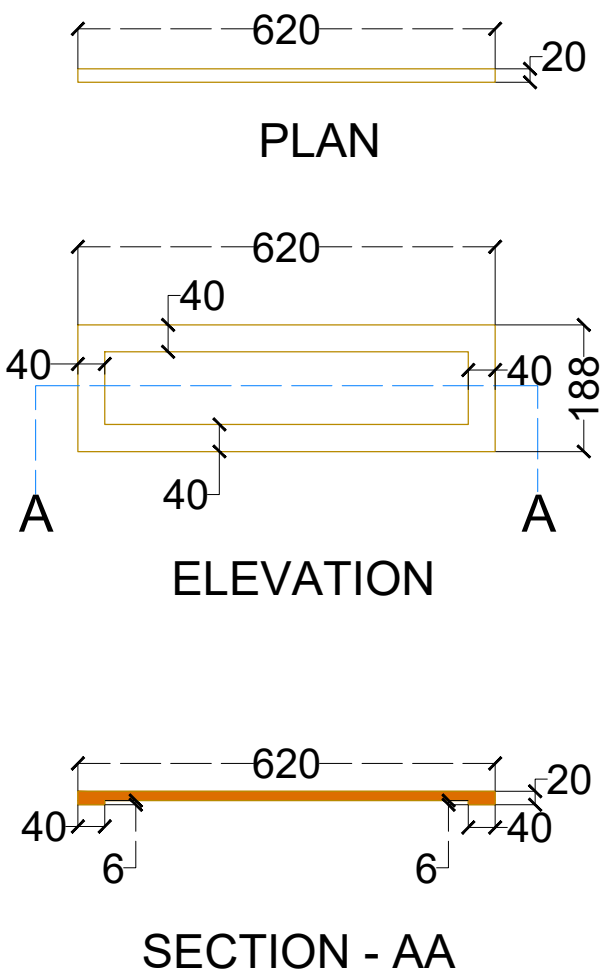



CSY 18062 (BEYOND LIMIT STORY)

TELESCOPIC DRAWER FASCIA - DETAILS
(QUANTITY - 4 NOS)

QUADRO DRAWER FASCIA - DETAILS
(QUANTITY - 2 NOS)

TITLE : MBR WARDROBE SHUTTER	DISINED BY : JITHESH K	PROPOSED INTERIORS FOR : PROJECT : DESIRE TREE CLIENT : Mr AMIT	 LISNO INDIA PRIVATE LIMITED H1/1, 402 Asher Enclave, Naigaon (E) Mumbai, Maharashtra-401208
DATE : 04/05/2026	CHECKED BY :		
PROJECT CODE : M064	HANDOVER DATE :		

MBR WARDROBE SHUTTER - DETAIL

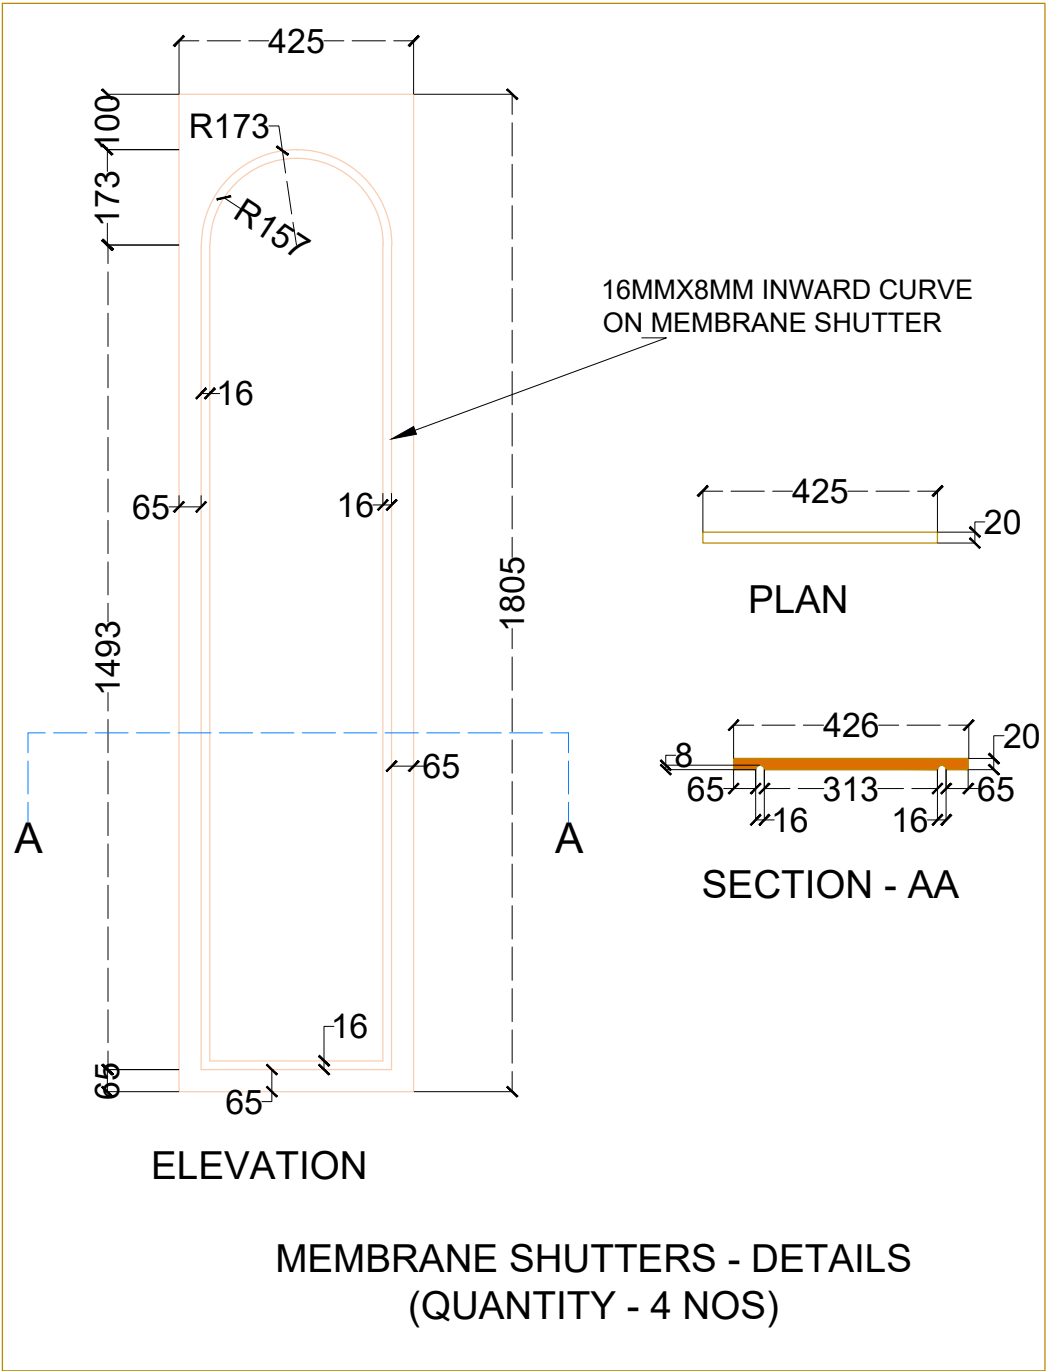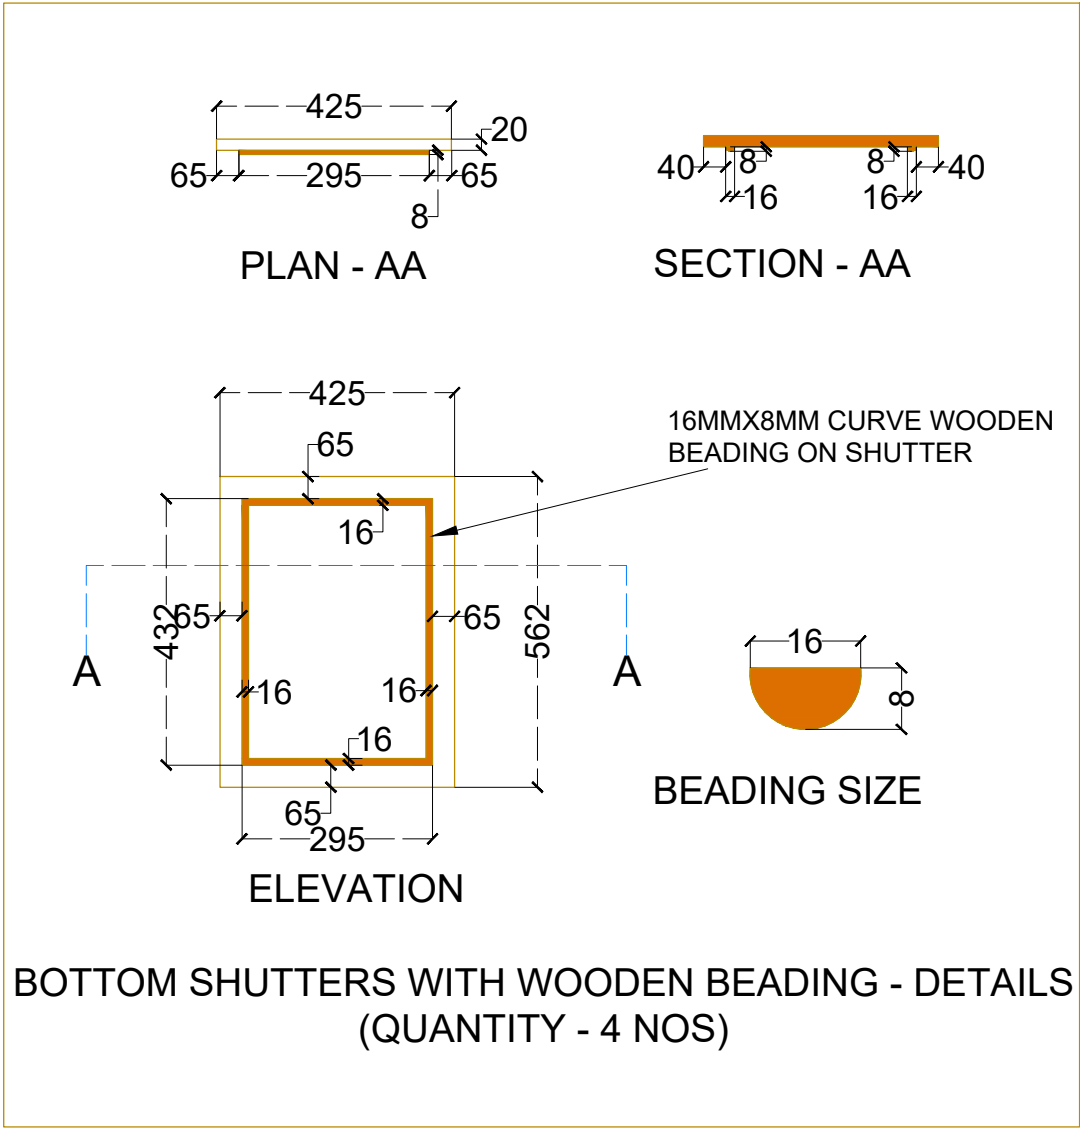

CSY 18062 (BEYOND LIMIT STORY)



NOVA MAGNOLIA (RENOLIT - MEMBRANE FINISH)

TITLE : MBR WARDROBE SHUTTER	DISINED BY : JITHESH K	PROPOSED INTERIORS FOR : PROJECT : DESIRE TREE CLIENT : Mr AMIT	 LISNO INDIA PRIVATE LIMITED H1/1, 402 Asher Enclave, Naigaon (E) Mumbai, Maharashtra-401208
DATE : 04/05/2026	CHECKED BY :		
PROJECT CODE : M064	HANDOVER DATE :		

MBR DRESSER UNIT - DETAIL SHEET

BASE UNIT

CORE MATERIAL	MR ply
EXPOSED SIDE FINISH	1417 (SLOAN - CORK SHEET)
DRAWER & SHUTER FASCIA FINISH	1417 (SLOAN - CORK SHEET)
INTERNAL FINISH	220 MT/SF (SAFE DECOR)
VISIBLE EDGE BANDING COLOUR	MATCHING WITH LAMINATE

WALL - UNIT

CORE MATERIAL	MR ply
EXPOSED SIDE FINISH	CSY 18062 (BEYOND LIMIT STORY)
GLASS SHUTER - GLASS	BLACK TINTED FLUTED (TOUGHENED)
GLASS SHUTER - PROFILE	BLACK
INTERNAL FINISH	220 MT/SF (SAFE DECOR)
VISIBLE EDGE BANDING COLOUR	MATCHING WITH LAMINATE

FILLER & SKIRTING



CORE MATERIAL	MR ply
SKIRTING FINISH	1417 (SLOAN - CORK SHEET)
FILLER FINISH	1417 (SLOAN - CORK SHEET)

FLUTED PANEL


FLUTED PANEL CODE	WD-3048 (WIDE DECOR-S4)
-------------------	-------------------------

HANDLES

BASE UNIT DRAWER	KNOB	2 Nos
BASE UNIT SHUTTER	KNOB	1 Nos
WALL UNIT	BINDI PROFILE HANDLE	1 Nos

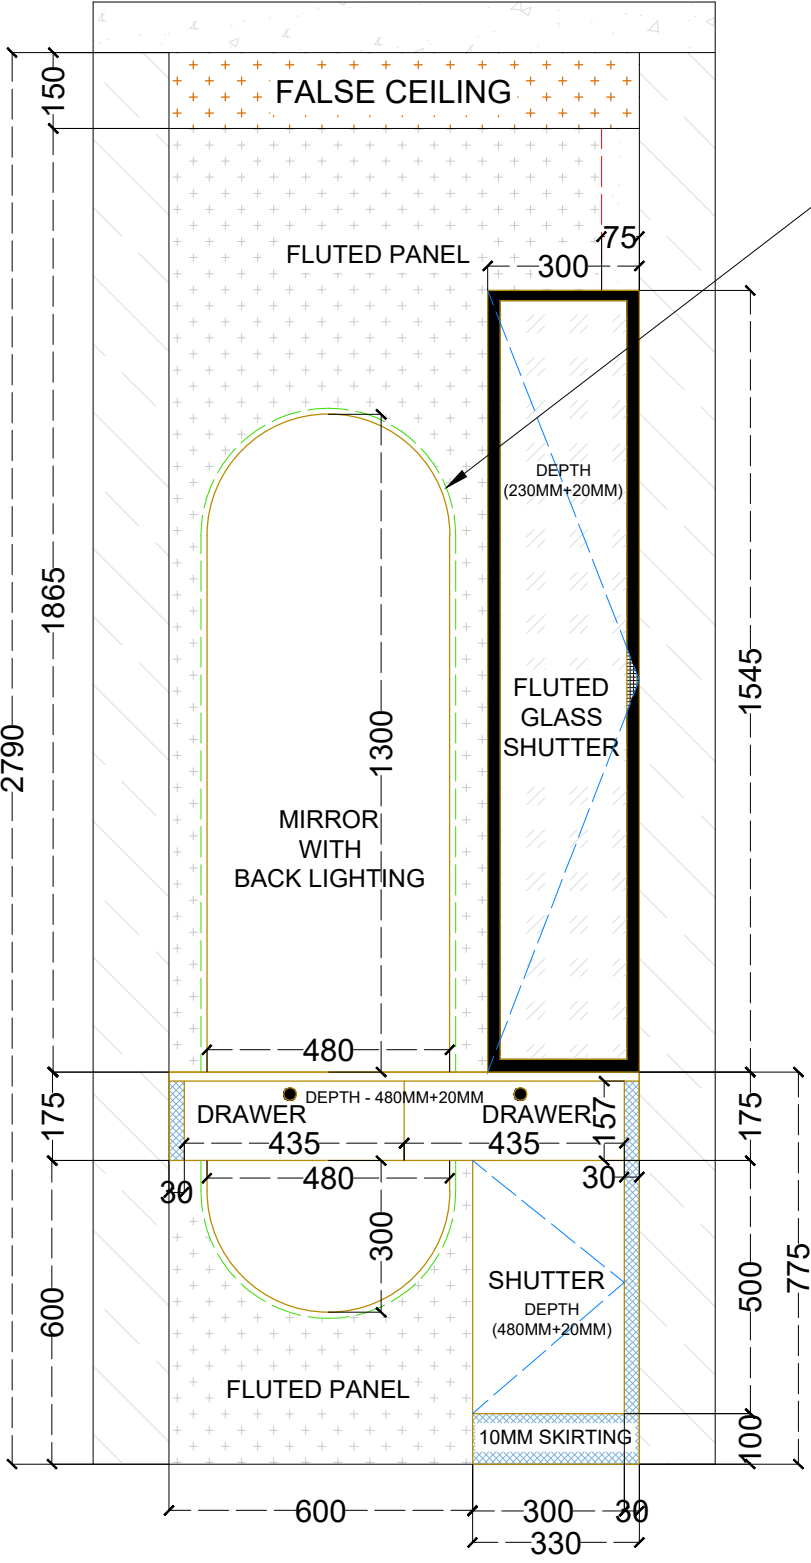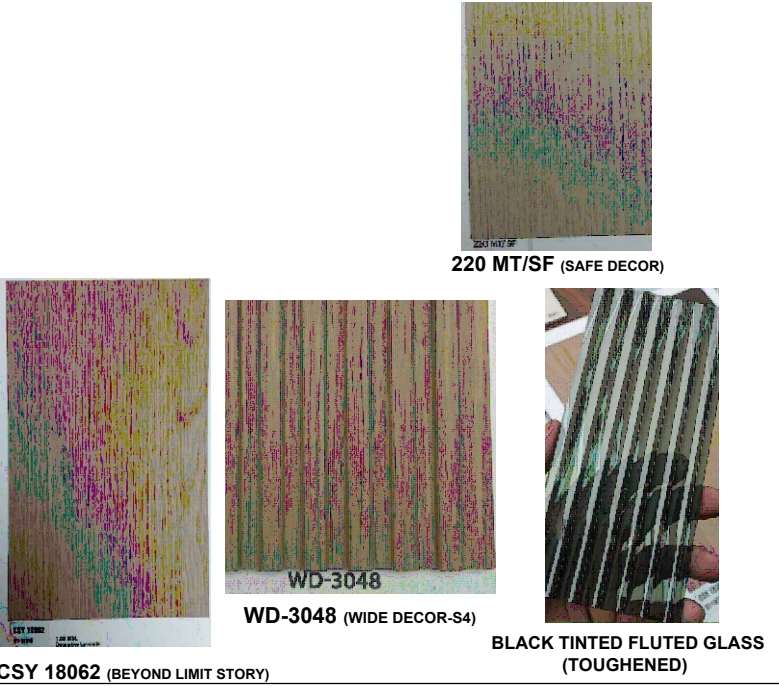


MBR DRESSER - ELEVATION

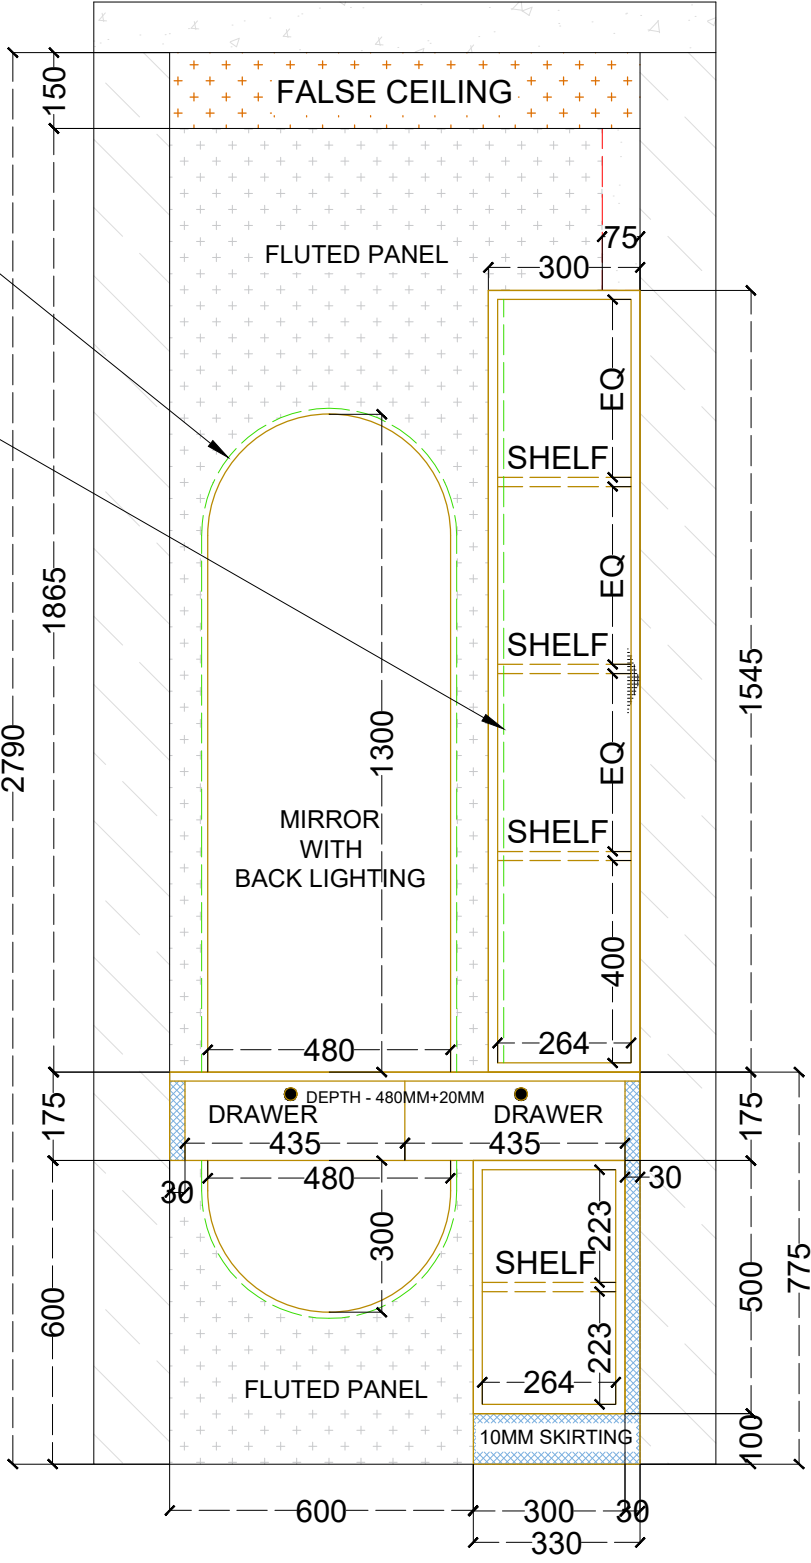

MBR DRESSER - INTERNAL

TITLE : MBR DRESSER UNIT	DISINED BY : JITHESH K	PROPOSED INTERIORS FOR : PROJECT : DESIRE TREE CLIENT : Mr AMIT	 LISNO INDIA PRIVATE LIMITED H1/1, 402 Asher Enclave, Naigaon (E) Mumbai, Maharashtra-401208
DATE : 04/05/2026	CHECKED BY :		
PROJECT CODE : M064	HANDOVER DATE :		

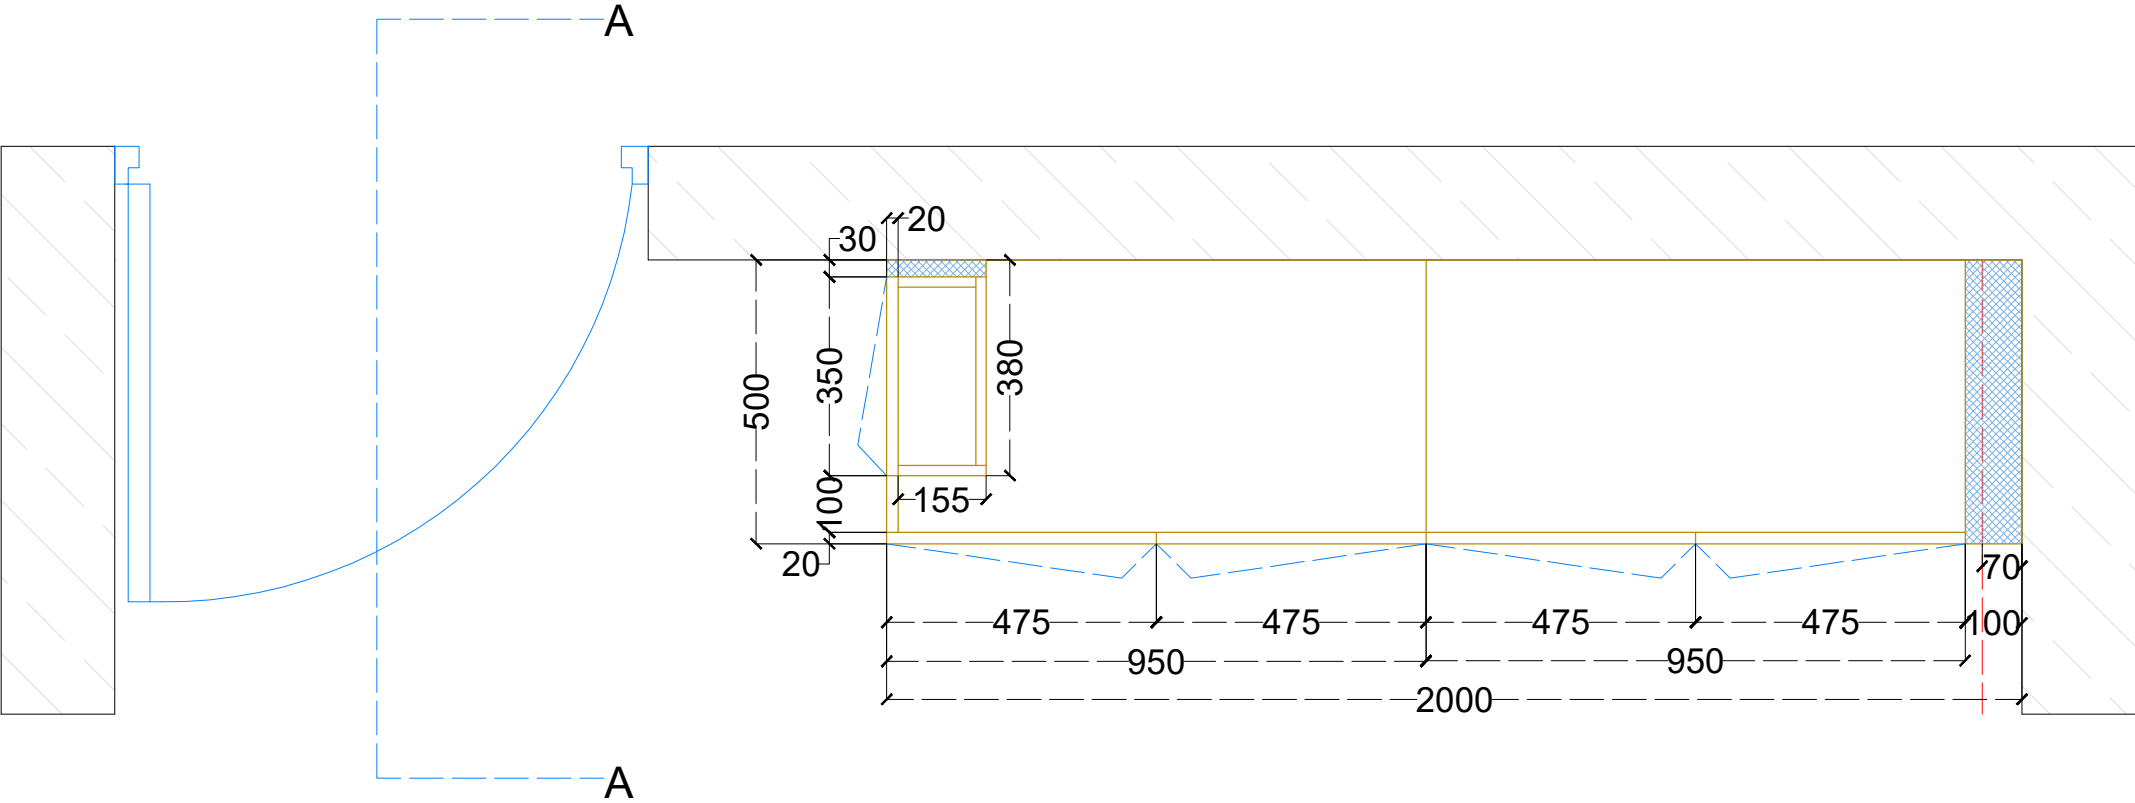

PBR WARDROBE - PLAN

TITLE : PBR - WARDROBE	DISINED BY : JITHESH K	PROPOSED INTERIORS FOR : PROJECT : DESIRE TREE CLIENT : Mr AMIT	 LISNO INDIA PRIVATE LIMITED H1/1, 402 Asher Enclave, Naigaon (E) Mumbai, Maharashtra-401208
DATE : 04/05/2026	CHECKED BY :		
PROJECT CODE : M064	HANDOVER DATE :		

PBR WARDROBE - DETAIL SHEET

WADROBE UNIT


CORE MATERIAL	MR ply
EXPOSED SIDE FINISH	CSY 18062 (BEYOND LIMIT STORY)
SHUTER FASCIA FINISH 1	CSY 18062 (BEYOND LIMIT STORY)
SHUTER FASCIA FINISH 2	OT 2153 (RESHAM)
INTERNAL FINISH	220 MT/SF (SAFE DECOR)
VISIBLE EDGE BANDING COLOUR	MATCHING WITH LAMINATE

FILLER & SKIRTING


CORE MATERIAL	MR ply
SKIRTING FINISH	CSY 18062 (BEYOND LIMIT STORY)
FILLER FINISH	CSY 18062 (BEYOND LIMIT STORY)

HANDLE

TOP SHUTTER	HANDLE	4Nos
BOTTOM SHUTTER	KNOB	4Nos
SIDE SHUTTER (USED CLOTHES STORAGE)	PUSH TO OPEN	1Nos

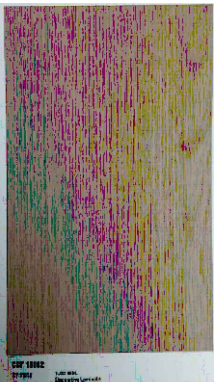


CSY 18062 (BEYOND LIMIT STORY)

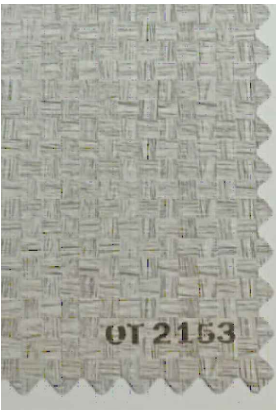

OT 2153 (RESHAM)




220 MT/SF (SAFE DECOR)

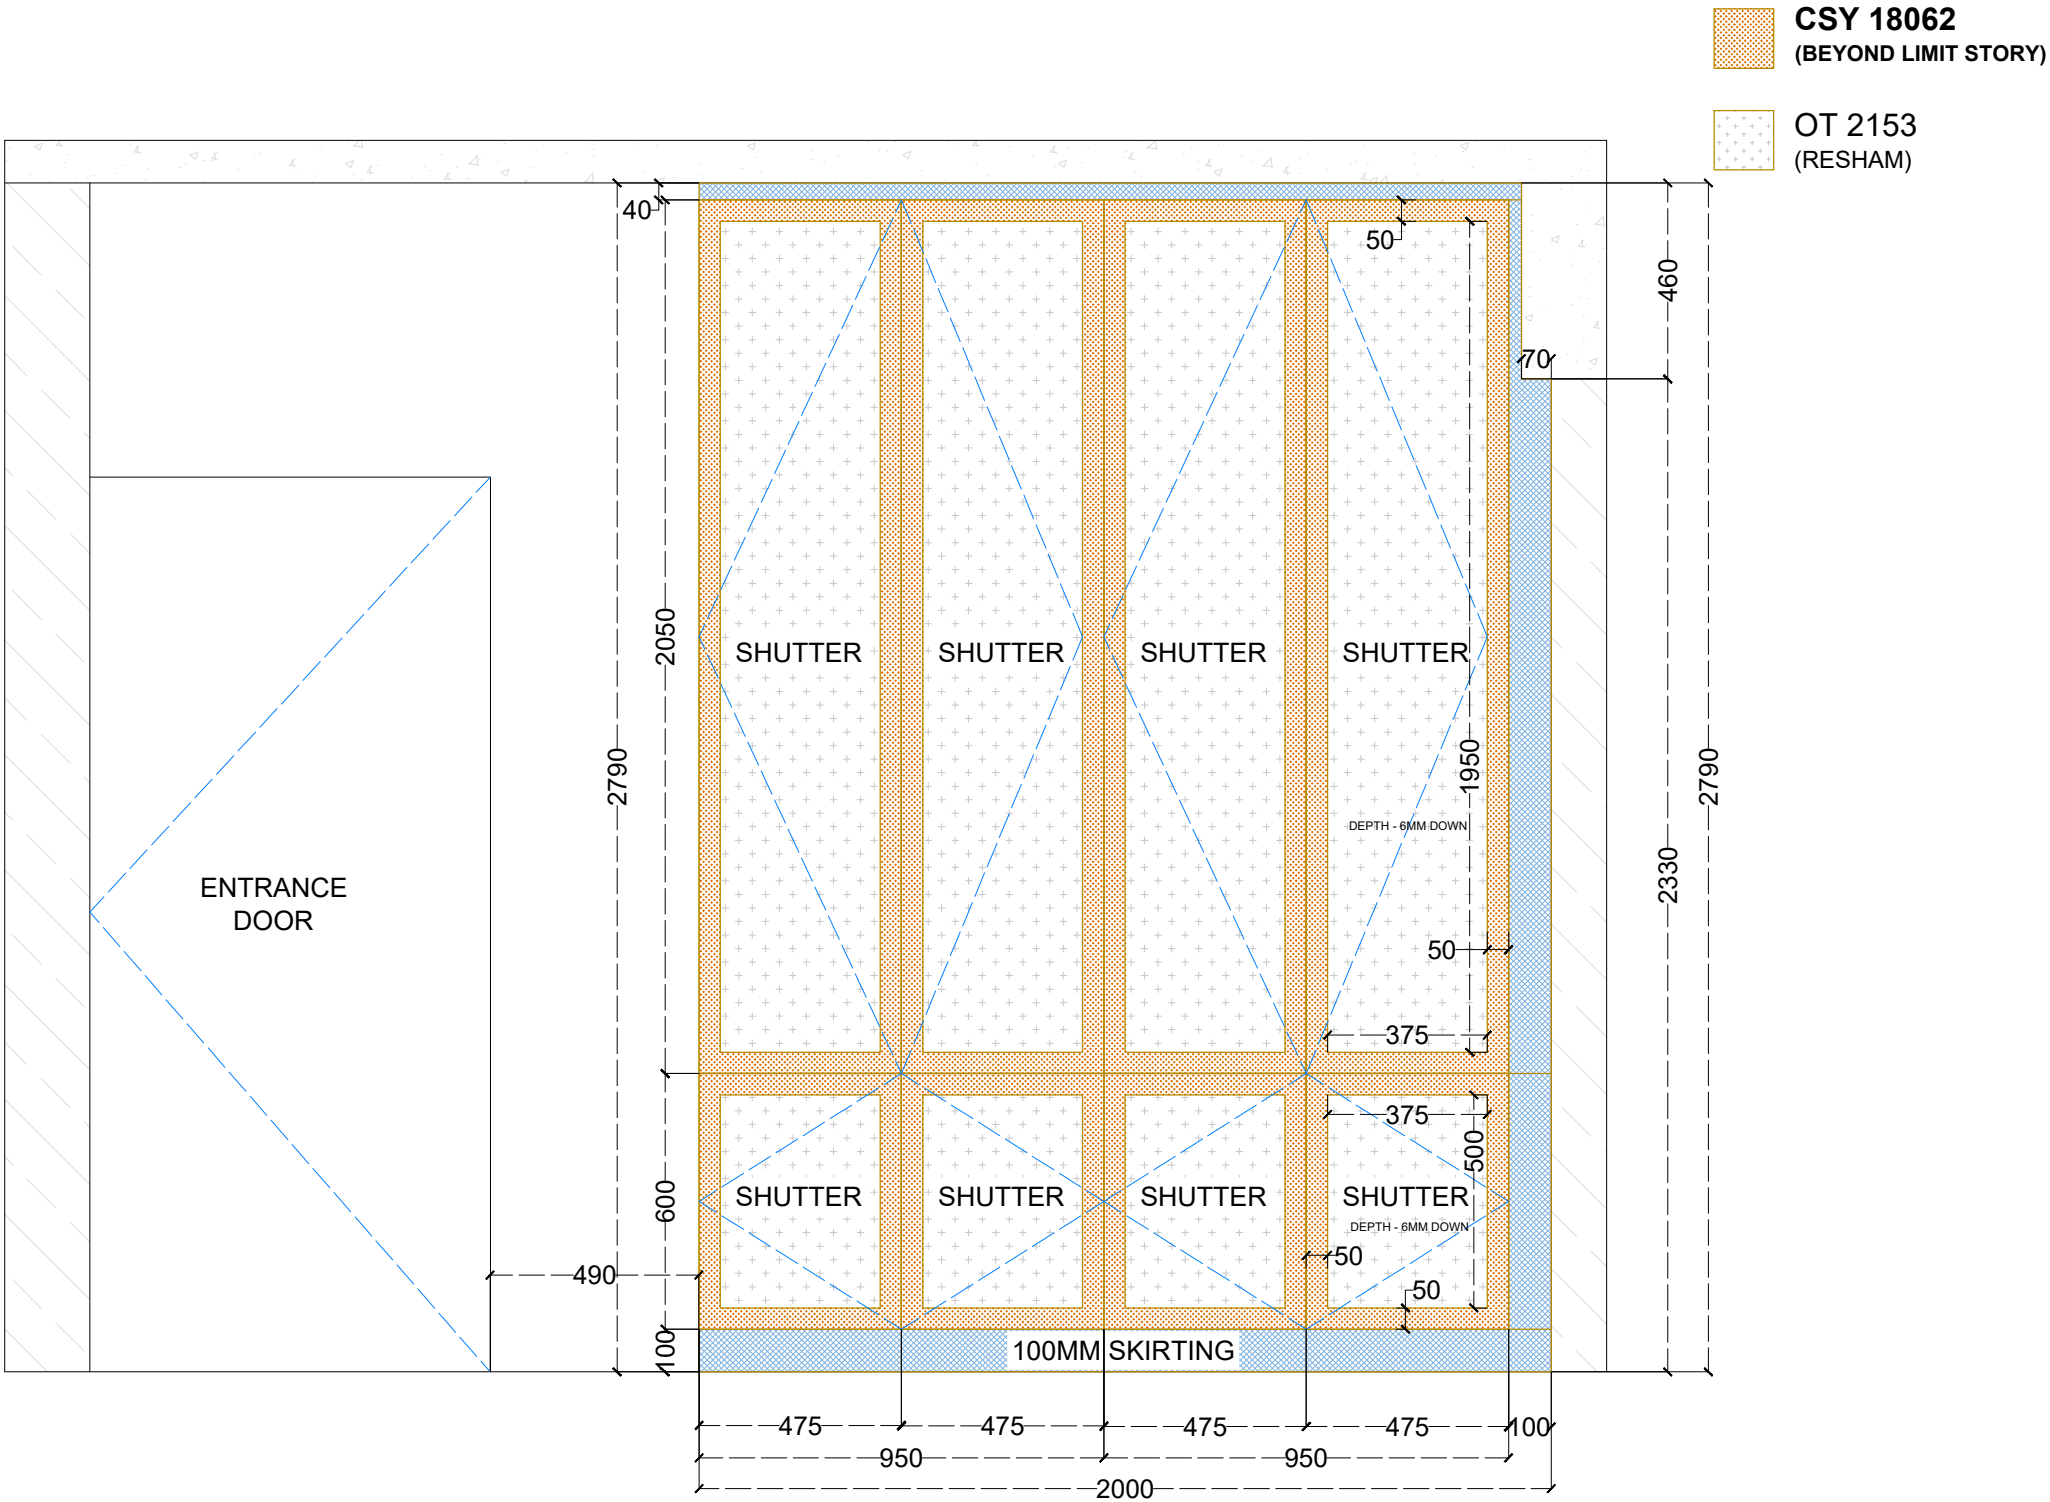


PBR WARDROBE - ELEVATION

TITLE : PBR WARDROBE	DISINED BY : JITHESH K	PRAPOSED INTERIORS FOR : PROJECT : DESIRE TREE CLIENT : Mr AMIT	 LISNO INDIA PRIVATE LIMITED H1/1, 402 Asher Enclave, Naigaon (E) Mumbai, Maharashtra-401208
DATE : 04/05/2026	CHECKED BY :		
PROJECT CODE : M064	HANDOVER DATE :		

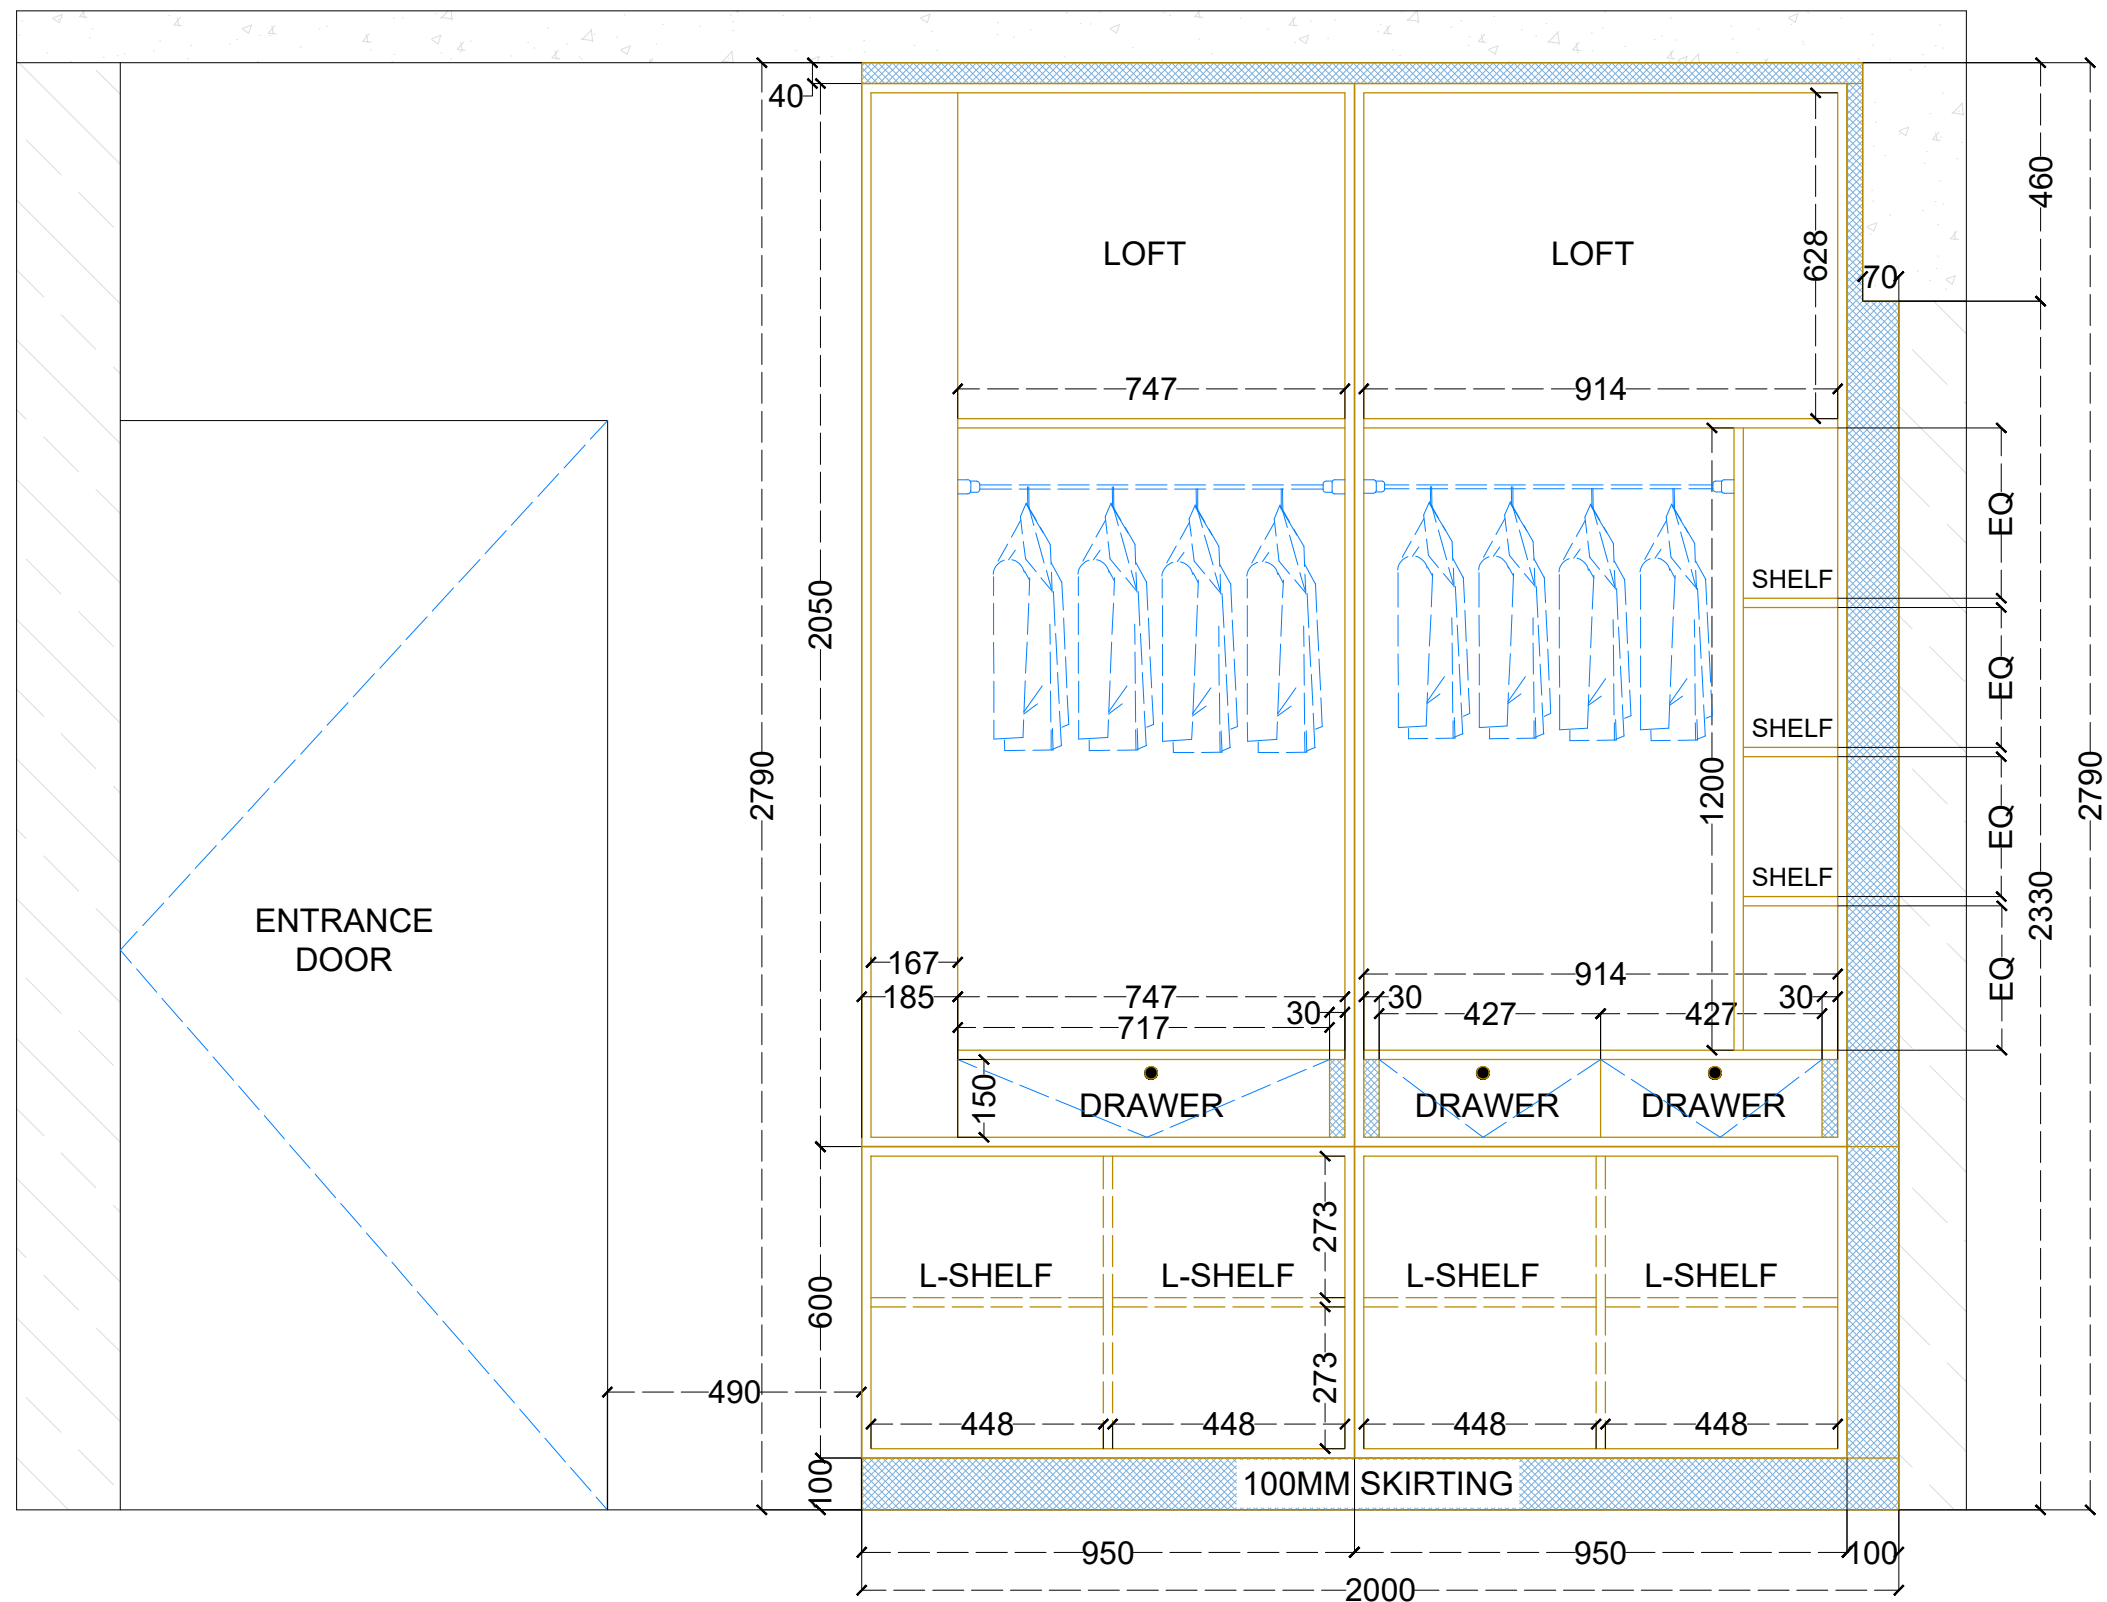


PBR WARDROBE - INTERNAL

TITLE : PBR - WARDROBE	DISINED BY : JITHESH K	PROPOSED INTERIORS FOR : PROJECT : DESIRE TREE CLIENT : Mr AMIT	 LISNO INDIA PRIVATE LIMITED H1/1, 402 Asher Enclave, Naigaon (E) Mumbai, Maharashtra-401208
DATE : 04/05/2026	CHECKED BY :		
PROJECT CODE : M064	HANDOVER DATE :		

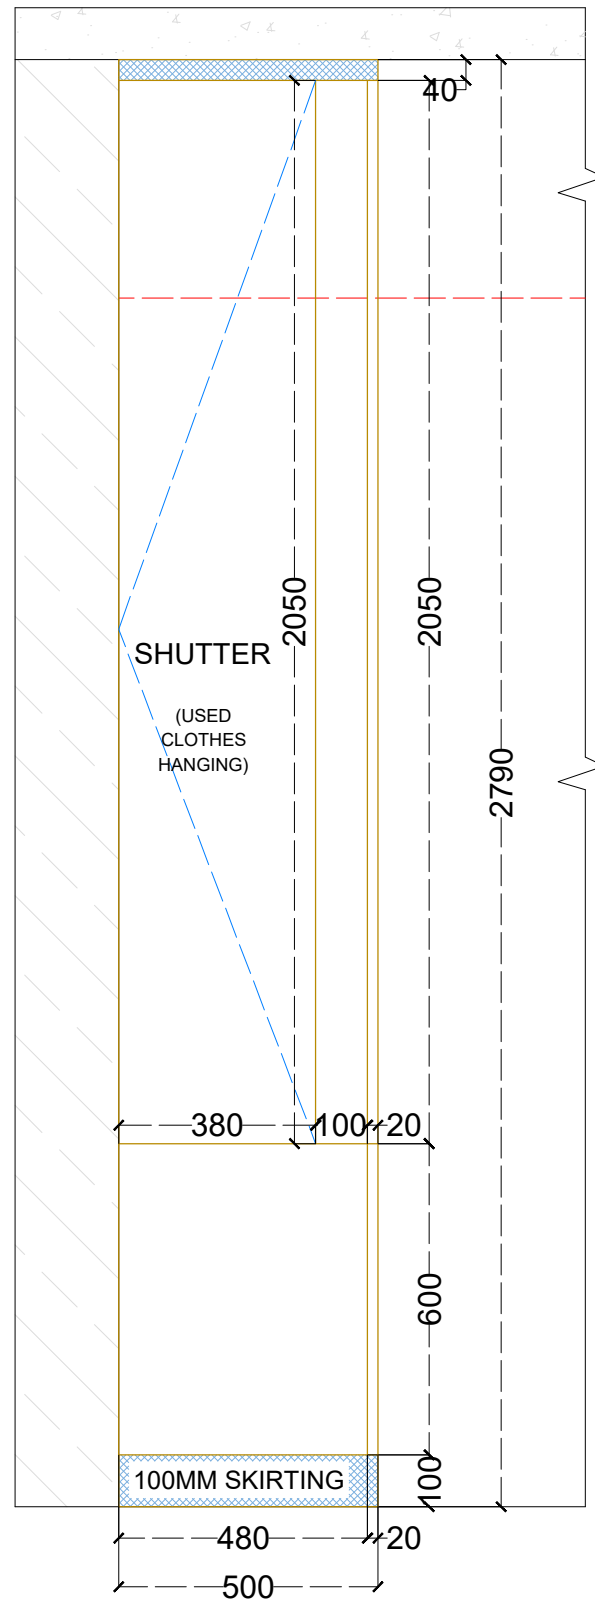


PBR WARDROBE - ELEVATION A-A

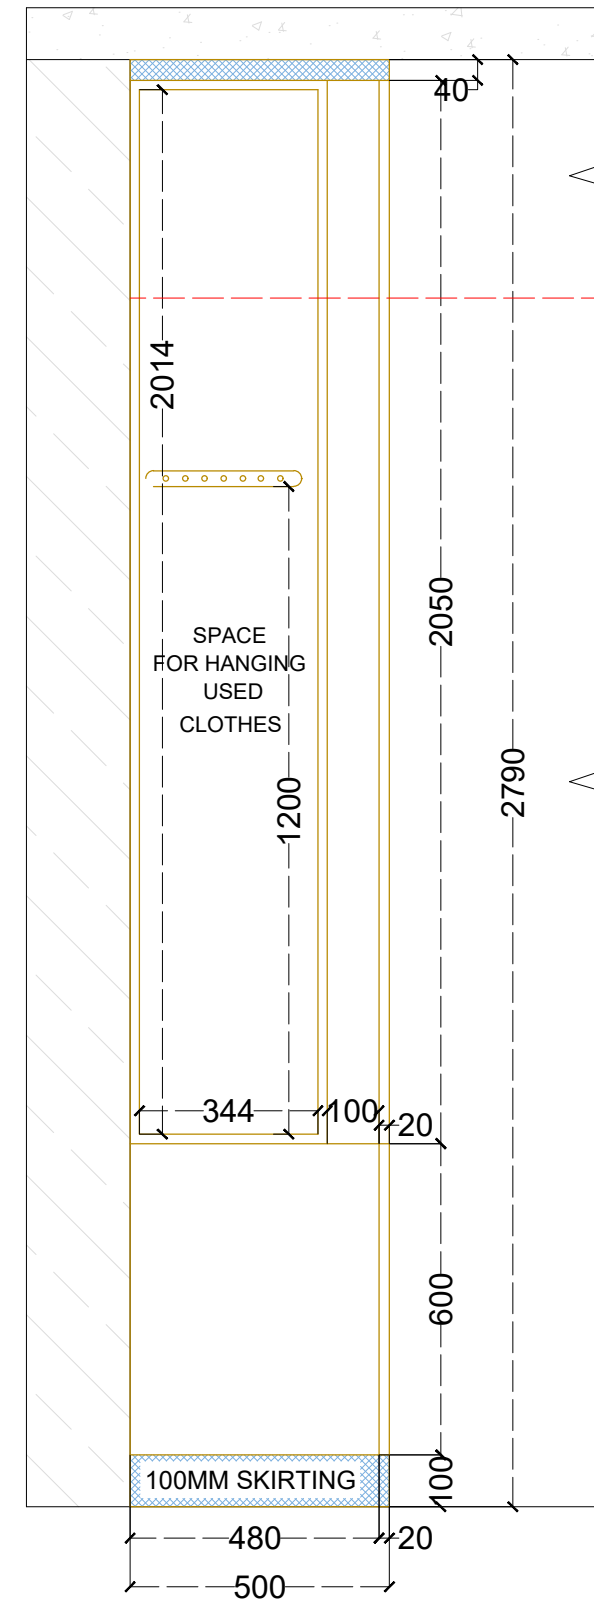


PBR WARDROBE - ELEVATION A-A INTERNAL


TITLE : PBR - WARDROBE	DISIGNED BY : JITHESH K	PROPOSED INTERIORS FOR : PROJECT : DESIRE TREE CLIENT : Mr AMIT	 LISNO INDIA PRIVATE LIMITED H1/1, 402 Asher Enclave, Naigaon (E) Mumbai, Maharashtra-401208
DATE : 04/05/2026	CHECKED BY :		
PROJECT CODE : M064	HANDOVER DATE :		

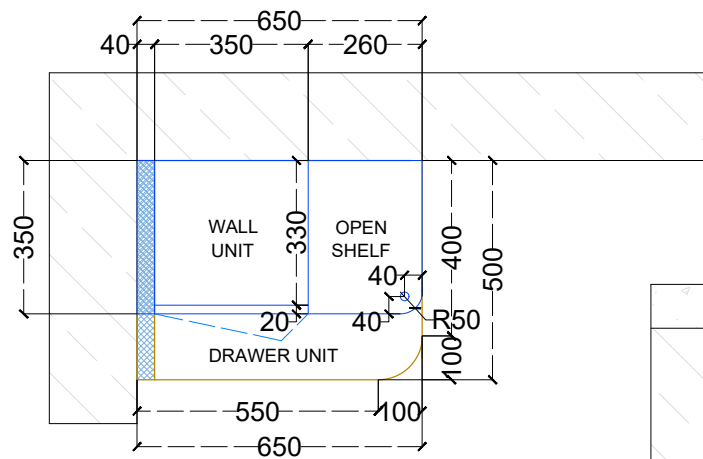

PBR STUDY - PLAN

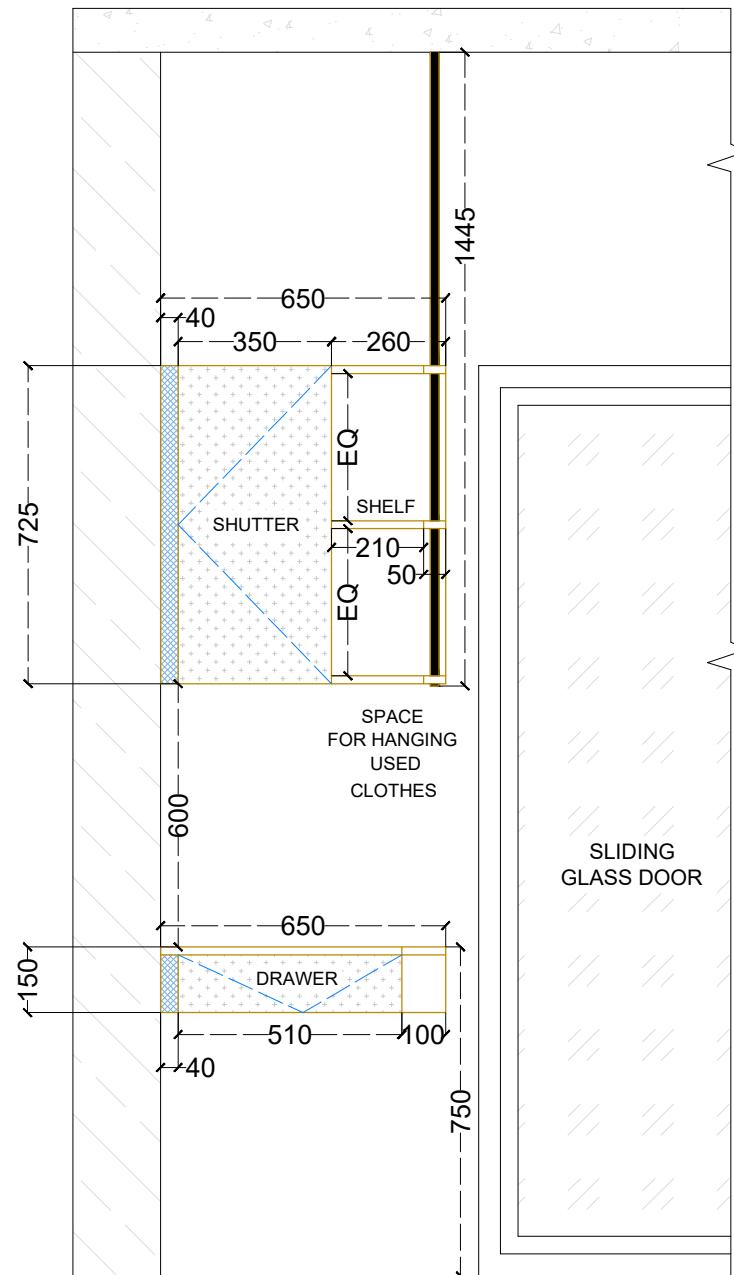

PBR STUDY - ELEVATION

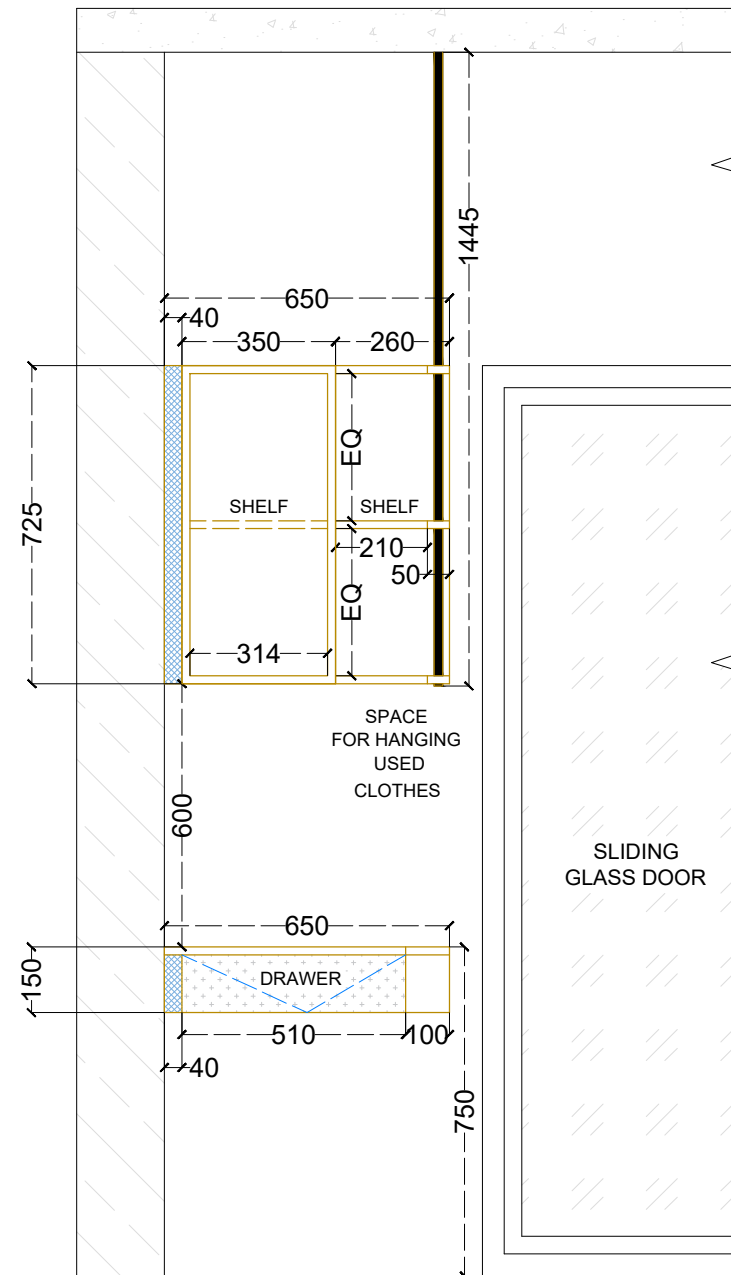

PBR STUDY - INTERNAL

PBR STUDY - DETAIL SHEET

WALL UNIT


CORE MATERIAL	MR ply
EXPOSED SIDE FINISH	CSY 18062 (BEYOND LIMIT STORY)
DRAWER FASCIA FINISH	OT 2153 (RESHAM)
SHUTER FASCIA FINISH	OT 2153 (RESHAM)
INTERNAL FINISH	220 MT/SF (SAFE DECOR)
VISIBLE EDGE BANDING COLOUR	MATCHING WITH LAMINATE
MS ROD	20MM DIA - BLACK

FILLER

CORE MATERIAL	MR ply
FILLER FINISH	CSY 18062 (BEYOND LIMIT STORY)

FILLER & SKIRTING

TOP SHUTTER	HANDLE	4Nos
BOTTOM SHUTTER	KNOB	4Nos
SIDE SHUTTER (USED CLOTHES STORAGE)	PUSH TO OPEN	1Nos

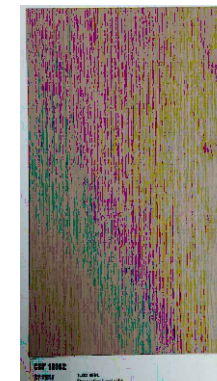

CSY 18062 (BEYOND LIMIT STORY)



OT 2153 (RESHAM)



220 MT/SF (SAFE DECOR)

TITLE : PBR STUDY

DATE : 04/05/2026

PROJECT CODE : M064

DISINED BY : JITHESH K

CHECKED BY :


HANDOVER DATE :

PRAPOSED INTERIORS FOR :

PROJECT : DESIRE TREE
CLIENT : Mr AMIT




LISNO INDIA PRIVATE LIMITED
H1/1, 402 Asher Enclave, Naigaon (E) Mumbai,
Maharashtra-401208

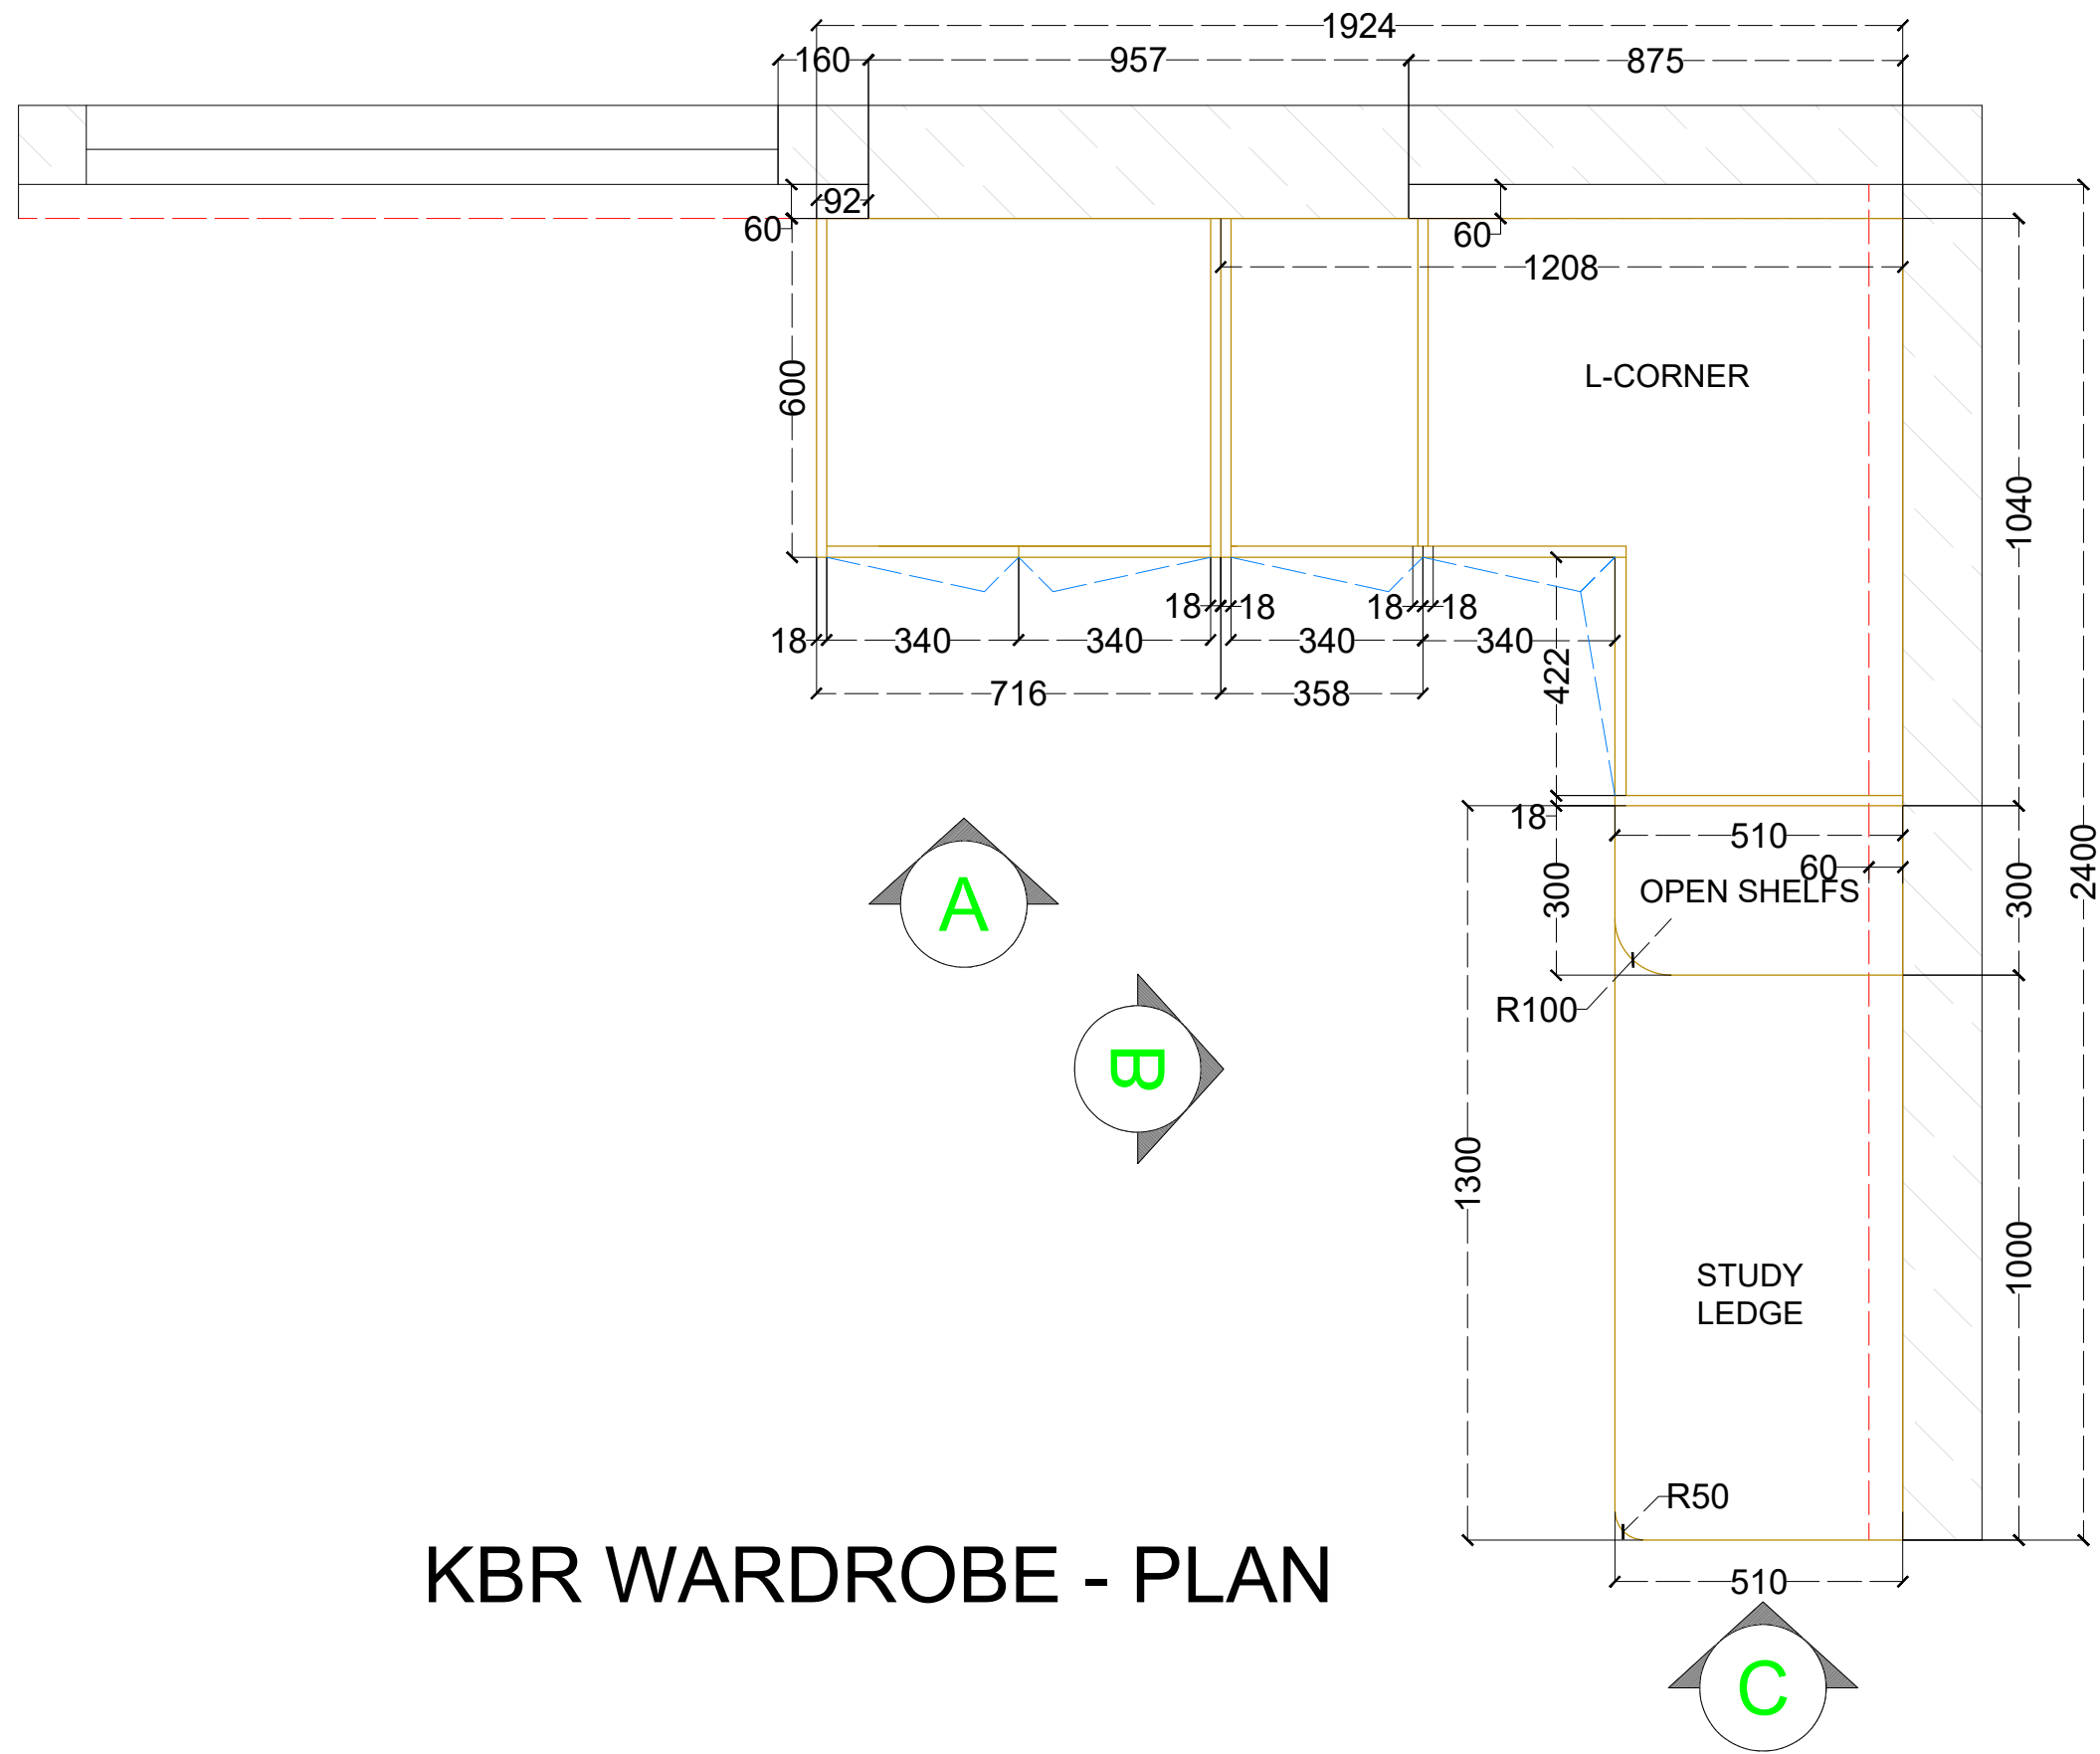

KBR WARDROBE - PLAN

KBR WARDROBE - DETAIL SHEET

TITLE : KBR - WARDROBE	DISINED BY : JITHESH K	PROPOSED INTERIORS FOR : PROJECT : DESIRE TREE CLIENT : Mr AMIT	 LISNO INDIA PRIVATE LIMITED H1/1, 402 Asher Enclave, Naigaon (E) Mumbai, Maharashtra-401208
DATE : 04/05/2026	CHECKED BY :		
PROJECT CODE : M064	HANDOVER DATE :		

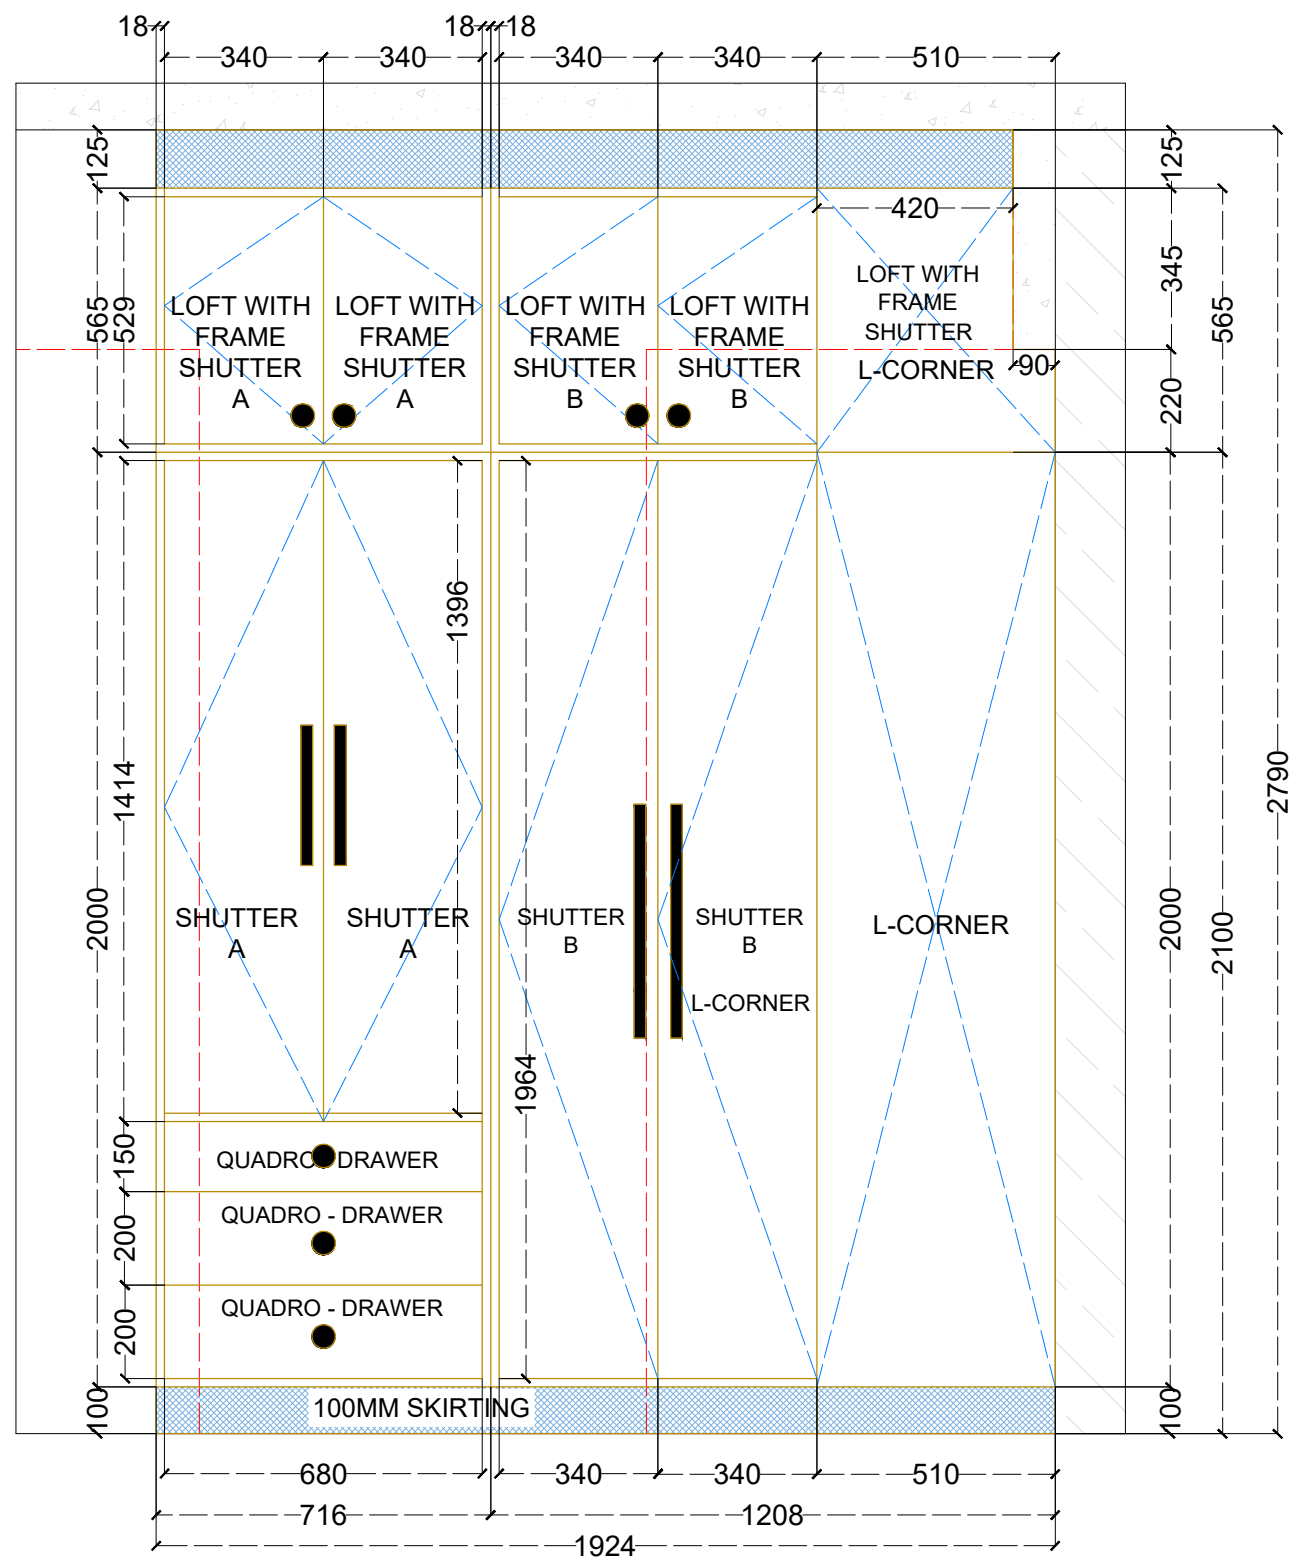

KBR WARDROBE - ELEVATION A

KBR WARDROBE - DETAIL SHEET

WARDROBE UNIT

CORE MATERIAL	MR ply
EXPOSED SIDE FINISH	1088 E (FLUXA)
SHUTER - A FINISH 1	1052 E (FLUXA)
SHUTER - B FINISH 2	DIGI 57 (FLUXA)
QUADRO DRAWER FASCIA FINISH	DIGI 57 (FLUXA)
OPEN SHELF & STORAGE	1088 E (FLUXA)
INTERNAL FINISH	220 MT/SF (SAFE DECOR)
STUDY LEDGE FINISH	1088 E (FLUXA)
VISIBLE EDGE BANDING COLOUR	MATCHING WITH LAMINATE
MS ROD FINISH	16MM DIA - BLACK

FILLER & SKIRTING

CORE MATERIAL	MR ply
SKIRTING FINISH	1088 E (FLUXA)
FILLER FINISH	1088 E (FLUXA)

HANDLE


SHUTTERS	HANDLE	5Nos
QUADRO DRAWERS	KNOB	3Nos
LOFT SHUTTER	KNOB	5Nos
(OPEN SHELF SIDE) STORAGE SHUTTER	PUSH TO OPEN	2Nos




DIGI 57 (FLUXA)



220 MT/SF (SAFE DECOR)

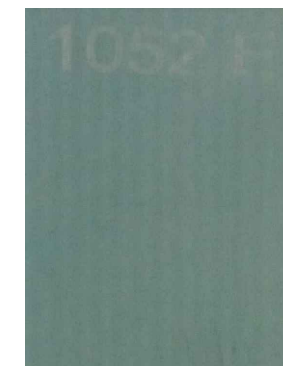

1052 E (FLUXA)

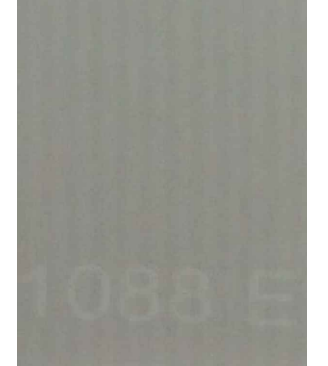

1088 E (FLUXA)

TITLE : KBR WARDROBE

DISINED BY : JITHESH K

PRAPOSED INTERIORS FOR :

DATE : 04/05/2026

CHECKED BY :


PROJECT : DESIRE TREE
CLIENT : Mr AMIT

PROJECT CODE : M064

HANDOVER DATE :



LISNO INDIA PRIVATE LIMITED
H1/1, 402 Asher Enclave, Naigaon (E) Mumbai,
Maharashtra-401208

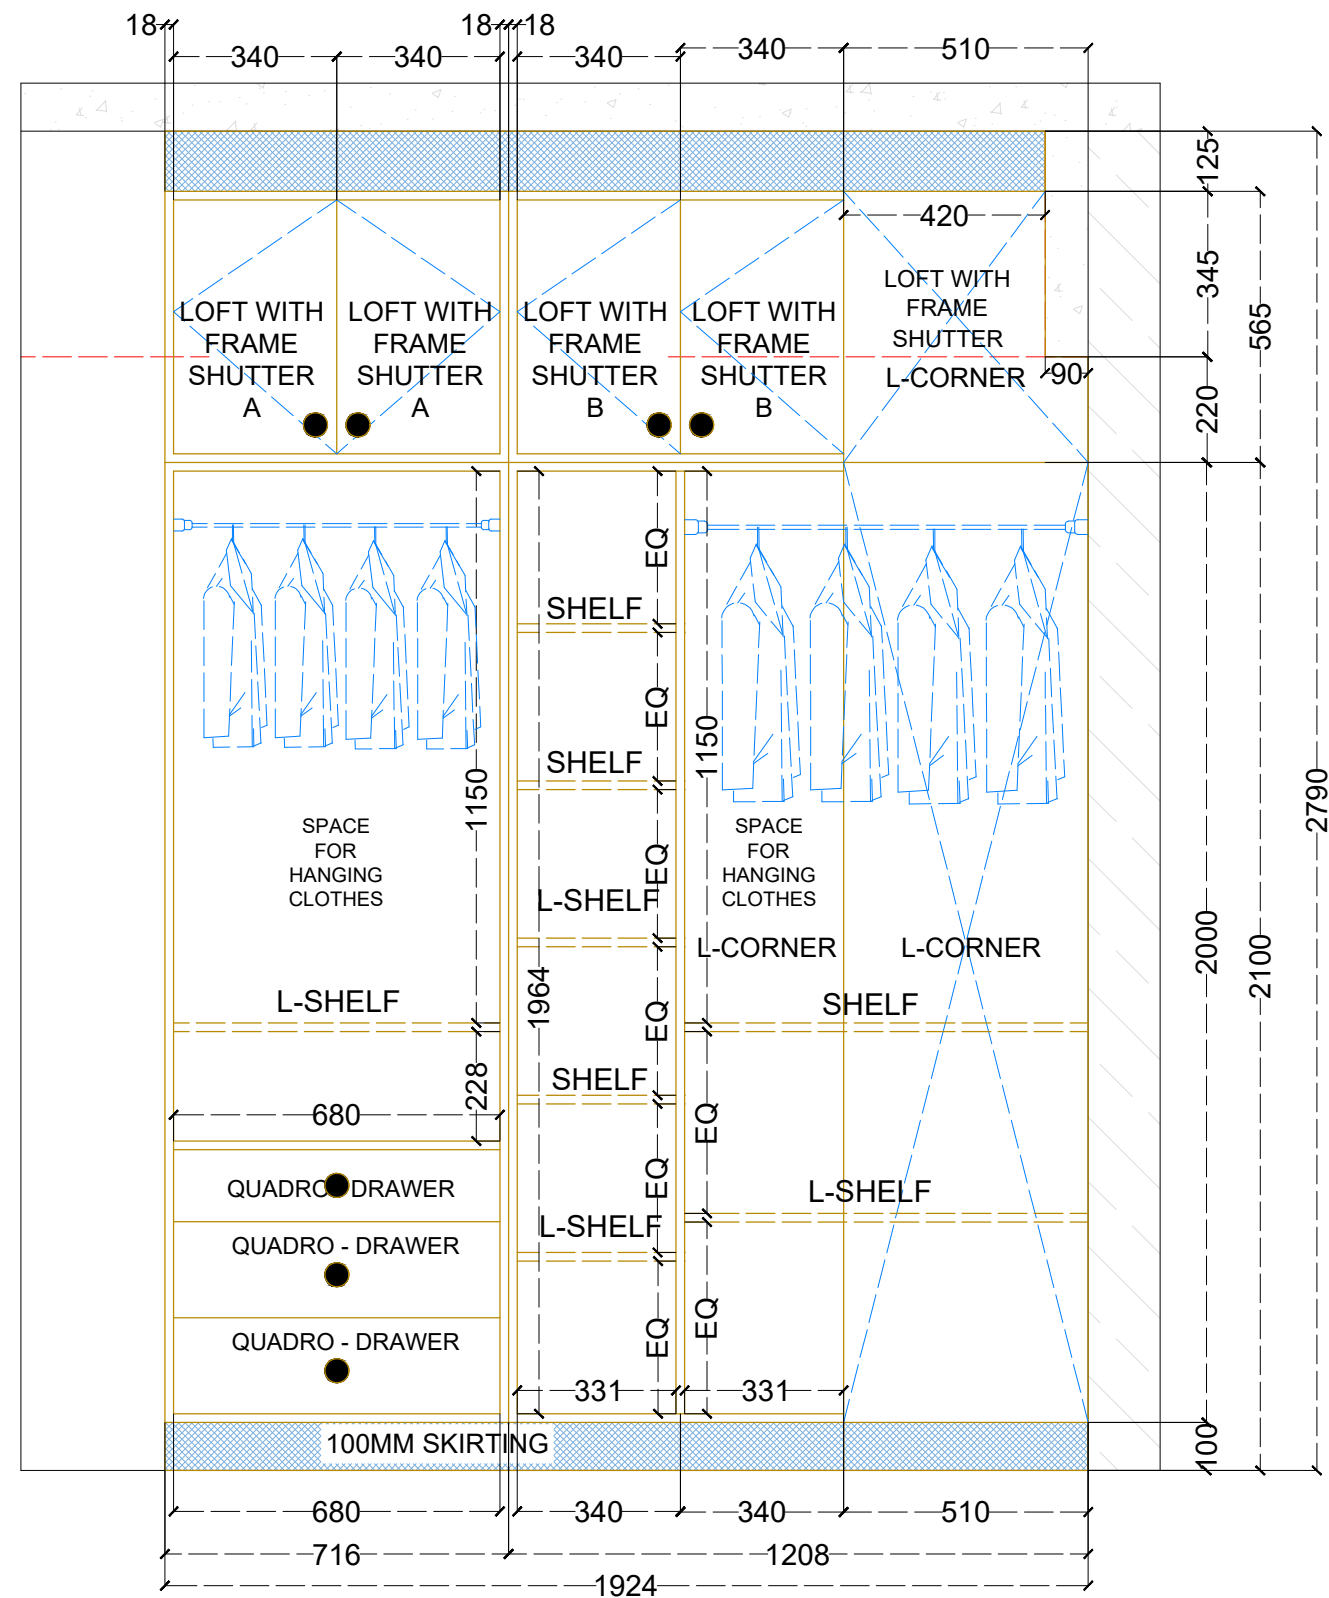

KBR WARDROBE - ELEVATION A INTERNAL

TITLE : KBR - WARDROBE

DISINED BY : JITHESH K

PROPOSED INTERIORS FOR :

DATE : 04/05/2026

CHECKED BY :

PROJECT : DESIRE TREE


PROJECT CODE : M064

HANDOVER DATE :


CLIENT : Mr AMIT



LISNO INDIA PRIVATE LIMITED
H1/1, 402 Asher Enclave, Naigaon (E) Mumbai,
Maharashtra-401208


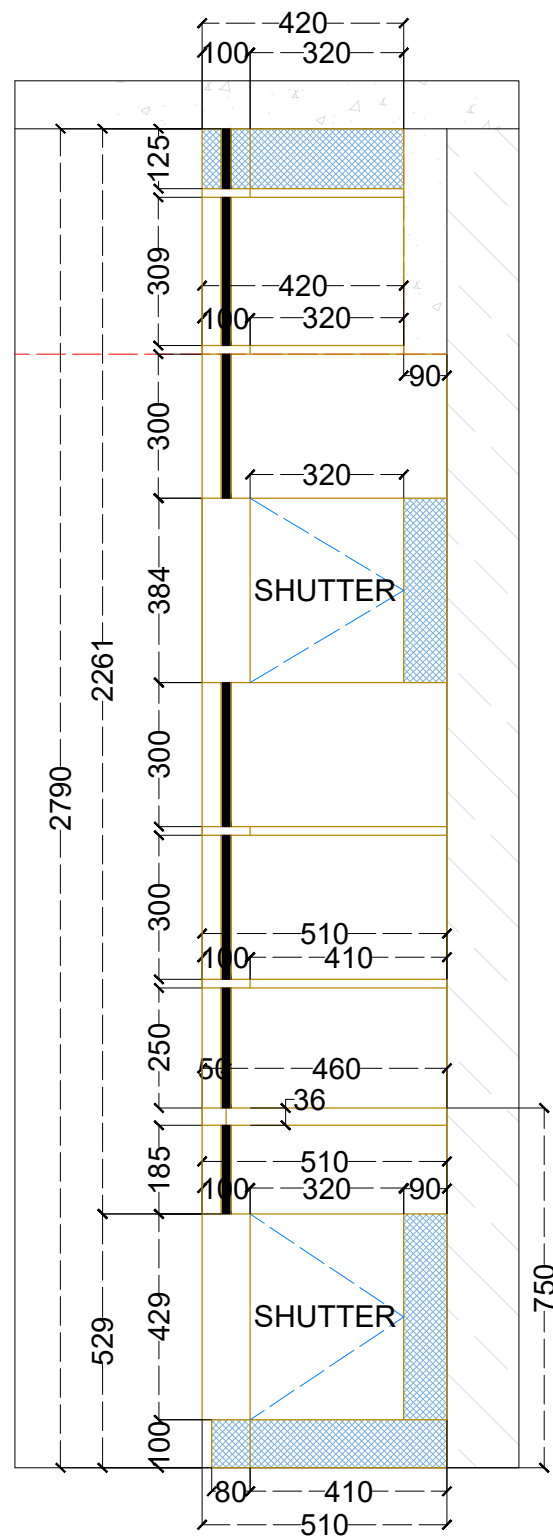


ELEVATION C
(OPEN SHELF & STORAGE)

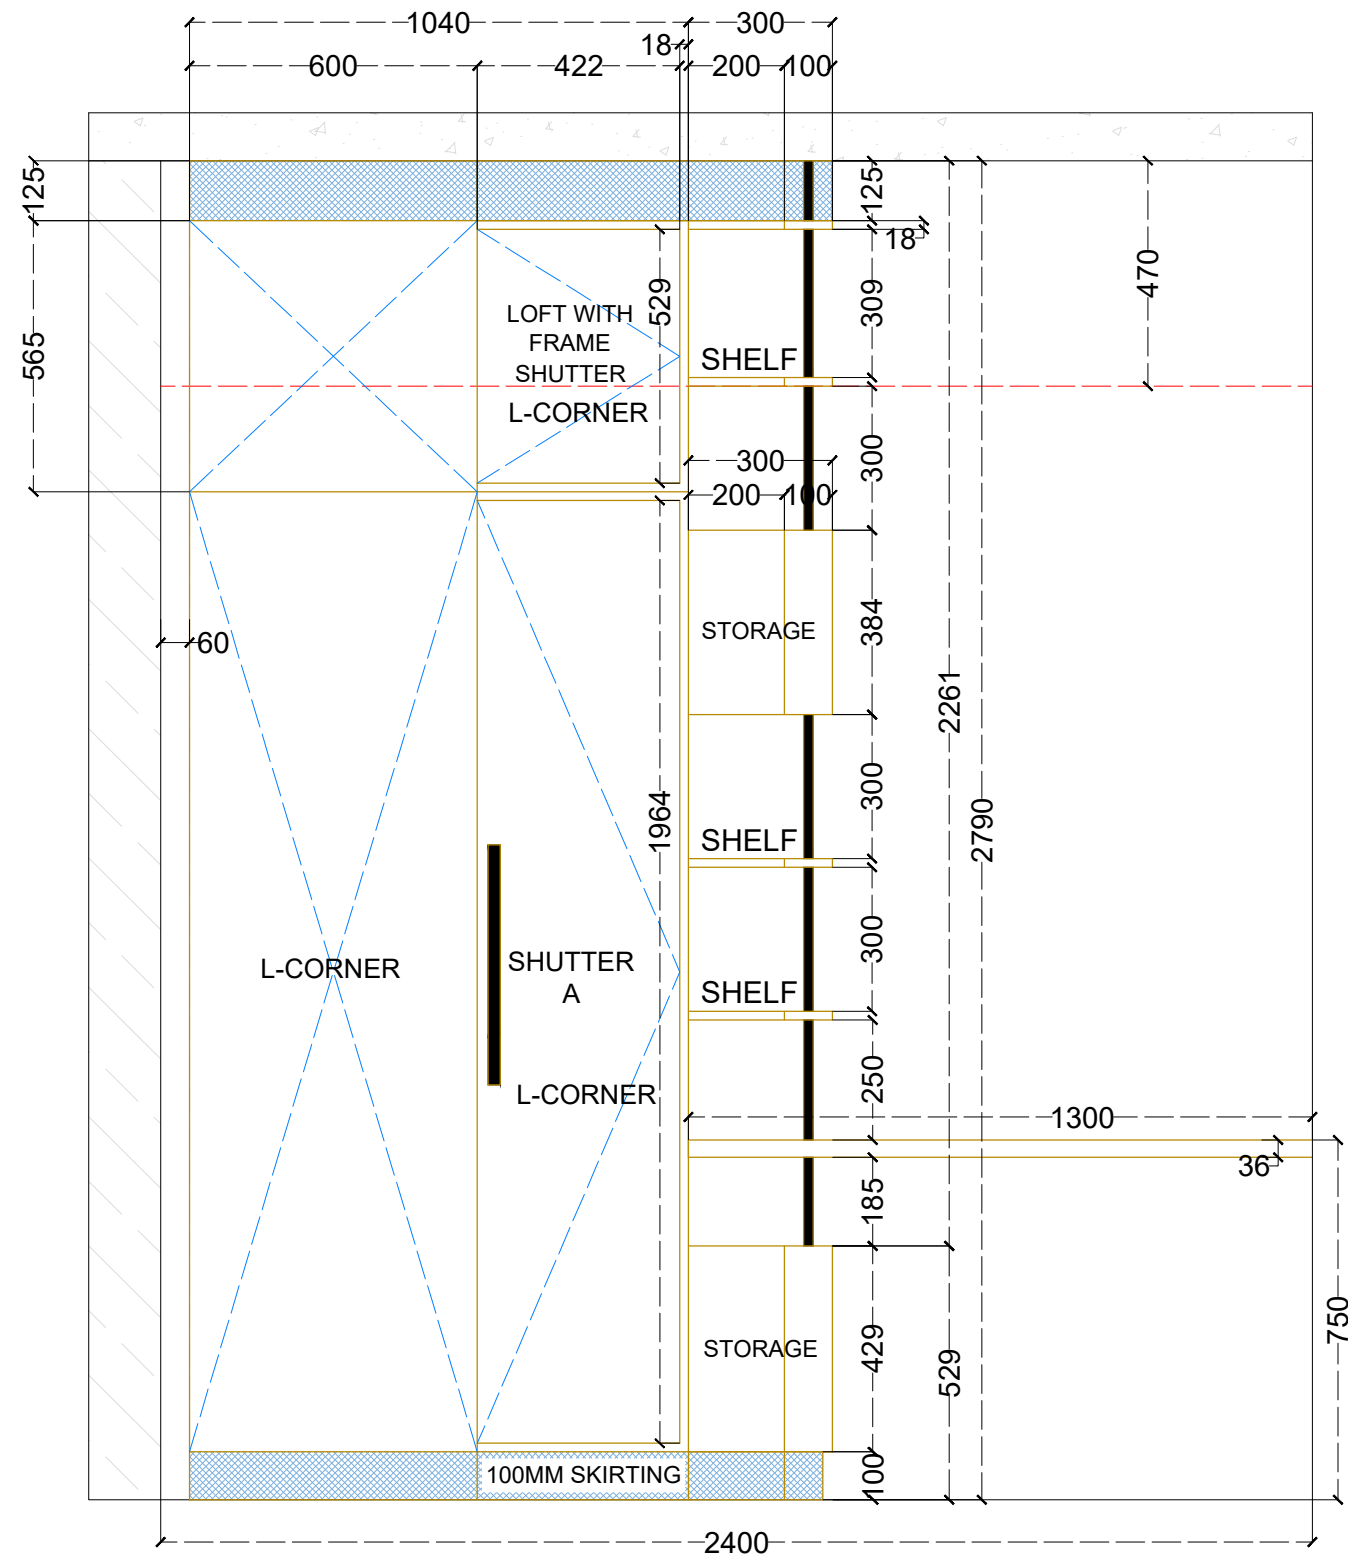


KBR WARDROBE - ELEVATION B

TITLE : KBR - WARDROBE	DISINED BY : JITHESH K	PROPOSED INTERIORS FOR : PROJECT : DESIRE TREE CLIENT : Mr AMIT	 LISNO INDIA PRIVATE LIMITED H1/1, 402 Asher Enclave, Naigaon (E) Mumbai, Maharashtra-401208
DATE : 04/05/2026	CHECKED BY :		
PROJECT CODE : M064	HANDOVER DATE :		

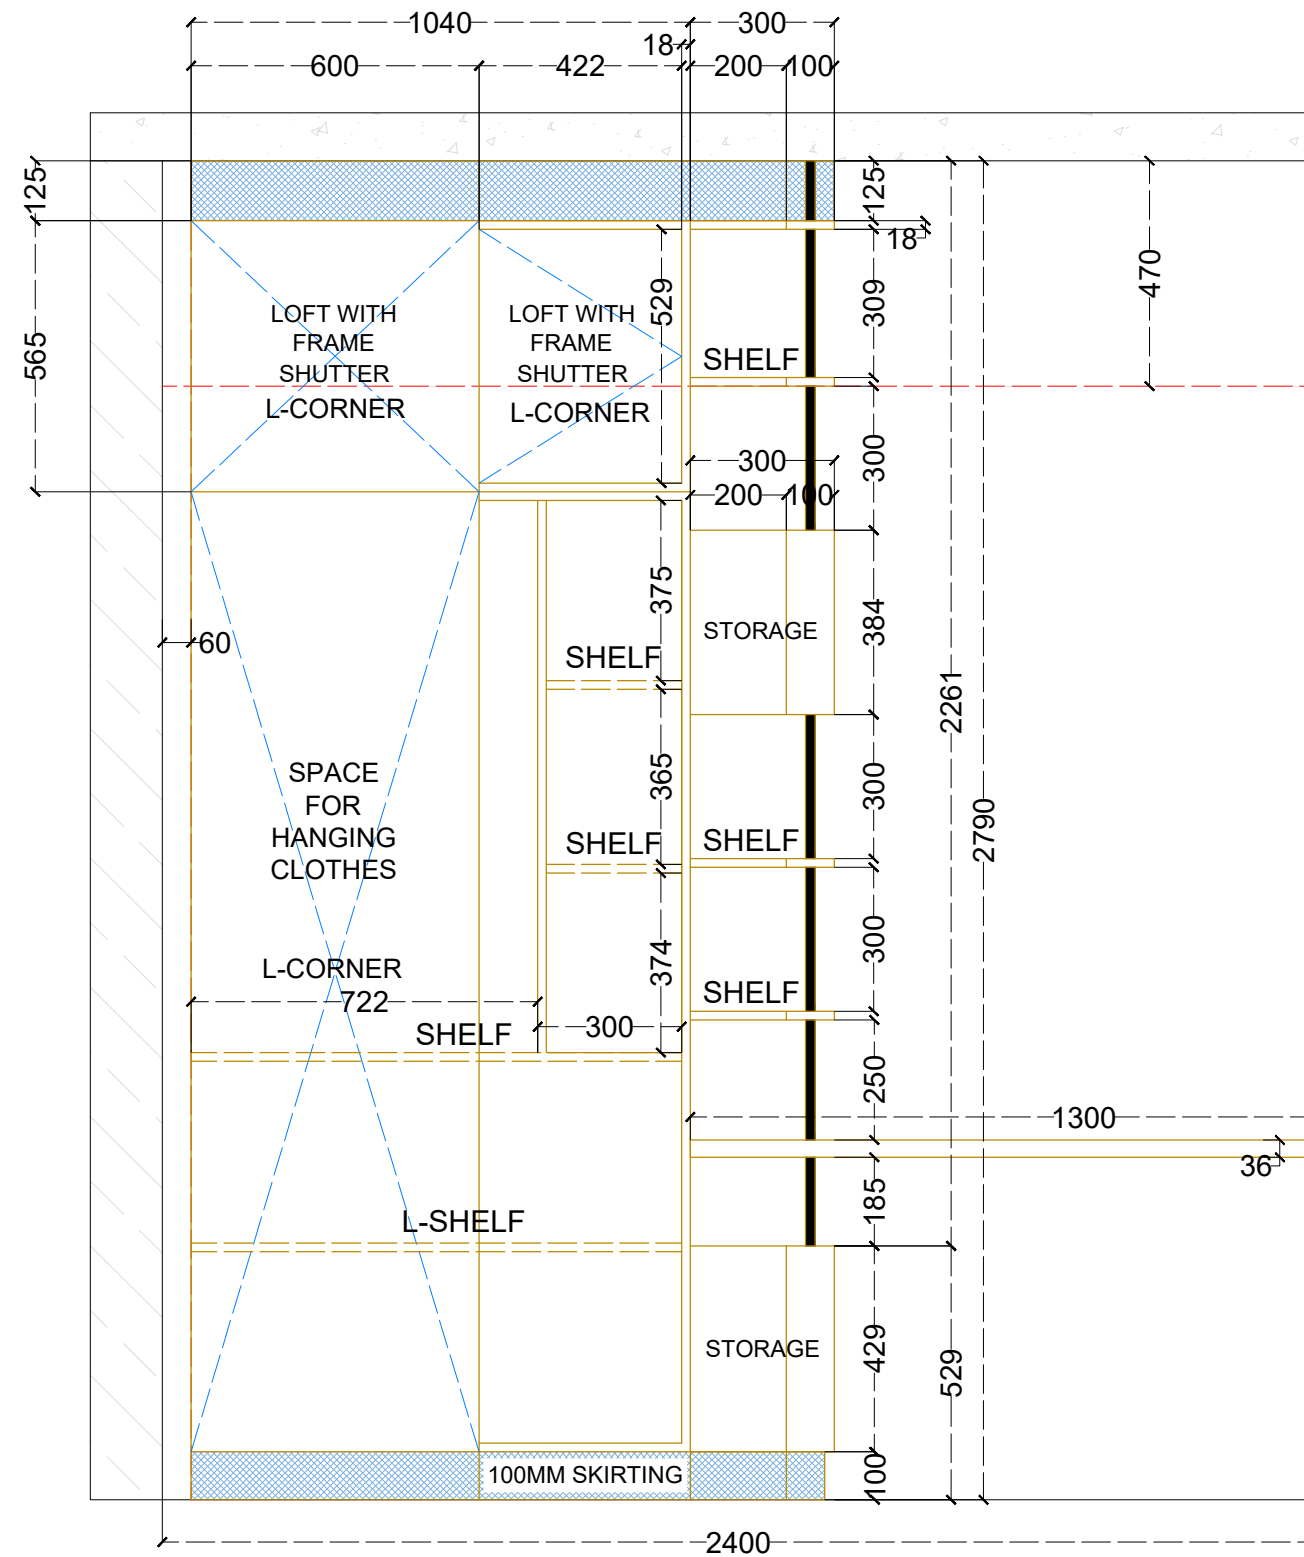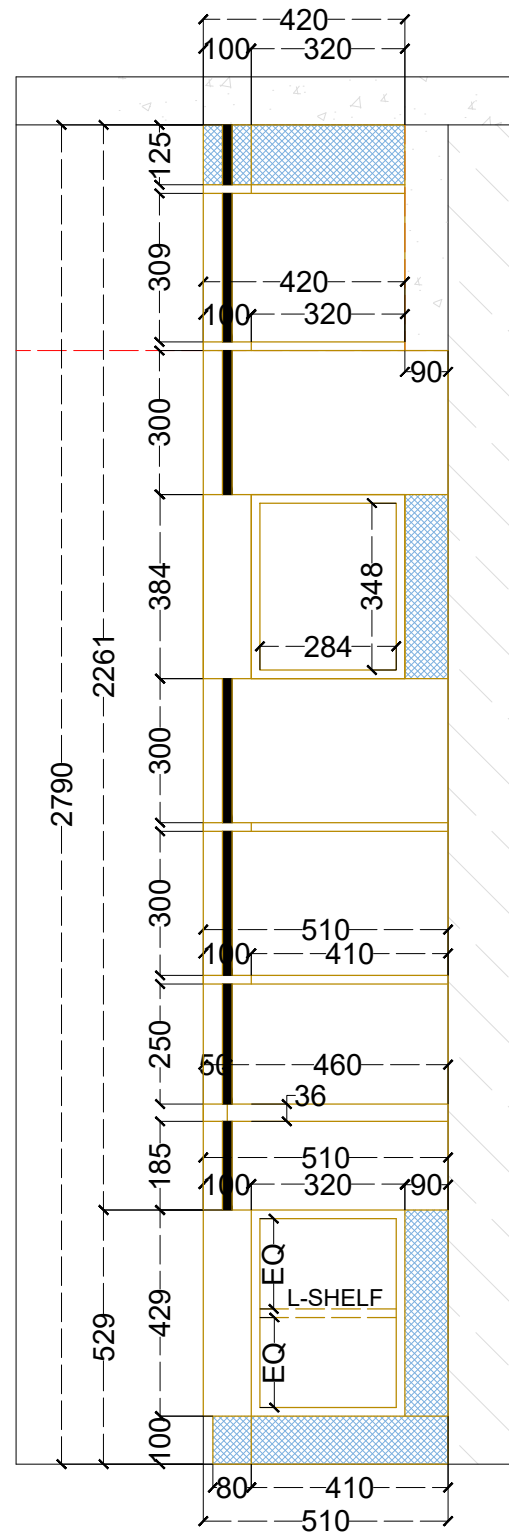


ELEVATION C - INTERNAL KBR WARDROBE - ELEVATION B INTERNAL
(OPEN SHELVES & STORAGE)


TITLE : KBR - WARDROBE	DISINED BY : JITHESH K	PROPOSED INTERIORS FOR : PROJECT : DESIRE TREE CLIENT : Mr AMIT	 LISNO INDIA PRIVATE LIMITED H1/1, 402 Asher Enclave, Naigaon (E) Mumbai, Maharashtra-401208
DATE : 04/05/2026	CHECKED BY :		
PROJECT CODE : M064	HANDOVER DATE :		

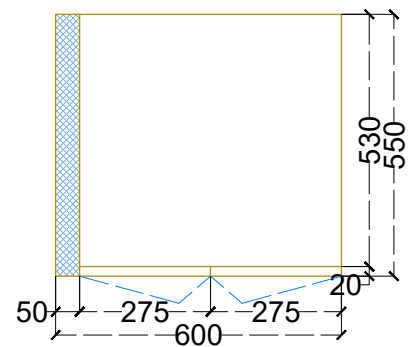


MBR VANITY - PLAN

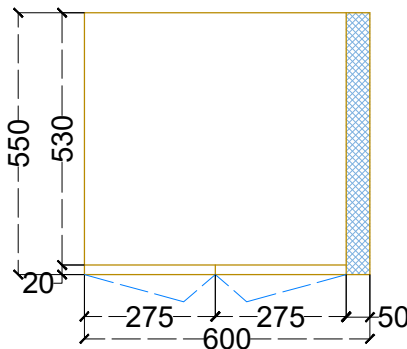

COMMON VANITY - PLAN

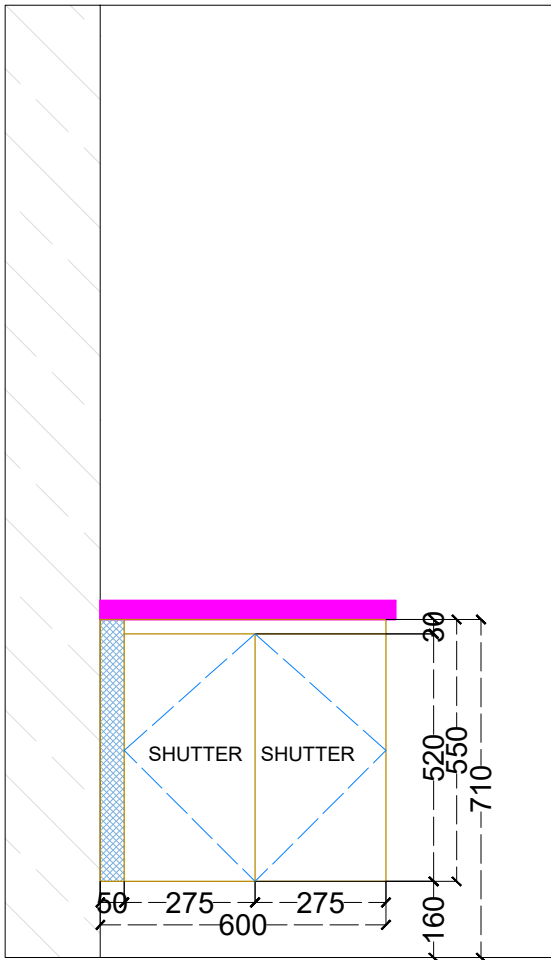

MBR VANITY - ELEVATION

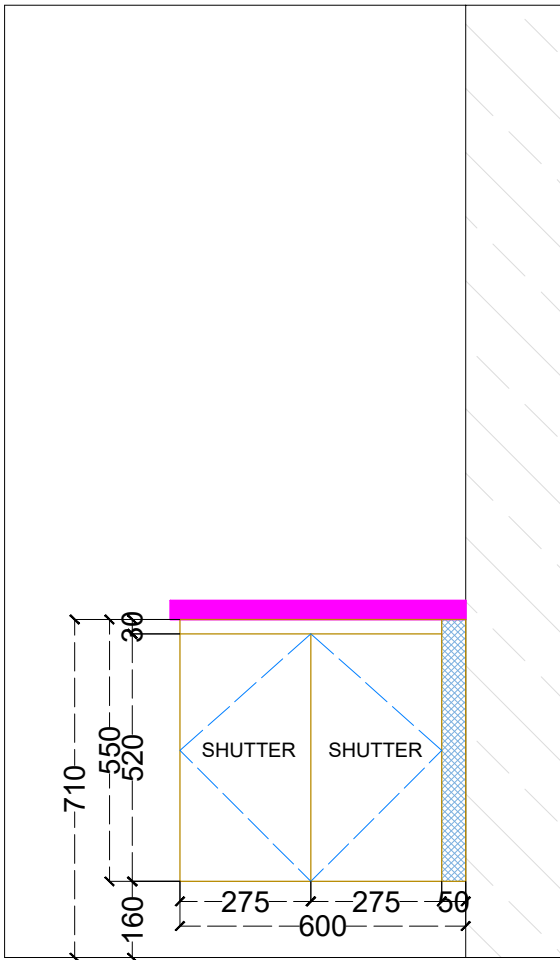

COMMON VANITY - ELEVATION

MBR & COMMON VANITY - DETAIL SHEET

WALL - UNIT


CORE MATERIAL	BWP ply
EXPOSED SIDE FINISH	MR-EL-28 LINEN HEX(ELEGORA)
SHUTER FASCIA FINISH	MR-EL-28 LINEN HEX(ELEGORA)
INTERNAL FINISH	220 MT/SF (SAFE DECOR)
VISIBLE EDGE BANDING COLOUR	MATCHING WITH LAMINATE

FILLER


CORE MATERIAL	BWP ply
SKIRTING FINISH	MR-EL-28 LINEN HEX(ELEGORA)

HANDLE

BASE UNIT SHUTTER	SLANT CUT	2Nos
-------------------	-----------	------

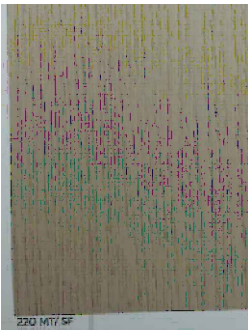

220 MT/SF (SAFE DECOR)

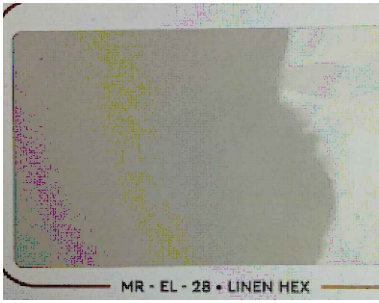

MR-EL-28 LINEN HEX(ELEGORA)

TITLE : MBR & COMMON VANITY

DISINED BY : JITHESH K

PROPOSED INTERIORS FOR :

DATE : 04/05/2026

CHECKED BY :

PROJECT : DESIRE TREE


PROJECT CODE : M064

HANDOVER DATE :


CLIENT : Mr AMIT




LISNO INDIA PRIVATE LIMITED
H1/1, 402 Asher Enclave, Naigaon (E) Mumbai,
Maharashtra-401208

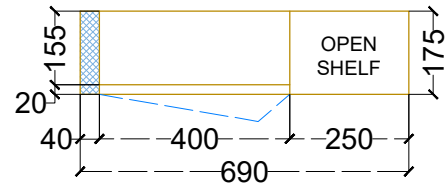


MBR VANITY - WALL UNIT PLAN

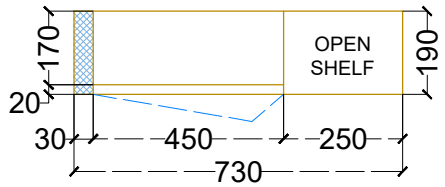

COMMON VANITY - WALL UNIT PLAN

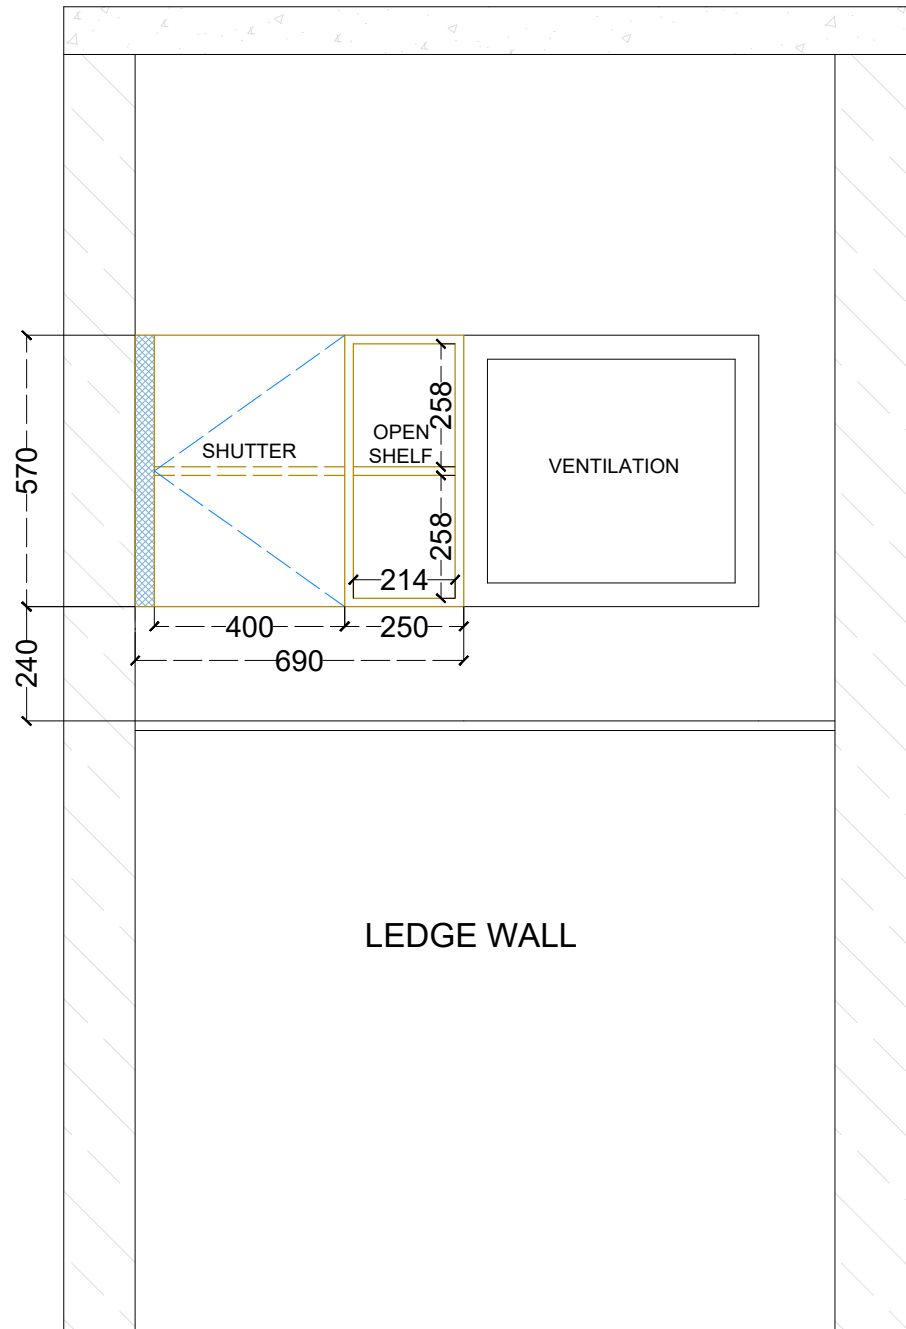

MBR VANITY - WALL UNIT ELEVATION

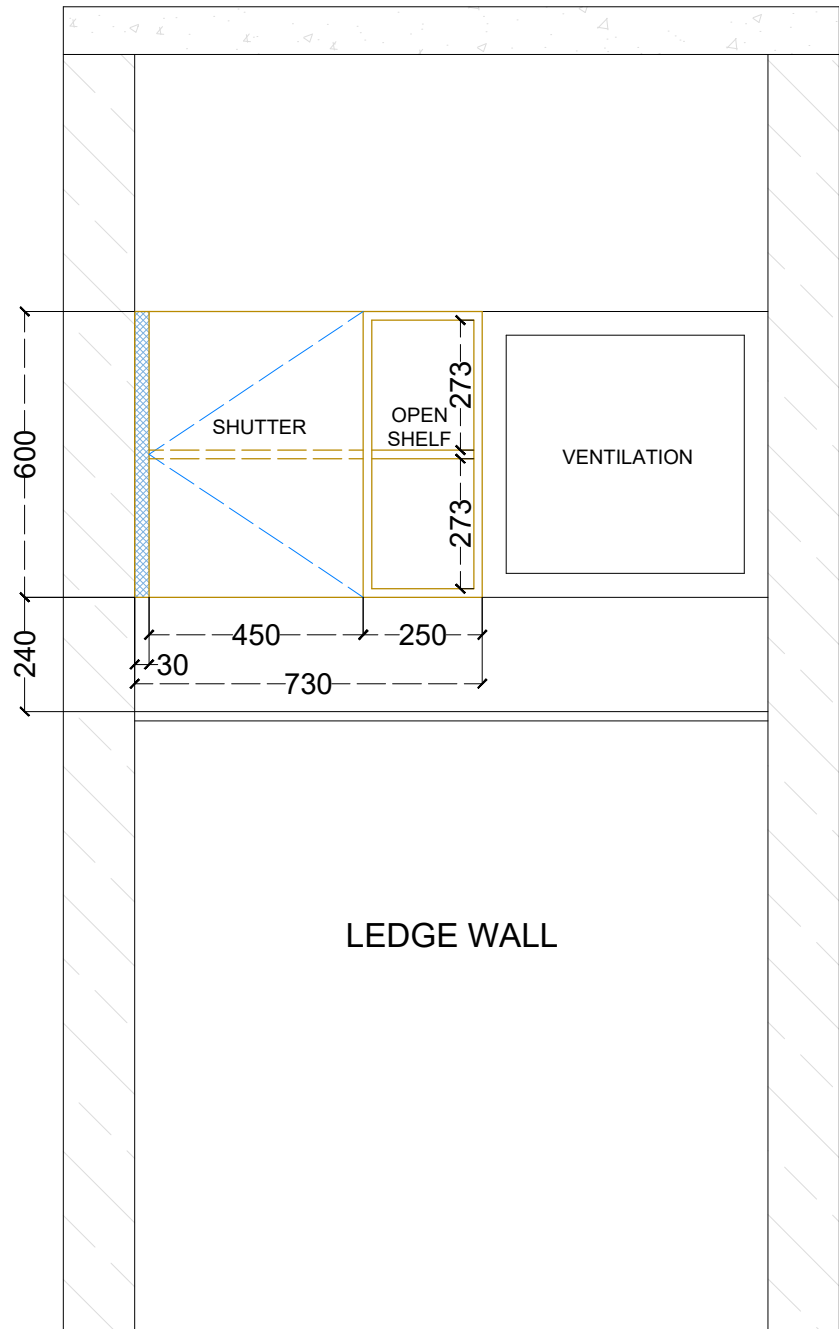

COMMON VANITY - WALL UNIT ELEVATION

MBR & COMMON VANITY - DETAIL SHEET

WALL - UNIT

CORE MATERIAL	MR ply
EXPOSED SIDE FINISH	CSY 18062 (BEYOND LIMIT STORY)
SHUTER FASCIA FINISH	CSY 18062 (BEYOND LIMIT STORY)
INTERNAL FINISH	220 MT/SF (SAFE DECOR)
VISIBLE EDGE BANDING COLOUR	MATCHING WITH LAMINATE

FILLER


CORE MATERIAL	MR ply
FILLER FINISH	CSY 18062 (BEYOND LIMIT STORY)

HANDLE


BASE UNIT SHUTTER	PUSH TO OPEN	2Nos
-------------------	--------------	------



220 MT/SF (SAFE DECOR)

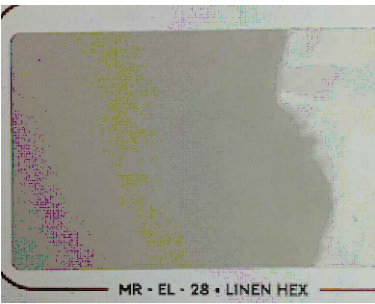

MR-EL-28 LINEN HEX (ELEGORA)

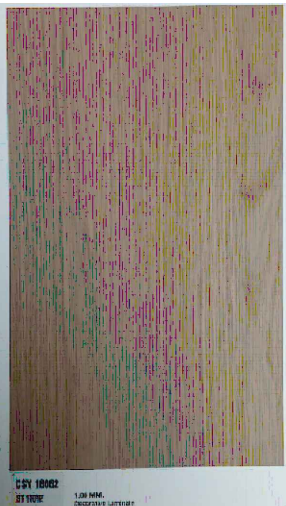

CSY 18062 (BEYOND LIMIT STORY)

TITLE : MBR & COMMON VANITY	DISINED BY : JITHESH K	PROPOSED INTERIORS FOR : PROJECT : DESIRE TREE CLIENT : Mr AMIT	 LISNO INDIA PRIVATE LIMITED H1/1, 402 Asher Enclave, Naigaon (E) Mumbai, Maharashtra-401208
DATE : 04/05/2026	CHECKED BY :		
PROJECT CODE : M064	HANDOVER DATE :		