
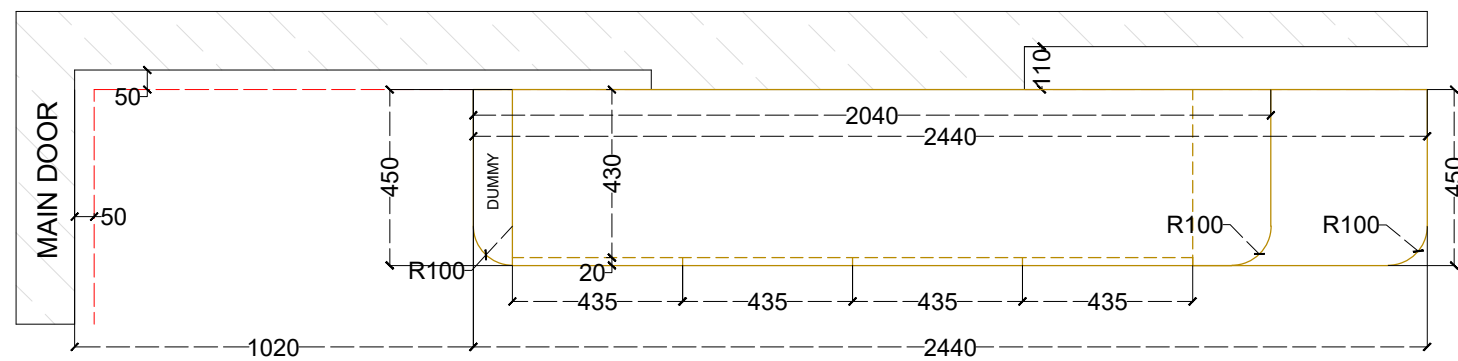
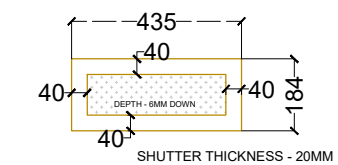
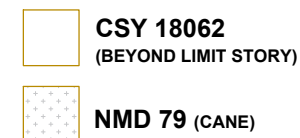


OPEN SHELF DETAIL

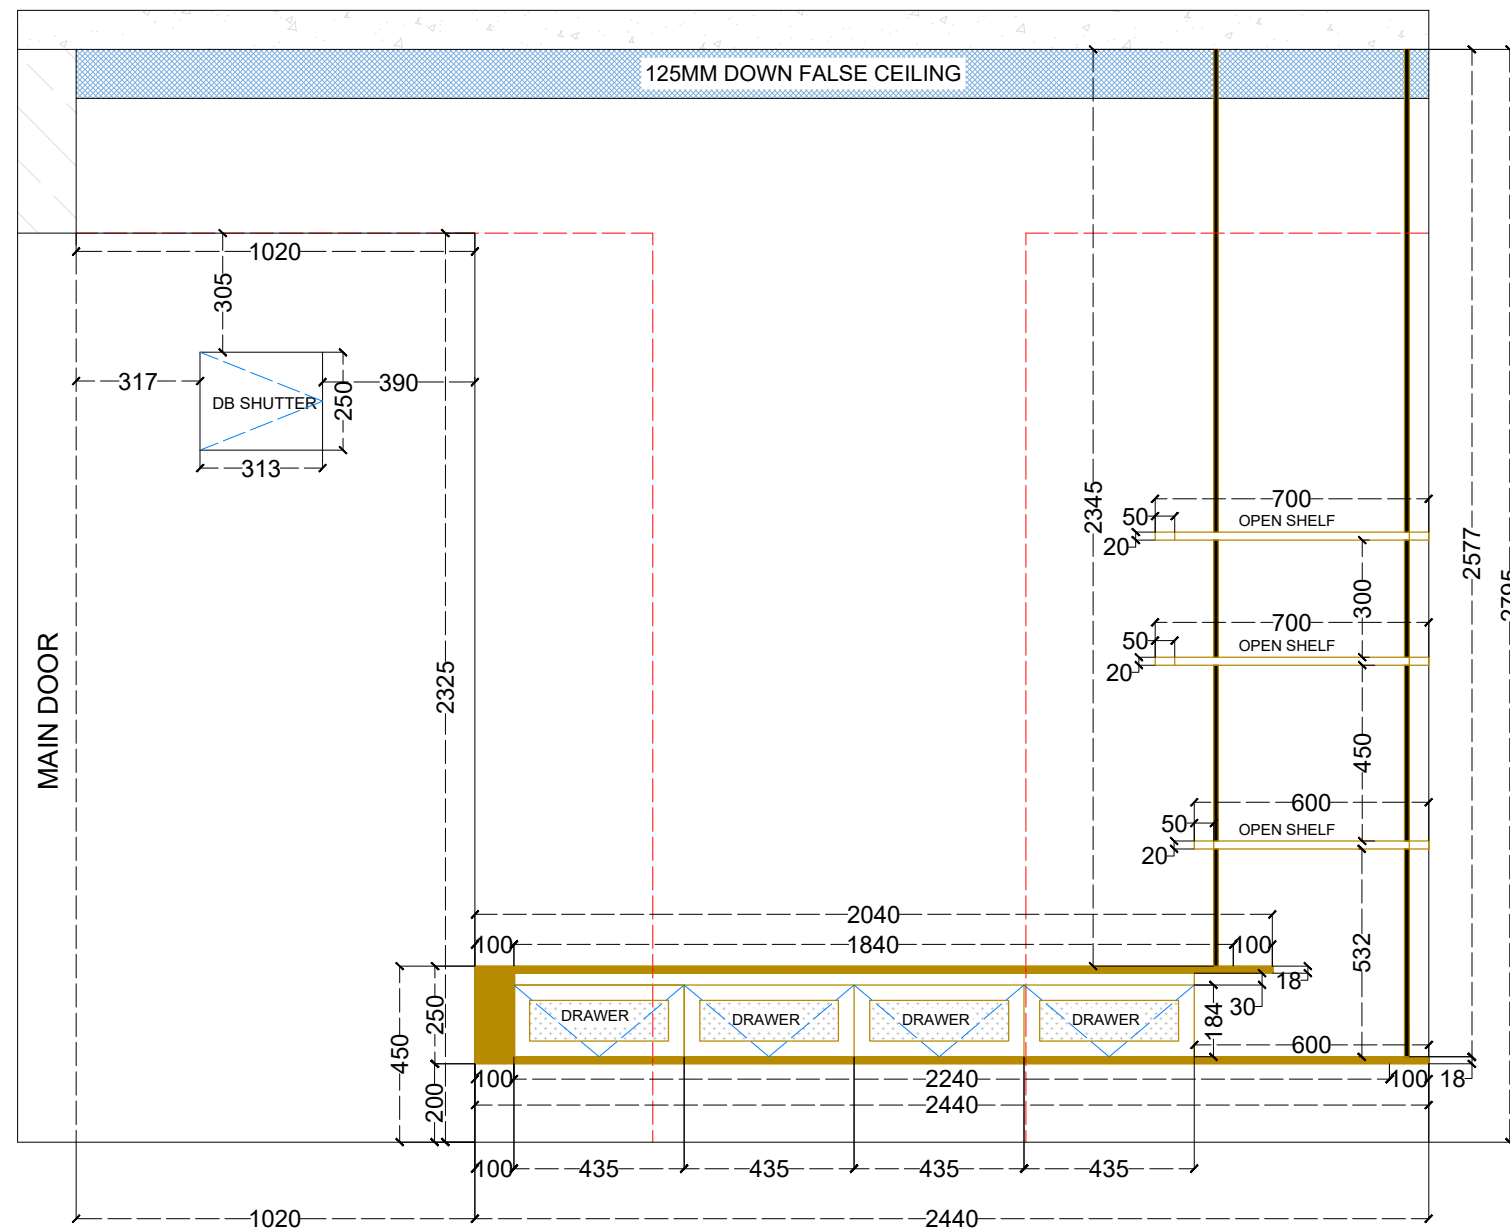

SHUTTER DETAIL (QTY - 4Nos)

TV UNIT - DETAIL SHEET

BASE UNIT

CORE MATERIAL	MR ply
EXPOSED SIDE FINISH	CSY 18062 (BEYOND LIMIT STORY)
SHUTER FASCIA FINISH 1	CSY 18062 (BEYOND LIMIT STORY)
SHUTER FASCIA FINISH 2	NMD 79 (CANE)
INTERNAL FINISH	220 MT/SF (SAFE DECOR)
VISIBLE EDGE BANDING COLOUR	MATCHING WITH LAMINATE

CURVE DUMMY

CORE MATERIAL	MR ply
CURVE DUMMY FINISH	CSY 18062 (BEYOND LIMIT STORY)

HANDLE

DRAWERS	SLANT CUT HANDLE	4Nos
----------------	-------------------------	-------------



CSY 18062 (BEYOND LIMIT STORY)




NMD 79 (CANE)




220 MT/SF (SAFE DECOR)


TITLE : TV UNIT	DISIGNED BY : JITHESH K	PROPOSED INTERIORS FOR : PROJECT : DESIRE TREE CLIENT : Mr AMIT	 LISNO INDIA PRIVATE LIMITED H1/1, 402 Asher Enclave, Naigaon (E) Mumbai, Maharashtra-401208
DATE : 04/05/2026	CHECKED BY :		
PROJECT CODE : M064	HANDOVER DATE :		

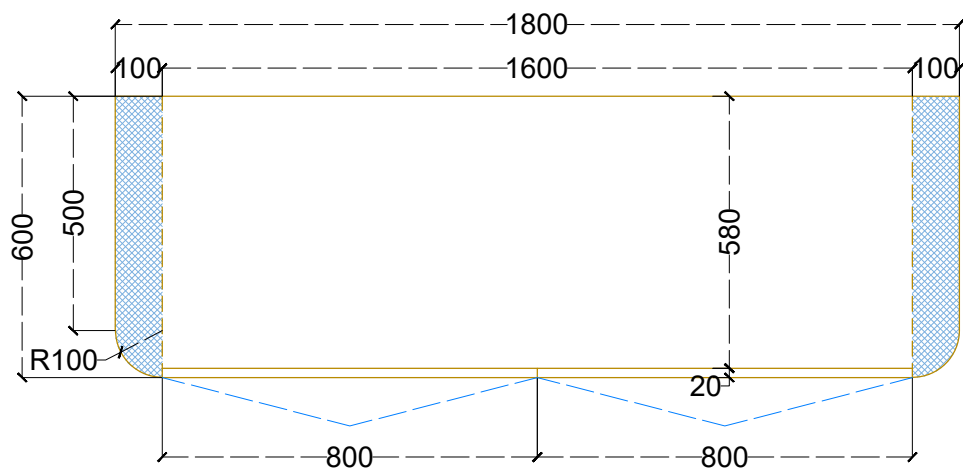


DINING - SEATER WITH STORAGE - PLAN

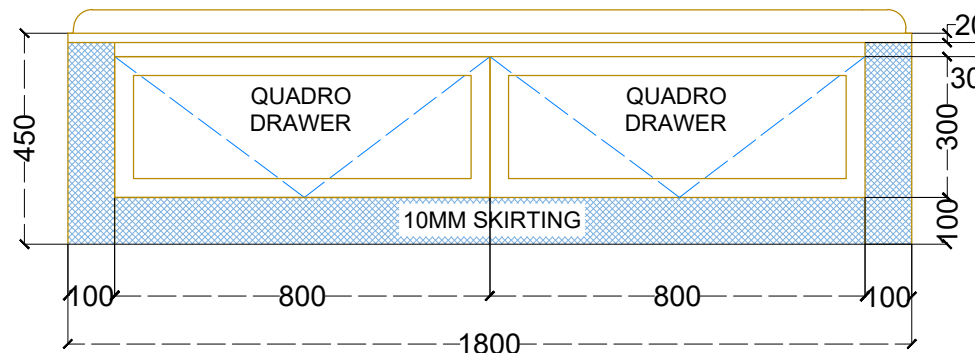

DINING - SEATER WITH STORAGE - ELEVATION

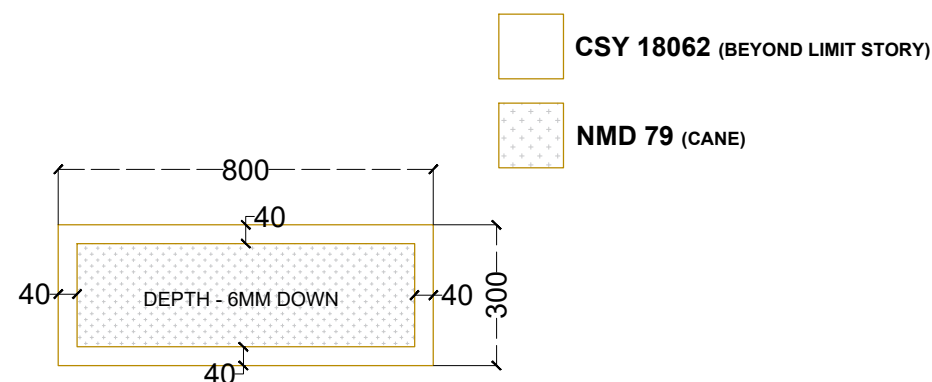

SHUTTER DETAIL (QTY 2Nos)

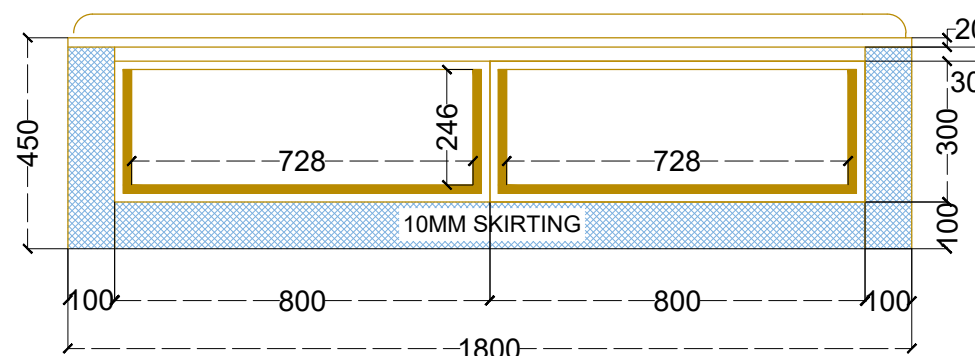

DINING - SEATER WITH STORAGE - INTERNAL

DINING - SEATER UNIT - DETAIL SHEET

BASE UNIT

CORE MATERIAL	MR ply
EXPOSED SIDE FINISH	CSY 18062 (BEYOND LIMIT STORY)
SHUTER FASCIA FINISH 1	CSY 18062 (BEYOND LIMIT STORY)
SHUTER FASCIA FINISH 2	NMD 79 (CANE)
INTERNAL FINISH	220 MT/SF (SAFE DECOR)
VISIBLE EDGE BANDING COLOUR	MATCHING WITH LAMINATE

CURVE DUMMY & SKIRTING

CORE MATERIAL	MR ply
SKIRTING FINISH	CSY 18062 (BEYOND LIMIT STORY)
CURVE DUMMY FINISH	CSY 18062 (BEYOND LIMIT STORY)

HANDLE

BASE DRAWERS	SLANT CUT	2Nos
--------------	-----------	------



CSY 18062 (BEYOND LIMIT STORY)



NMD 79 (CANE)



220 MT/SF (SAFE DECOR)

TITLE : DINING - SEATER UNIT

DISINED BY : JITHESH K

PROPOSED INTERIORS FOR :

DATE : 04/05/2026

CHECKED BY :

PROJECT : DESIRE TREE

PROJECT CODE : M064

HANDOVER DATE :

CLIENT : Mr AMIT



LISNO INDIA PRIVATE LIMITED
H1/1, 402 Asher Enclave, Naigaon (E) Mumbai,
Maharashtra-401208

PUJA UNIT - DETAIL SHEET

BASE UNIT

CORE MATERIAL	MR ply
EXPOSED SIDE FINISH	CSY 18062 (BEYOND LIMIT STORY)
SHUTER FASCIA FINISH 1	CSY 18062 (BEYOND LIMIT STORY)
SHUTER FASCIA FINISH 2	OT 2153 (RESHAM)
INTERNAL FINISH	220 MT/SF (SAFE DECOR)
VISIBLE EDGE BANDING COLOUR	MATCHING WITH LAMINATE

FILLER & SKIRTING

CORE MATERIAL	MR ply
SKIRTING FINISH	CSY 18062 (BEYOND LIMIT STORY)
FILLER FINISH	CSY 18062 (BEYOND LIMIT STORY)

HANDLES

BASE UNIT SHUTTERS	SLANT CUT	3Nos
--------------------	-----------	------




CSY 18062 (BEYOND LIMIT STORY)




OT 2153 (RESHAM)




220 MT/SF (SAFE DECOR)

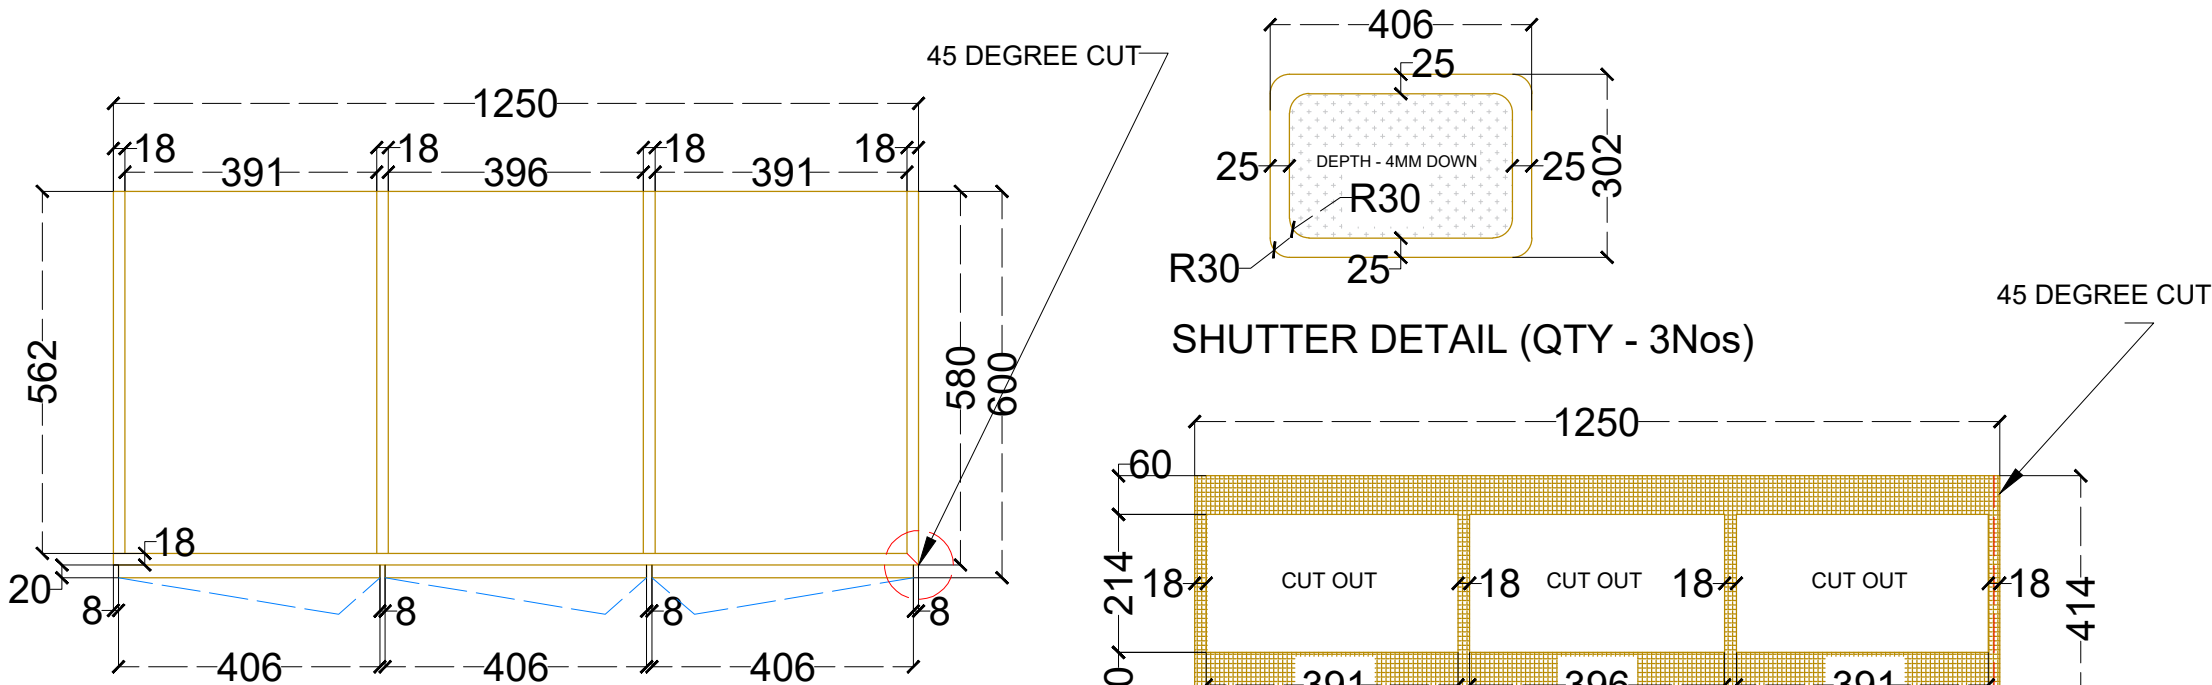


POOJA UNIT - PLAN

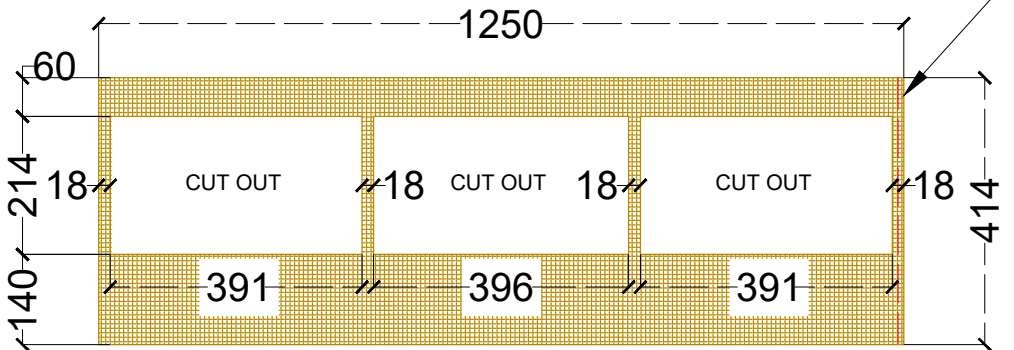

CARCASS FRONT PANEL DETAIL
(18MM)

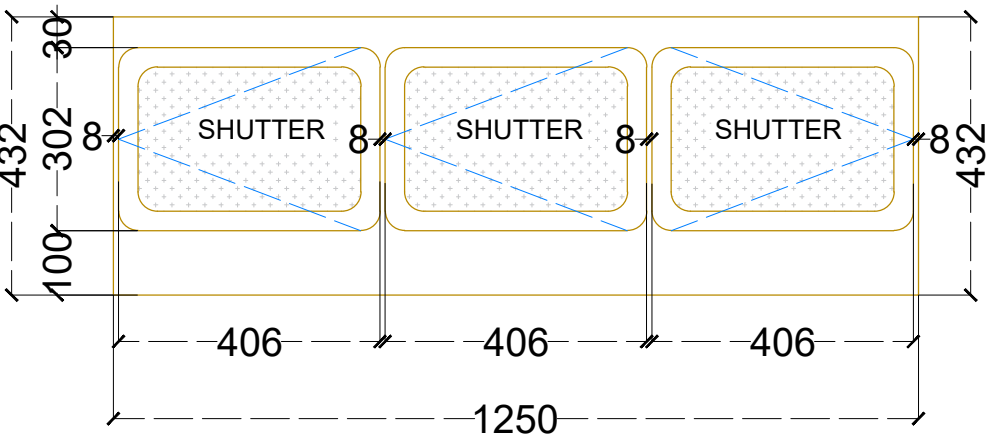

POOJA UNIT - ELEVATION

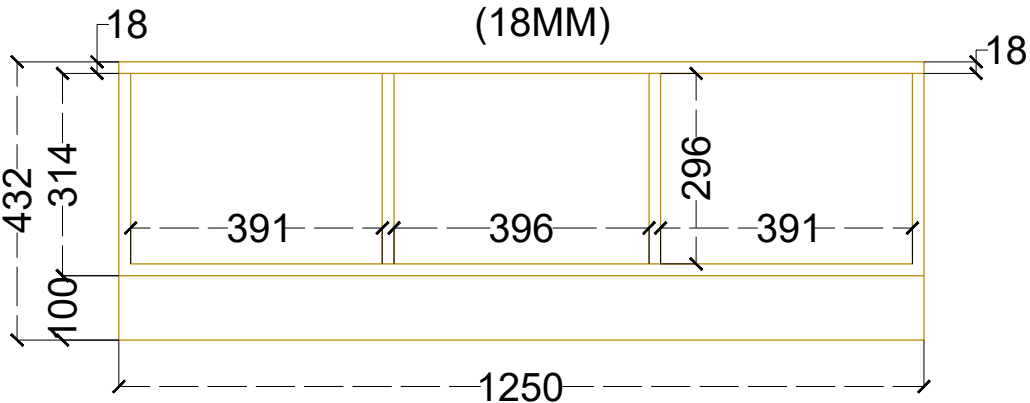

POOJA UNIT - INTERNAL

TITLE : PUJA - UNIT

DISINED BY : JITHESH K

PROPOSED INTERIORS FOR :

DATE : 04/05/2026

CHECKED BY :

PROJECT : DESIRE TREE


PROJECT CODE : M064

HANDOVER DATE :

CLIENT : Mr AMIT



LISNO INDIA PRIVATE LIMITED
H1/1, 402 Asher Enclave, Naigaon (E) Mumbai,
Maharashtra-401208

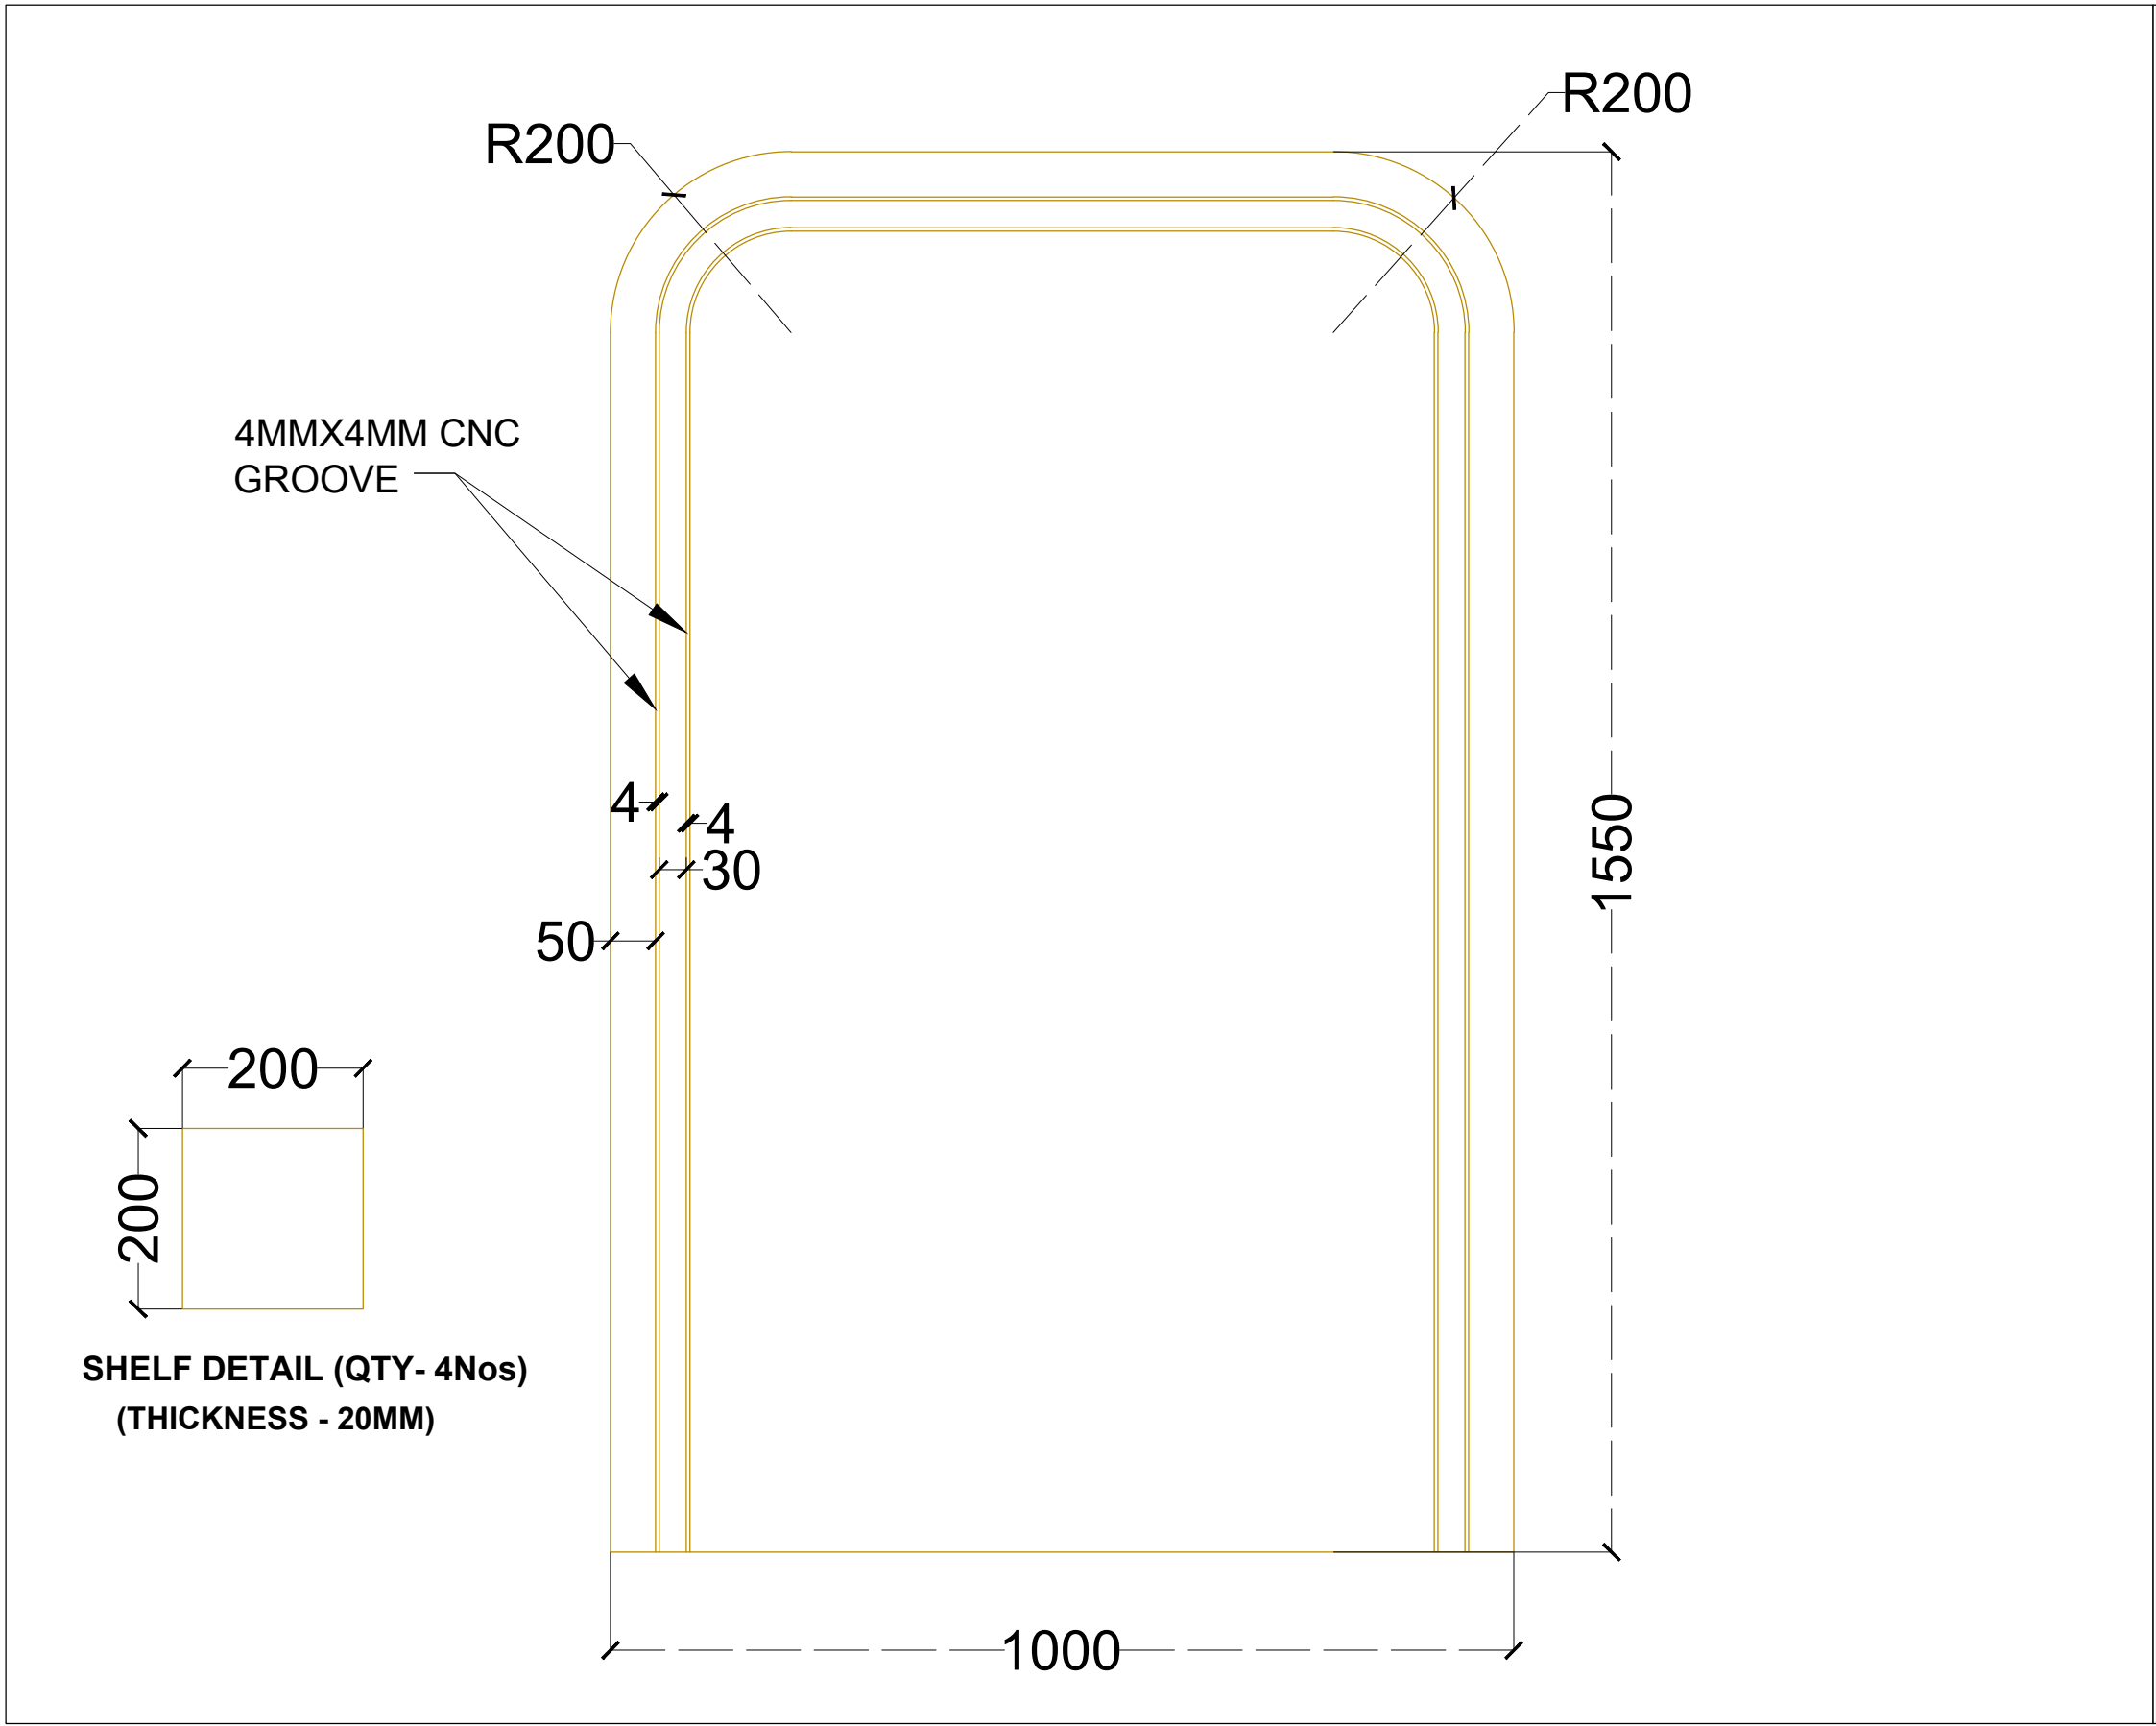


PUJA BACK PANEL - DETAIL SHEET

DRAWER BASE UNIT


CORE MATERIAL	MR ply
EXPOSED SIDE FINISH	CSY 18062 (BEYOND LIMIT STORY)
VISIBLE EDGE BANDING COLOUR	MATCHING WITH LAMINATE

CSY 18062 (BEYOND LIMIT STORY)

TITLE : PUJA BACK PANEL	DISINED BY : JITHESH K	PRAPOSED INTERIORS FOR : PROJECT : DESIRE TREE CLIENT : Mr AMIT	 LISNO INDIA PRIVATE LIMITED H1/1, 402 Asher Enclave, Naigaon (E) Mumbai, Maharashtra-401208
DATE : 04/05/2026	CHECKED BY :		
PROJECT CODE : M064	HANDOVER DATE :		

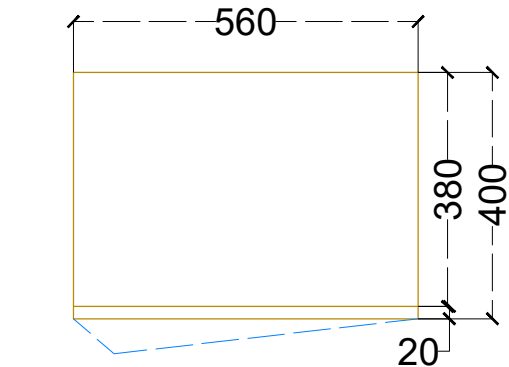


CROCKERY - PLAN

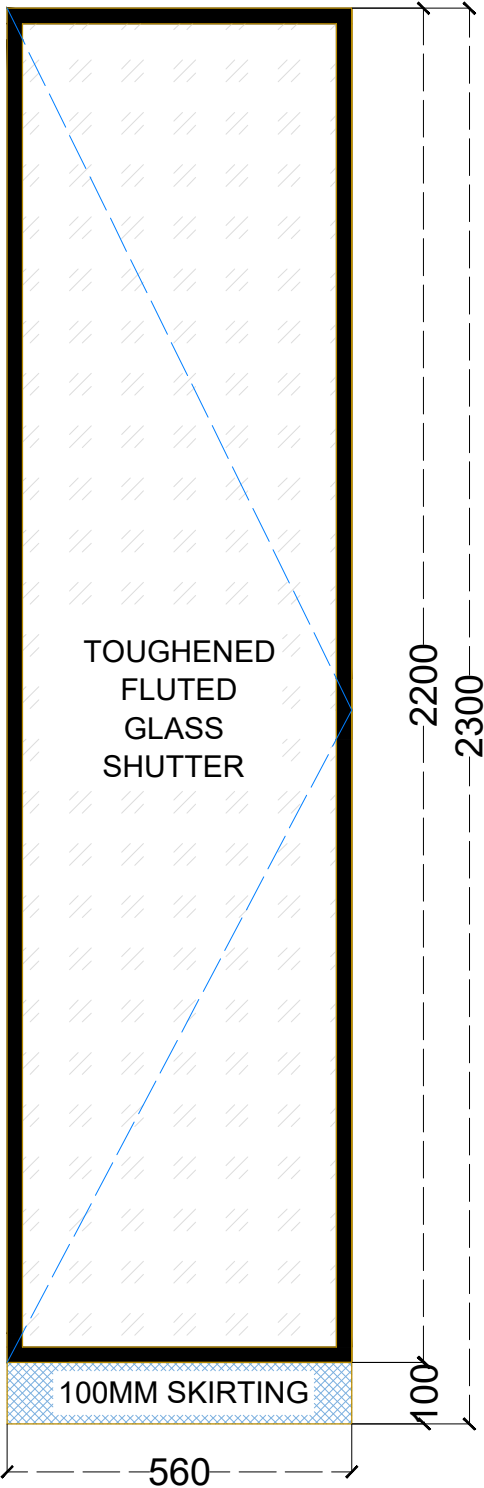

CROCKERY - EXTERNAL

17MM WIDE PROFILE
LIGHT(3000K)
GROOVE FROM
125MM FROM FRONT

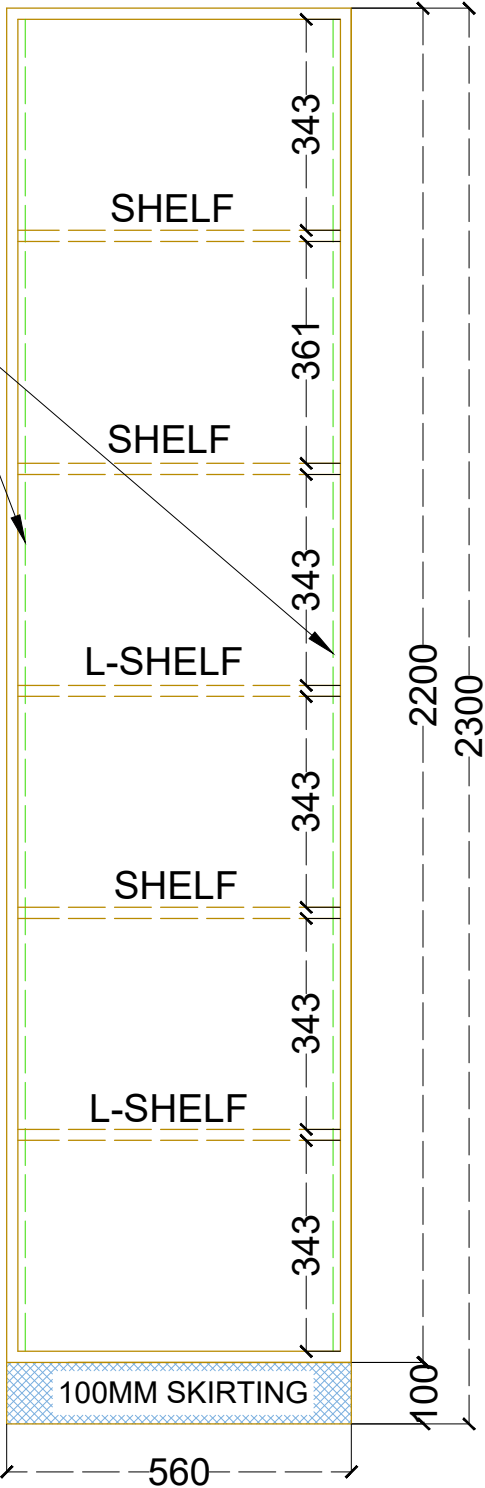

CROCKERY - INTERNAL

CROCKERY UNIT - DETAIL SHEET

TALL UNIT

CORE MATERIAL	MR ply
EXPOSED SIDE FINISH	CSY 18062 (BEYOND LIMIT STORY)
GLASS SHUTTER - GLASS	BLACK TINTED FLUTED (TOUGHENED)
GLASS SHUTTER - PROFILE	BLACK
INTERNAL FINISH	220 MT/SF (SAFE DECOR)
VISIBLE EDGE BANDING COLOUR	MATCHING WITH LAMINATE

SKIRTING

CORE MATERIAL	MR ply
SKIRTING FINISH	CSY 18062 (BEYOND LIMIT STORY)

HANDLE

GLASS SHUTTER	BINDI PROFILE HANDLE	1Nos
---------------	----------------------	------



CSY 18062 (BEYOND LIMIT STORY)




BLACK TINTED FLUTED GLASS
(TOUGHENED)



220 MT/SF (SAFE DECOR)

TITLE : CROCKERY - UNIT	DISINED BY : JITHESH K	PROPOSED INTERIORS FOR : PROJECT : DESIRE TREE CLIENT : Mr AMIT	 LISNO INDIA PRIVATE LIMITED H1/1, 402 Asher Enclave, Naigaon (E) Mumbai, Maharashtra-401208
DATE : 04/05/2026	CHECKED BY :		
PROJECT CODE : M064	HANDOVER DATE :		

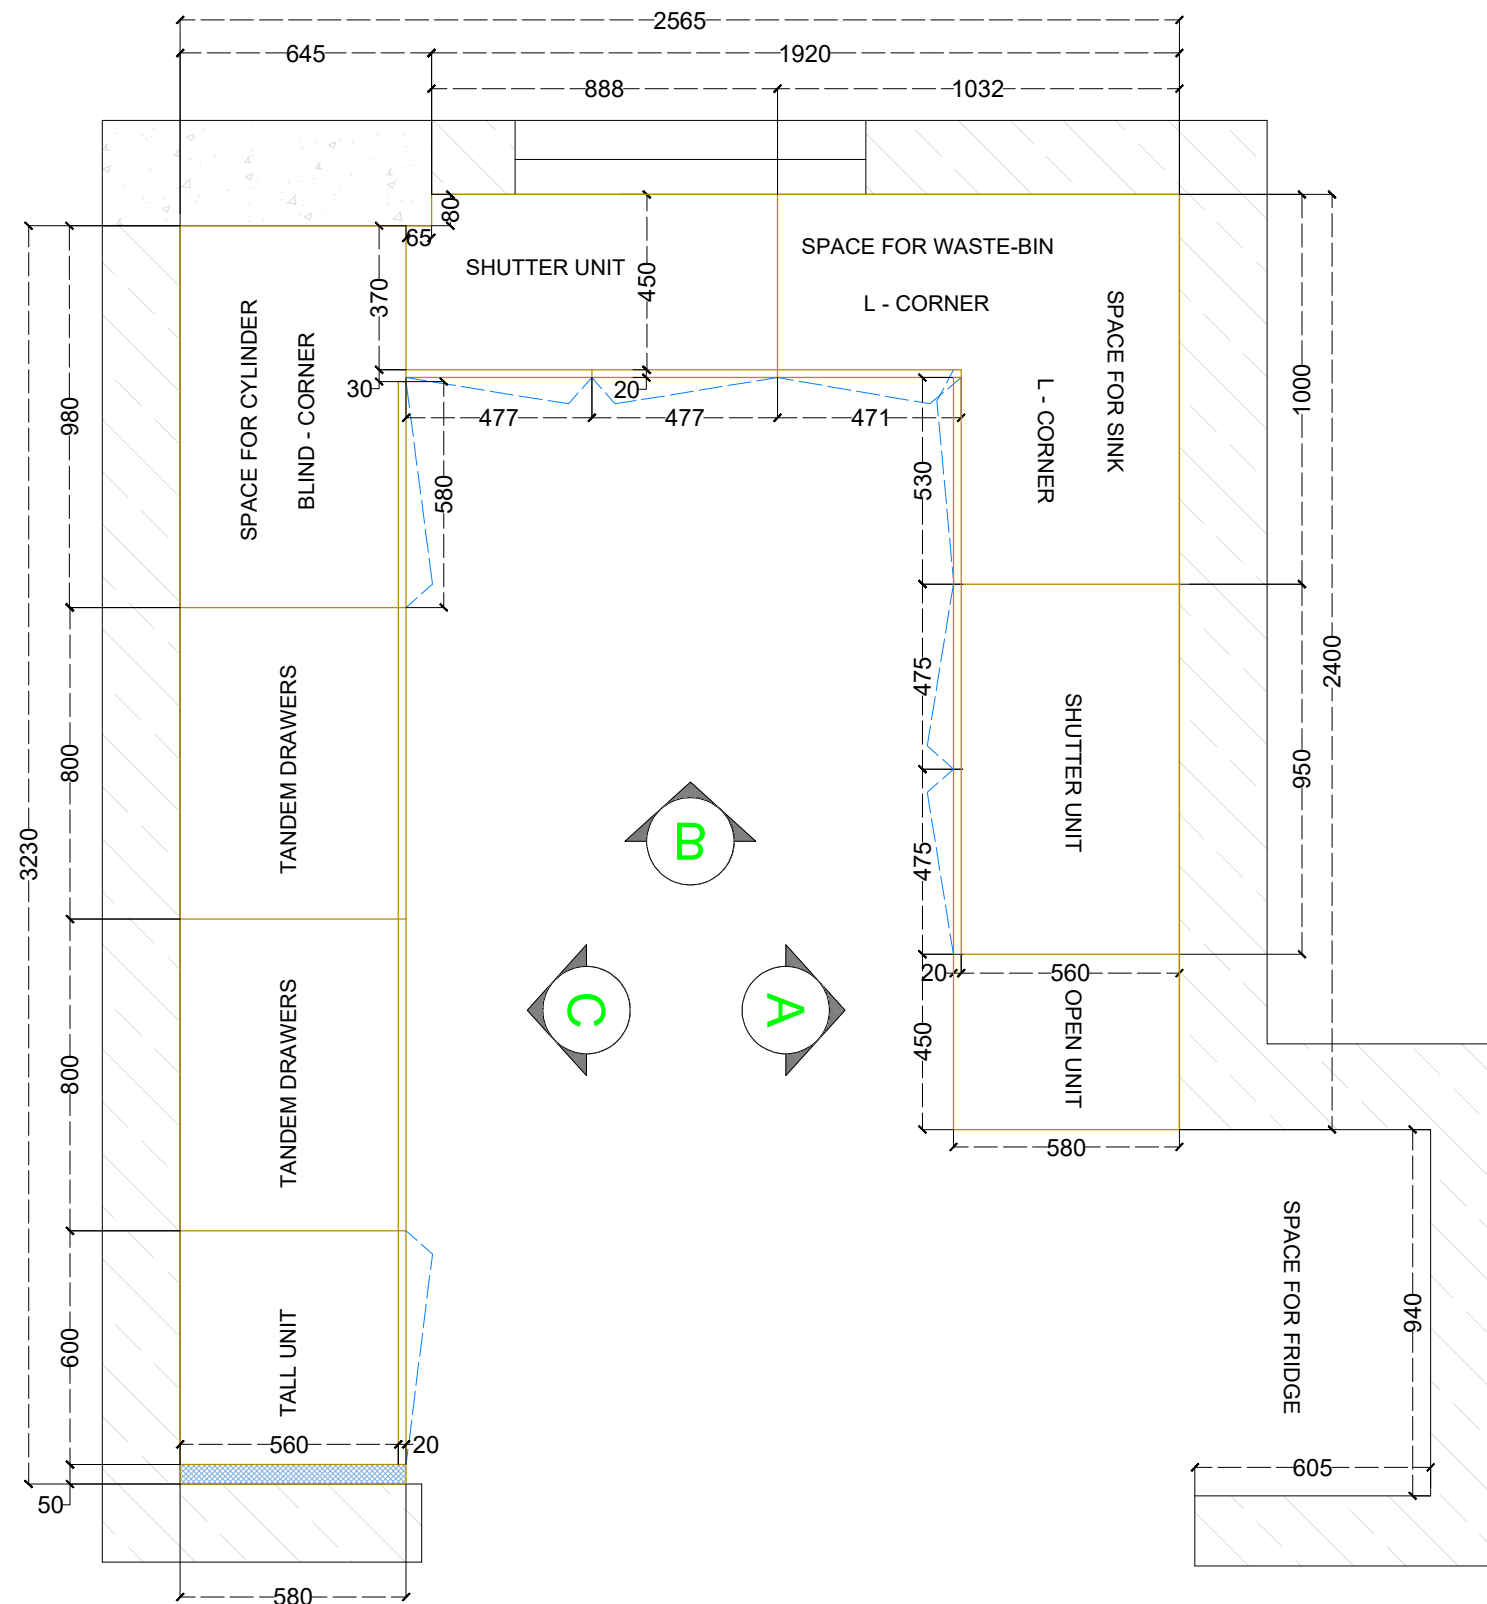


KITCHEN - BASE UNIT PLAN

KITCHEN - DETAIL SHEET




KITCHEN - SHUTTER FIXING DETAIL

BEADING DETAILS (BEADING THICKNESS - 5MM)

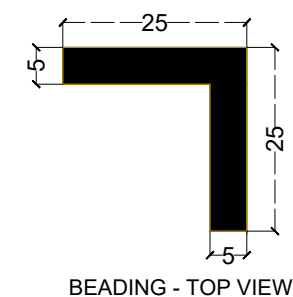

BEADING - TOP VIEW

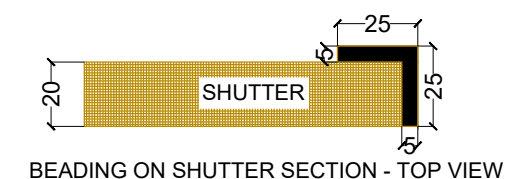

BEADING ON SHUTTER SECTION - TOP VIEW

TITLE : KITCHEN

DATE : 04/05/2026

PROJECT CODE : M064

DISINED BY : JITHESH K

CHECKED BY :

HANDOVER DATE :

PROPOSED INTERIORS FOR :

PROJECT : DESIRE TREE

CLIENT : Mr AMIT



LISNO INDIA PRIVATE LIMITED
H1/1, 402 Asher Enclave, Naigaon (E) Mumbai,
Maharashtra-401208